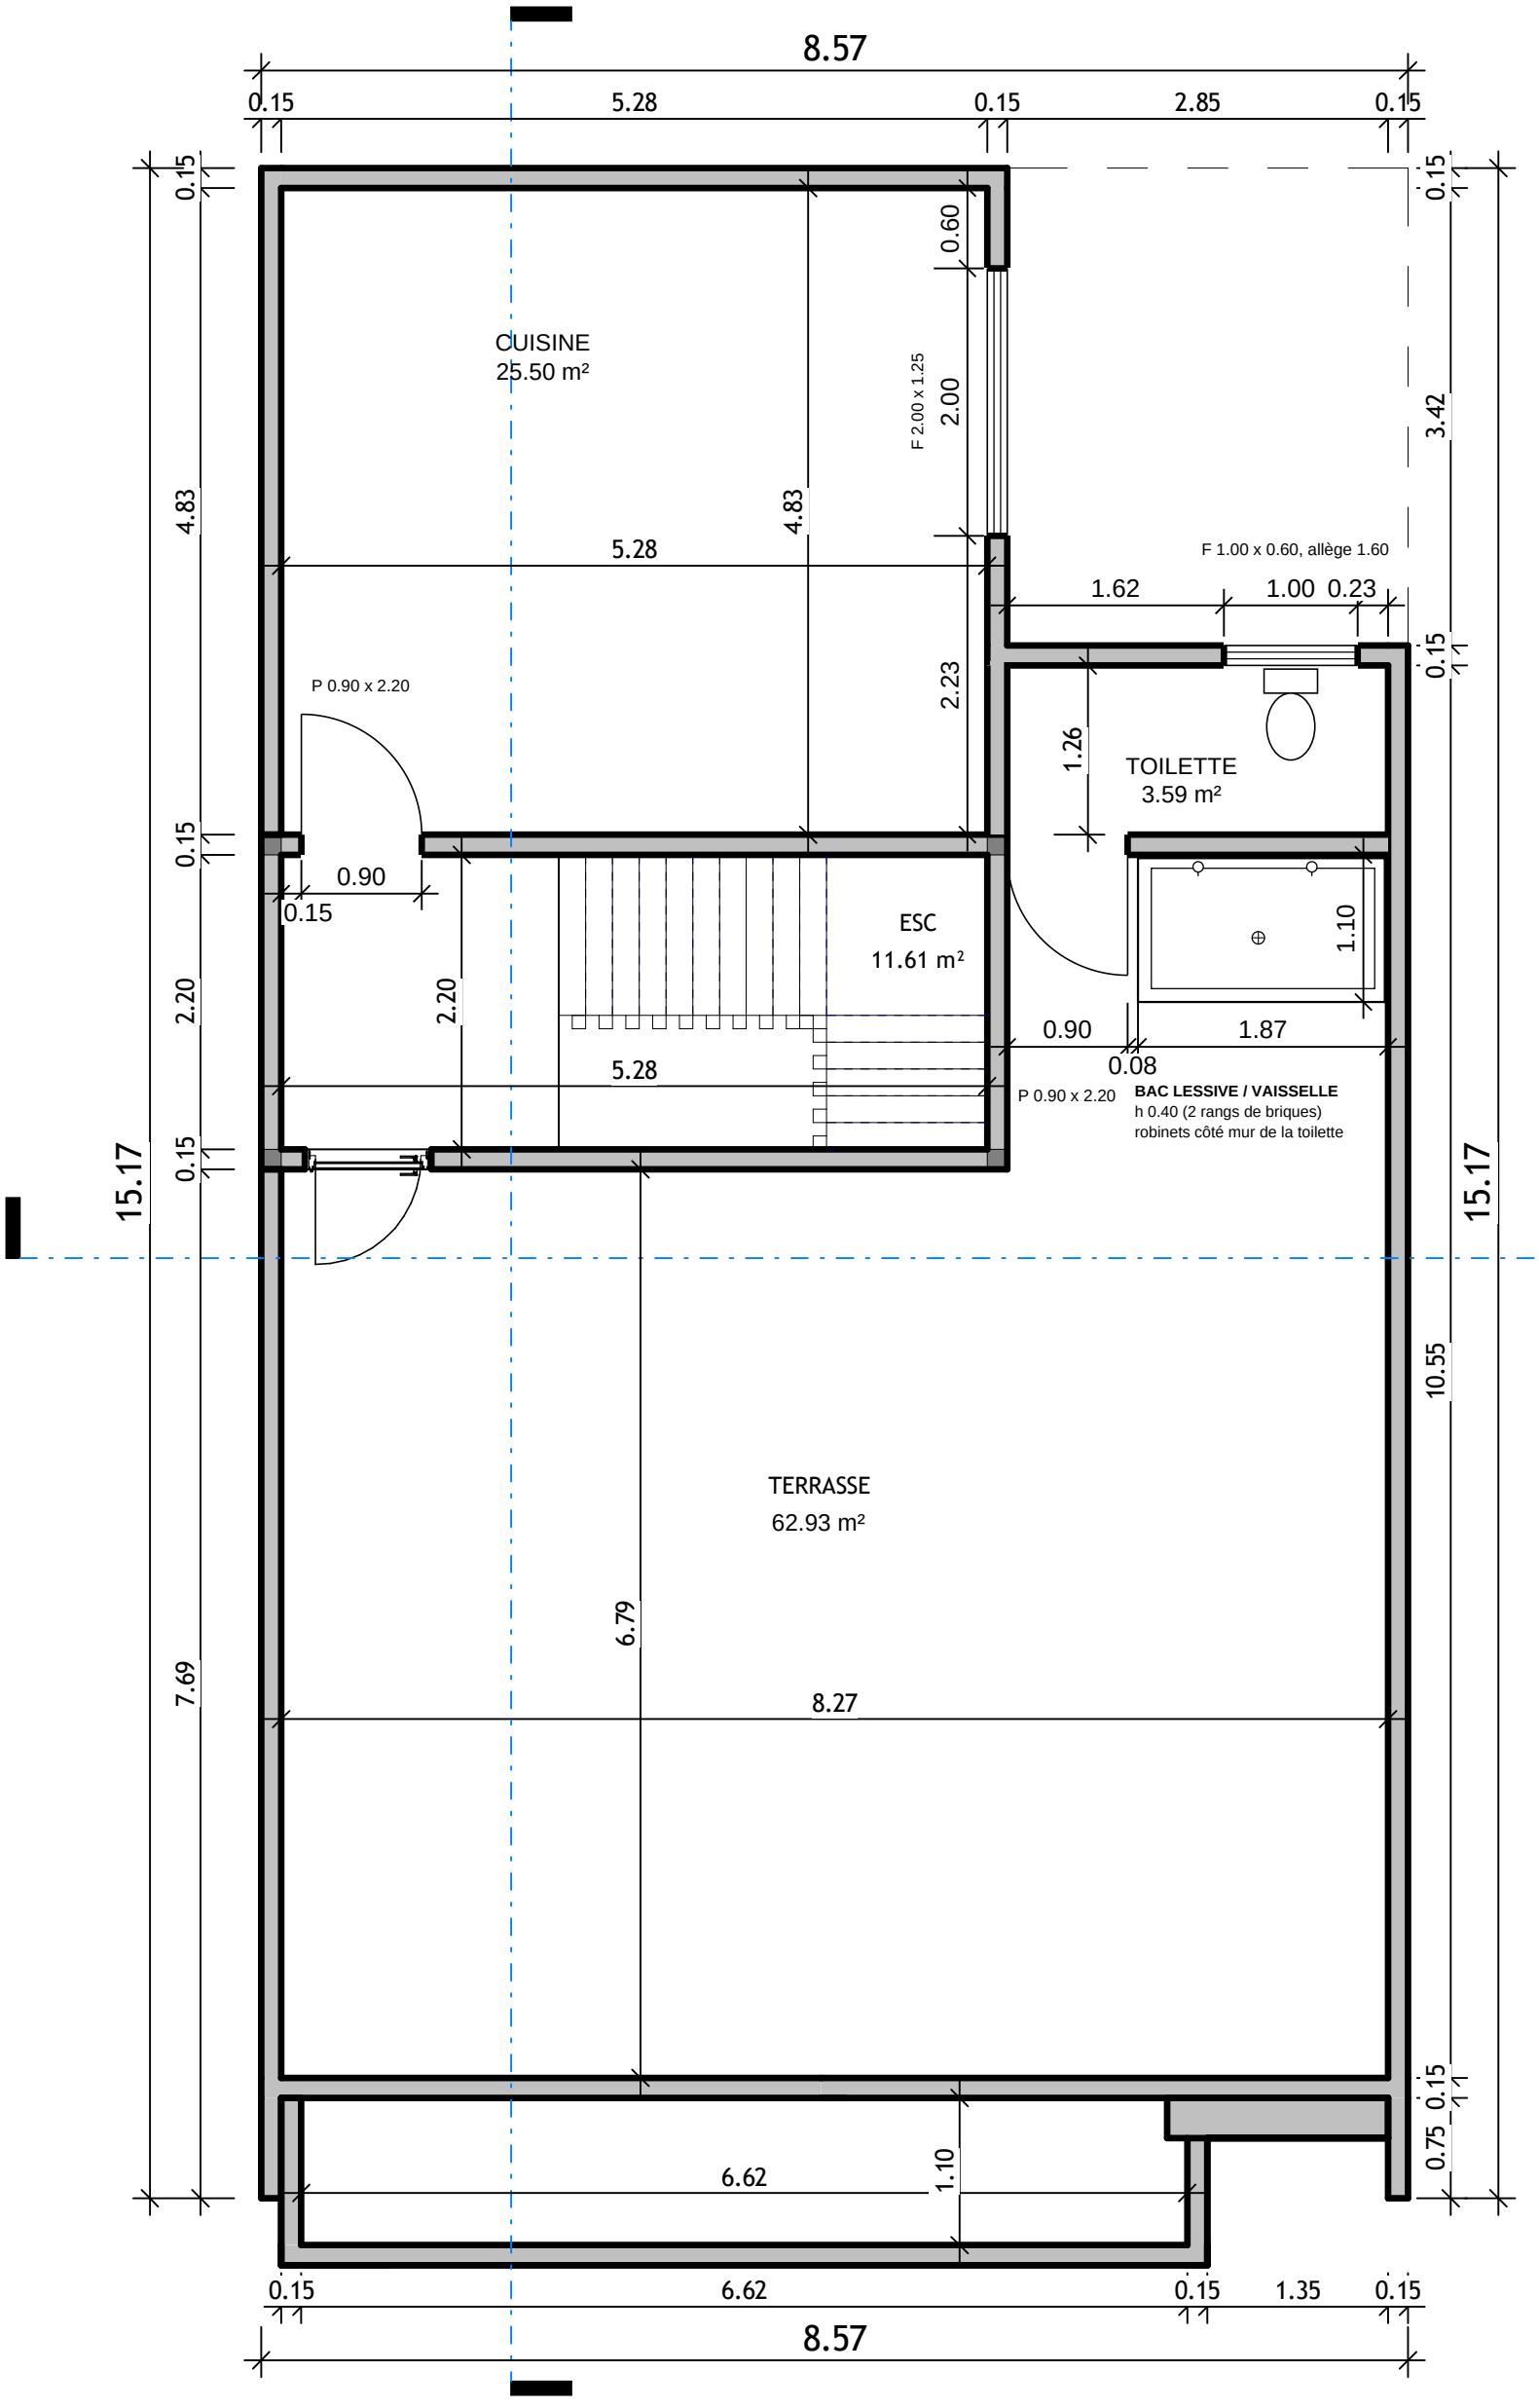


MAITRE D'OUVRAGE:

MOHAMED BADIANE

PROJET:

PROJET DE CONSTRUCTION D UNE VILLA RESIDENTIELLE SIS A MBAO

TITRE: **TERRASSE COTÉ - IND. A**

ECH: 1 : 50	DWG No: 019	CAD: APS
DWR: E.H.S.F	DATE DE FIN 05/11/26	

D&F ENGINEERING
Confort at home
Tel (+221) 76-141-32-23
Tel (+221) 77-234-03-20
Email: dnfengineeringsav@gmail.com

TERRASSE - TABLEAU DES PIÈCES ET DES MENUISERIES

Maître d'ouvrage : Mohamed BADIANE - Projet de construction d'une villa résidentielle à Mbao - D&F ENGINEERING - Indice A du 05/11/2026

PIÈCE	DIMENSIONS (m)	SURFACE (m²)	PÉRIMÈTRE (m)
CUISINE	5.28 x 4.83	**25.50**	20.22
TOILETTE	2.85 x 1.26	**3.59**	8.22
ESC	5.28 x 2.20	**11.61**	14.96
TERRASSE	forme en L (voir plan)	**62.93**	34.84
BAC (ouvrage)	1.87 x 1.10, h 0.40	2.06	5.94

- Surface = surface nette, mesurée à l'intérieur des murs (faces des murs) ; périmètre = contour des faces intérieures, ouvertures non déduites.
- CUISINE et TOILETTE : cotes du plan (5.28 x 4.83 ; 2.85 x 1.26). ESC : surface 11.61 du plan d'origine, inchangée (5.28 x 2.20 = 11.62).
- TERRASSE : polygone relevé sur le vectoriel (échelle 51.5 pt/m) ; le bac (2.06) est compris dans la surface, surface libre = 60.87.
- Le seuil de la porte de la toilette ferme le polygone de la terrasse au droit de l'ouverture (pas de surface d'ouverture comptée).

MENUISERIES

REP.	LOCAL	MUR / POSITION	L x H (m)	ALLÈGE	OUVRANT
F1	CUISINE	mur est, x 0.60 de l'angle nord	2.00 x 1.25	à confirmer	à définir
P1	CUISINE	mur sud (vers ESC), 0.15 de l'angle ouest	0.90 x 2.20	-	vers la cuisine
F2	TOILETTE	mur nord, 1.62 de l'angle ouest	1.00 x 0.60	1.60 (tête 2.20)	à définir
P2	TOILETTE	mur sud, côté ouest	0.90 x 2.20	-	vers la terrasse

- Dimensions L x H en mètres. Allège de F1 non donnée : 0.95 proposée (tête 2.20, comme P1/P2) ; allège de F2 : 1.60 (tête 2.20), à confirmer.

POINTS À SIGNALER

- Murs neufs en maçonnerie de 0.15 (comme les murs existants), faces dans le prolongement exact des murs voisins (contrôle des raccords).
- Bac lessive / vaisselle : maçonnerie de briques, 2 rangs soit h 0.40 ; robinets contre le mur de la toilette (alimentation par ce mur) ; décalé à 0.08 de l'ouvrant de la porte de la toilette (battant ouvert à 90°).
- POINTS DE L'INGÉNIEUR : (a) fermeture de la cuisine : murs neufs 0.15 à ancrer au mur existant ; (b) baie 2.00 dans le mur est existant : linteau, appuis 0.20, sous la poutre ;
- (c) fenêtre 1.00 x 0.60 de la toilette et portes 0.90 x 2.20 : linteaux ; (d) évacuations (WC, bac, cuisine) et étanchéité de la terrasse sous le bac et le long des murs neufs.
- Plan sous réserve du relevé sur site et du visa de l'ingénieur de structure. Cotes en mètres, échelle 1:50 pour le plan (page 1).

MAITRE D'OUVRAGE:

MOHAMED BADIANE

PROJET:

PROJET DE CONSTRUCTION D UNE VILLA RESIDENTIELLE SIS A MBAO

TITRE: **TERRASSE COTÉ - IND. A**

ECH: 1 : 50 | DWG No: 019 | CAD: APS

DWR: E.H.S.F | DATE DE FIN 05/11/26

D&F ENGINEERING
Confort at home
Tel (+221) 76-141-32-23
Tel (+221) 77-234-03-20
Email: dnfengineeringsav@gmail.com