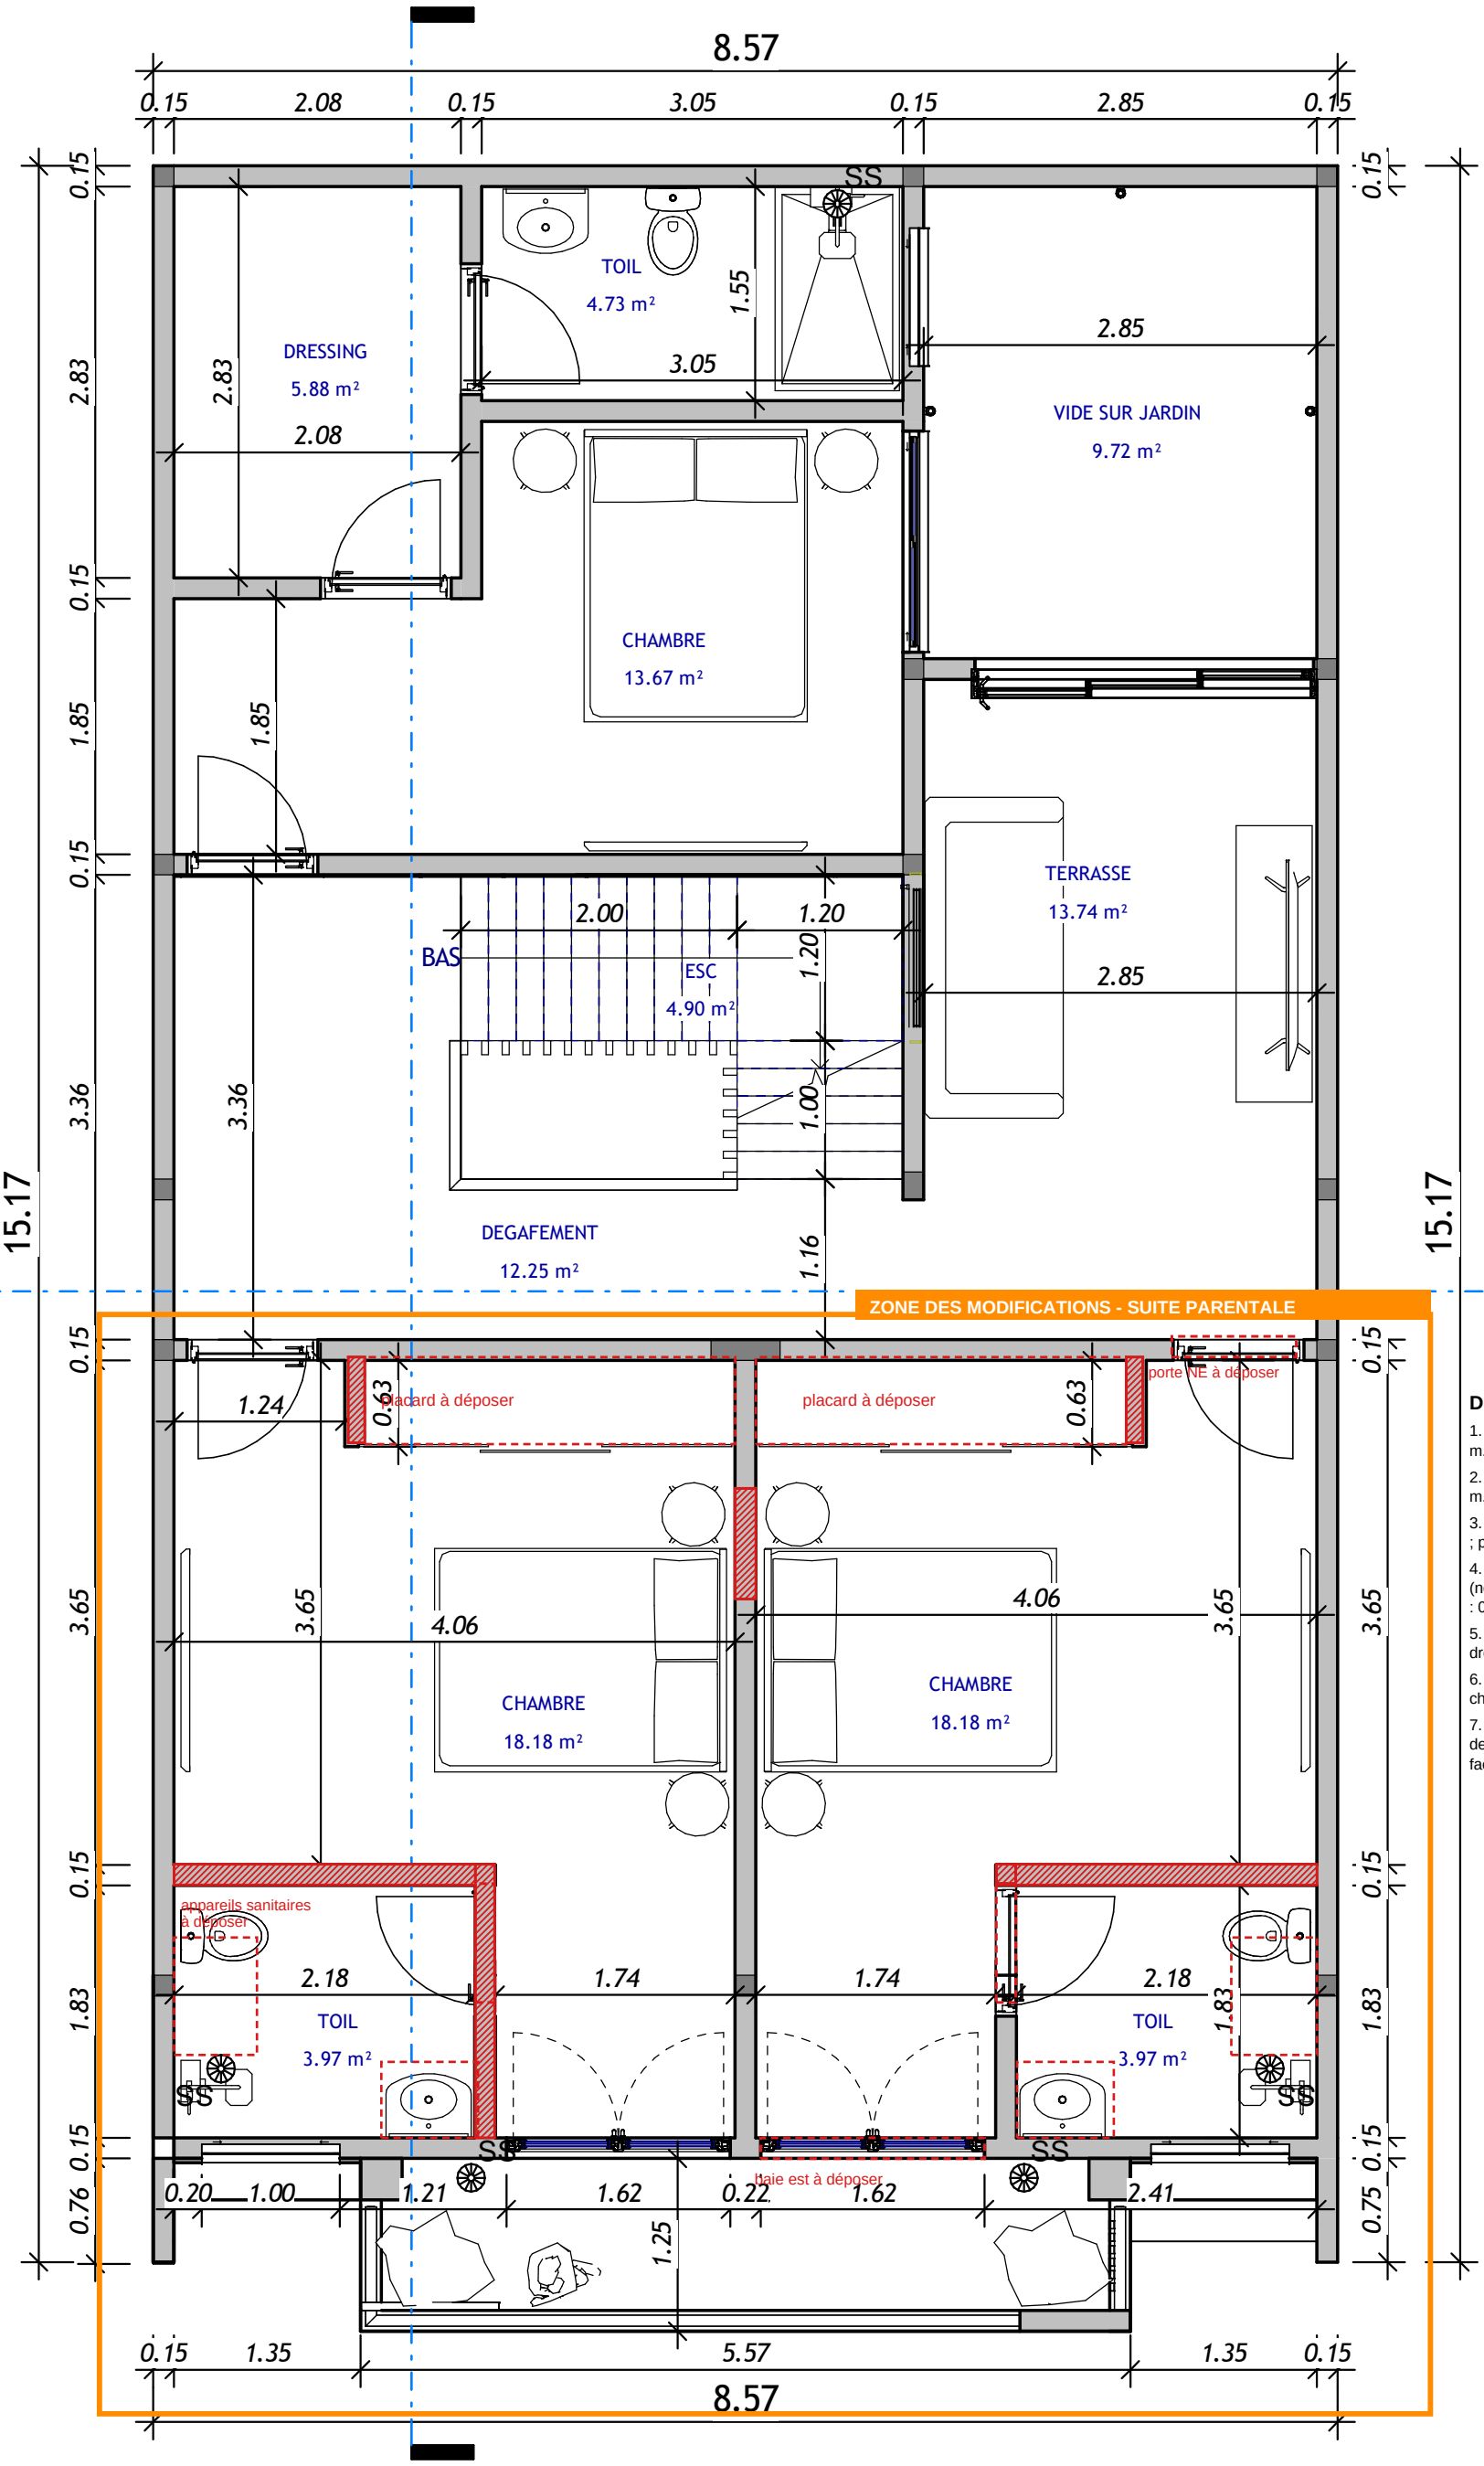


LÉGENDE

Cadre orange : zone des modifications (deux chambres miroirs du R+1).

Hachures rouges : cloison ou mur à démolir.

Pointillé rouge : élément à déposer (placard, sanitaire, porte, baie).

Gris : existant conservé.

Les poteaux, les poutres et les dalles ne sont pas touchés.

DÉMOLITIONS

1. Cloison nord du WC ouest, 2.32 m.
2. Cloison est du WC ouest, 1.98 m.
3. Cloison nord du WC est, 2.32 m ; petit retour du mur ouest, 0.14 m.
4. Percement de la cloison centrale (non porteuse, sous la poutre B14) : 0.80 m, linteau à prévoir.
5. Deux petits murs de l'ancien dressing : 0.62 m chacun.
6. Placards coulissants des deux chambres.
7. Appareils sanitaires, deux portes de WC, porte NE, baie est de façade.

Maitre d'ouvrage:

Mohamed BADIANE


Projet:

PROJET DE CONSTRUCTION D UNE VILLA RESIDENTIELLE SIS A MBAO

Titre: R+1 - DEMOLITIONS

02/11/26	DWG No: 016	Cad APS
DWR E.H.S.F	ECH: 1 : 50	

D&F ENGINEERING
Confort at home
Tel (+221) 76-141-32-23
Tel (+221) 77-234-03-20
Email: dnfengineeringsav@gmail.com

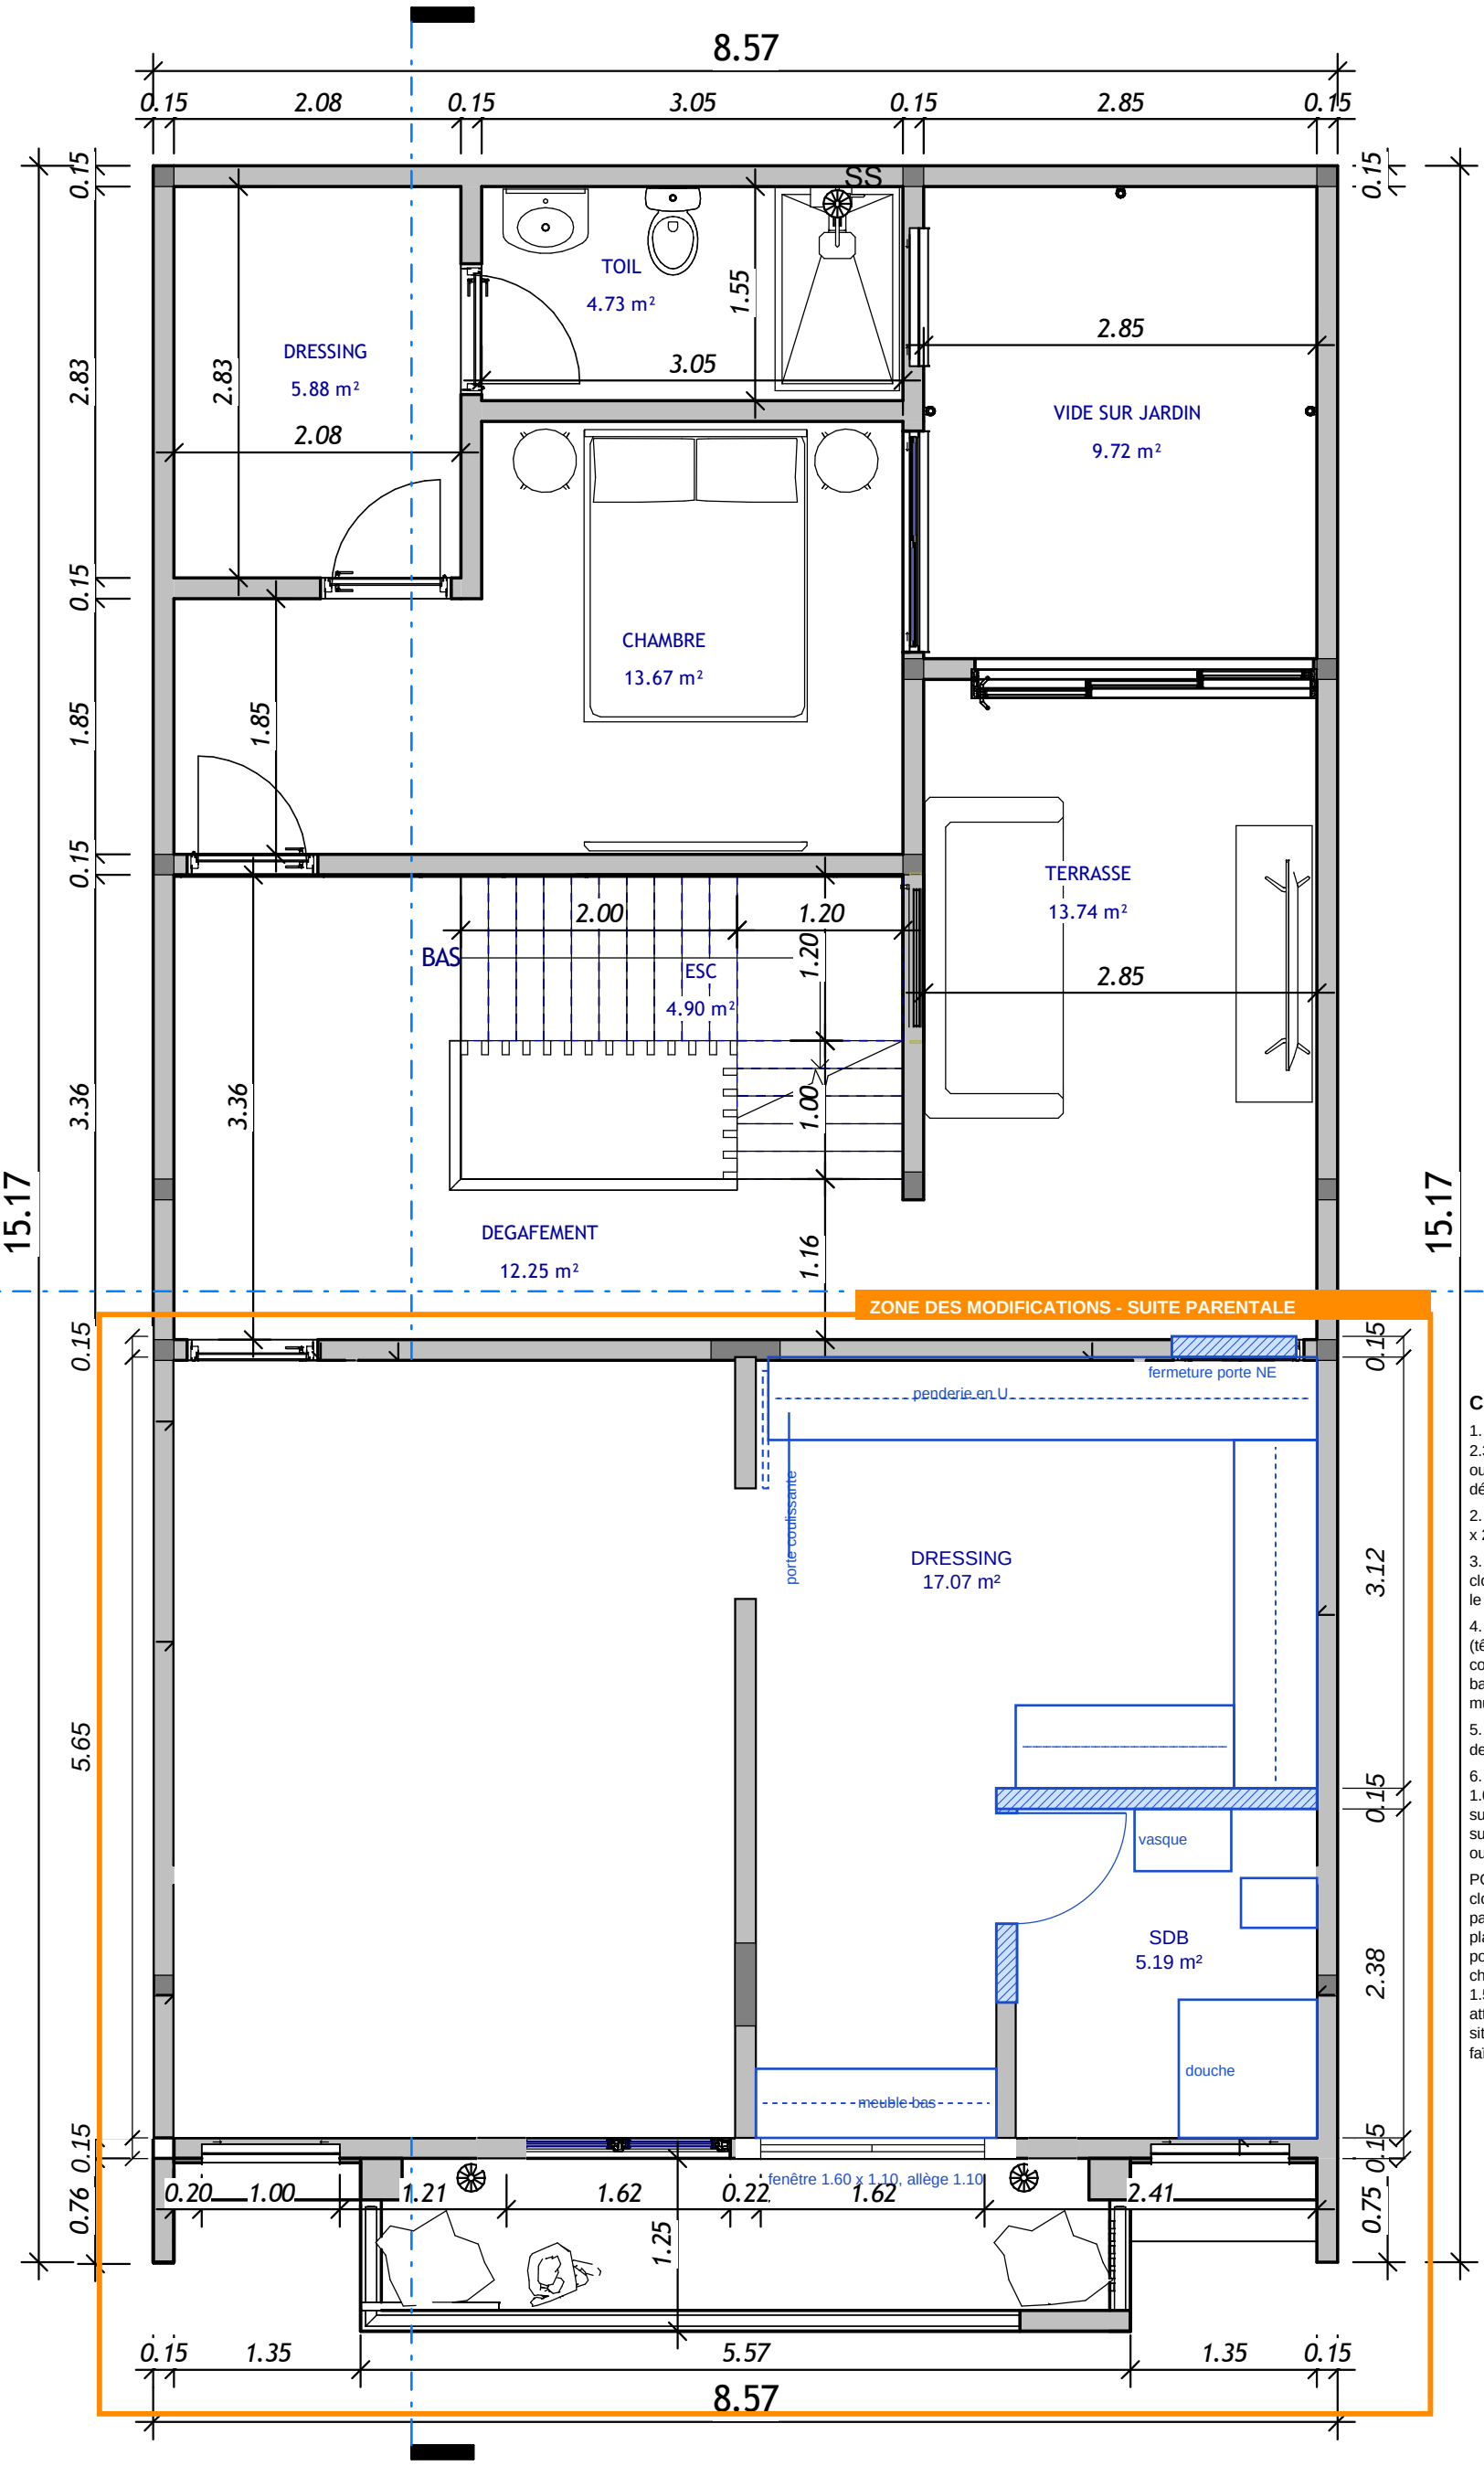

LÉGENDE

Cadre orange : zone des modifications (deux chambres miroirs du R+1).

Bleu hachuré : mur ou cloison à construire (épaisseur 0.15).

Contour bleu : menuiserie, appareil ou agencement neuf.

Gris : existant conservé.

Mobilier non figuré (voir le projet final).

CONSTRUCTIONS

1. Cloison nord de la salle de bain, 2.32 m, à 2.38 de la façade ; mur ouest prolongé de 1.22 m (porte déplacée à 1.55-2.35).

2. Fermeture de la porte NE (0.90 x 2.20) en maçonnerie.

3. Porte coulissante 0.80 dans la cloison centrale, vantail rangé vers le nord derrière la penderie.

4. Fenêtre 1.60 x 1.10, allège 1.10 (tête 2.20, linteau de la baie conservé), dans l'ouverture de la baie est ; meuble bas 1.74 x 0.50 mur à mur.

5. Penderie en U (nord, est, mur de la salle de bain), sans îlot.

6. Salle de bain : douche 1.00 x 1.00 avec paroi vitrée côté WC, WC suspendu, meuble vasque suspendu 0.70 ; porte 0.80, vantail ouvert contre le mur nord.

POINTS DE L'INGÉNIEUR : (a) cloison nord de la salle de bain parallèle aux nervures 12+8 du plancher, à 0.55 de l'ancienne : poutrelle doublée ou calcul de charge ; (b) linteau neuf de la porte 1.55-2.35 avec appuis de 0.20 ; (c) attentes de plomberie à relever sur site (WC déplacé) ; (d) étanchéité sous faïence toute hauteur côté vasque.

Maitre d'ouvrage:

Mohamed BADIANE


Projet:

PROJET DE CONSTRUCTION D UNE VILLA RESIDENTIELLE SIS A MBAO

Titre: R+1 - CONSTRUCTIONS

02/11/26	DWG No: 017	Cad APS
DWR E.H.S.F	ECH: 1 : 50	

D&F ENGINEERING
Confort at home
Tel (+221) 76-141-32-23
Tel (+221) 77-234-03-20
Email: dnfengineeringsav@gmail.com

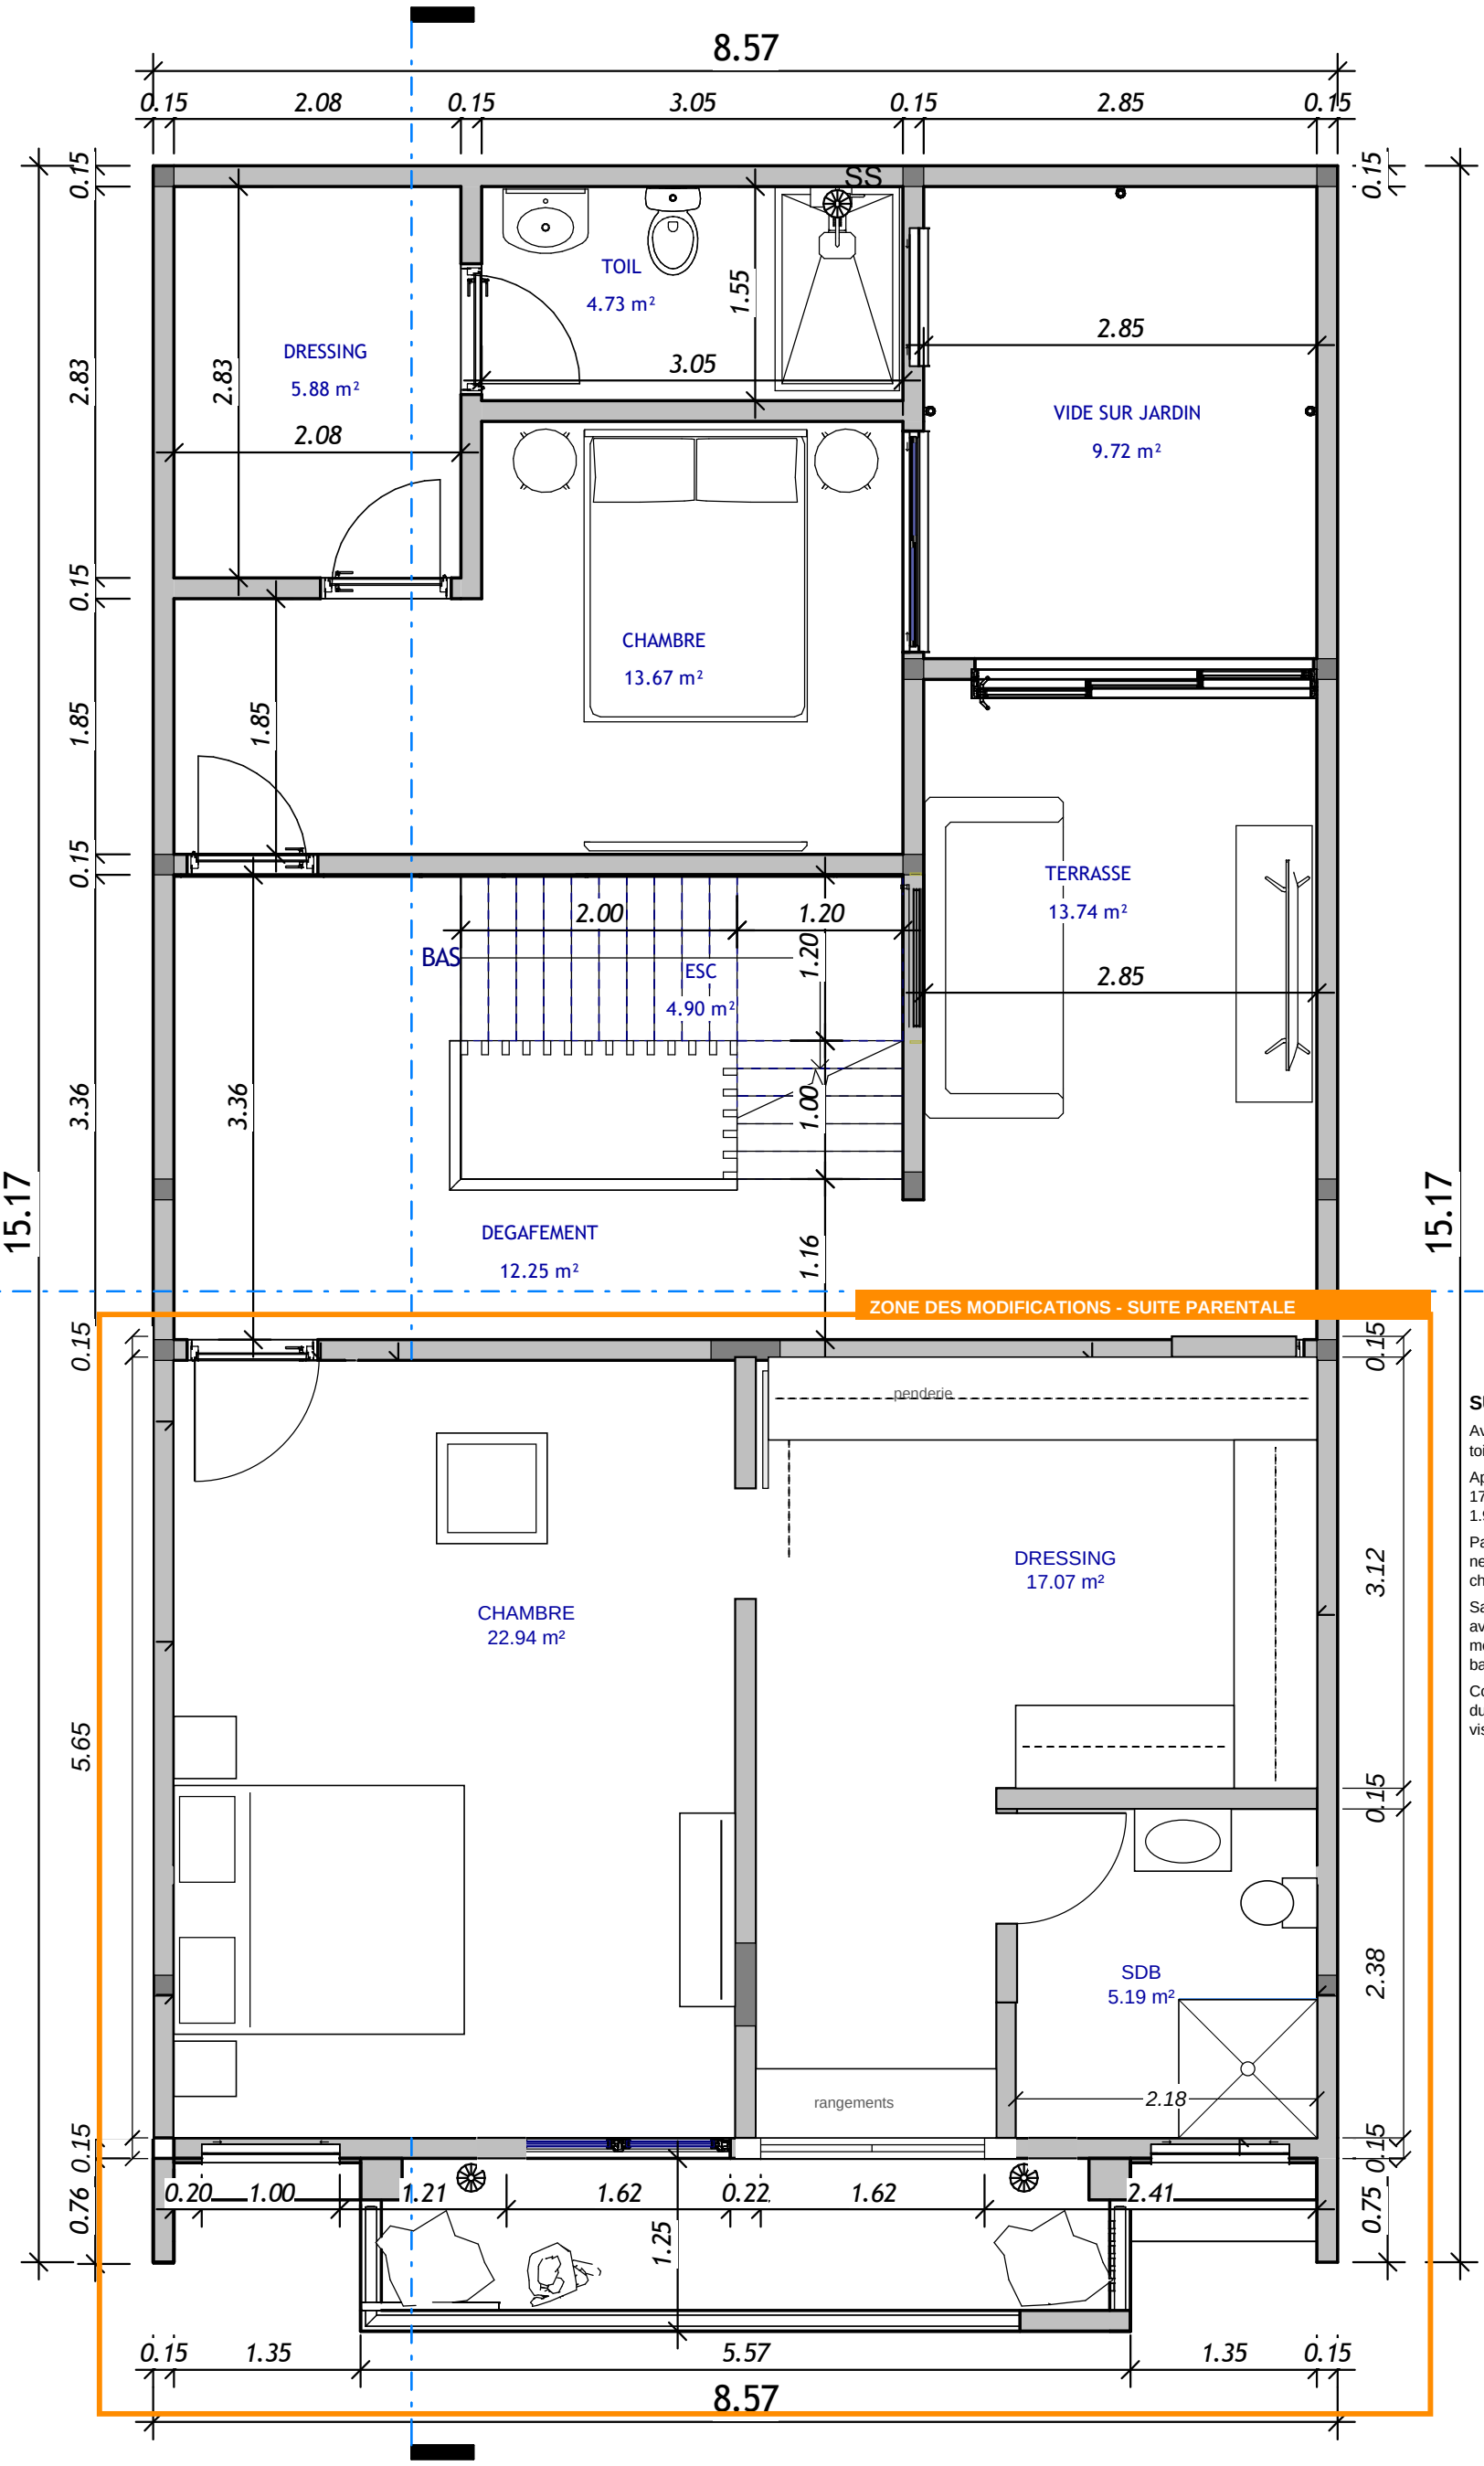

LÉGENDE

Cadre orange : zone des modifications (deux chambres miroirs du R+1 transformées en une suite parentale).

Parcours : chambre, dressing, salle de bain ; une seule porte depuis la chambre.

Lumière et air naturels : fenêtre 1.60 x 1.10 pour le dressing, fenêtre 1.00 pour la salle de bain (châssis fixe dépoli ou soufflet haut au-dessus de la douche).

SURFACES NETTES (m²)

Avant : 2 chambres de 18.18 et 2 toilettes de 3.97.

Après : chambre 22.94 ; dressing 17.07 (penderie en U, allée centrale 1.92) ; salle de bain 5.19.

Pas d'îlot : un îlot de 1.00 de large ne laisse pas 0.90 de passage de chaque côté.

Salle de bain : douche 1.00 x 1.00 avec paroi vitrée côté WC, WC et meuble vasque suspendus, pas de baignoire.

Cotes en mètres. Plan sous réserve du relevé des attentes sur site et du visa de l'ingénieur de structure.

Maitre d'ouvrage:

Mohamed BADIANE

Projet:

PROJET DE CONSTRUCTION D UNE VILLA RESIDENTIELLE SIS A MBAO

Titre: R+1 - PROJET FINAL

02/11/26	DWG No: 018	Cad APS
DWR E.H.S.F	ECH: 1 : 50	

D&F ENGINEERING
Confort at home
Tel (+221) 76-141-32-23
Tel (+221) 77-234-03-20
Email: dnfengineeringsav@gmail.com