

EXISTANT - R+1 : deux chambres miroirs (extrait du plan V2)

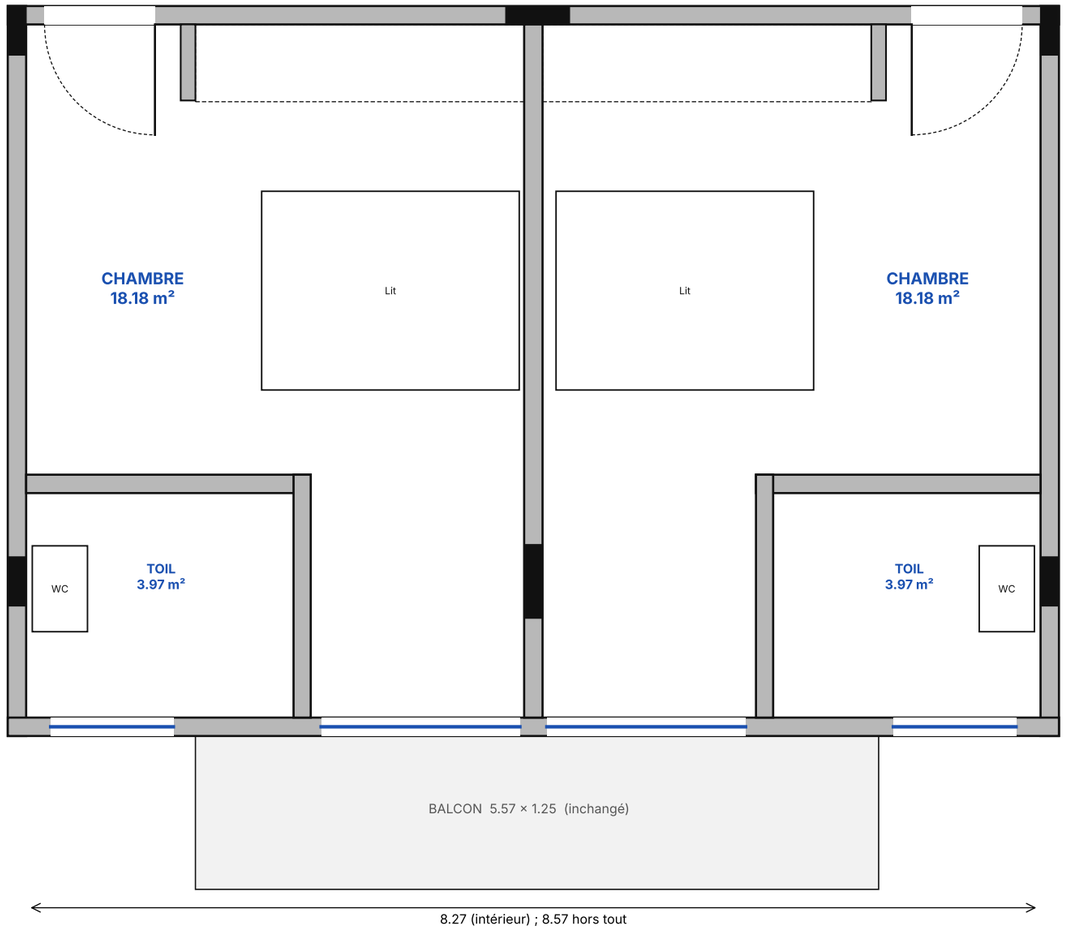

PROPOSITION A - suite parentale : chambre, salle de bain, walk-in dressing

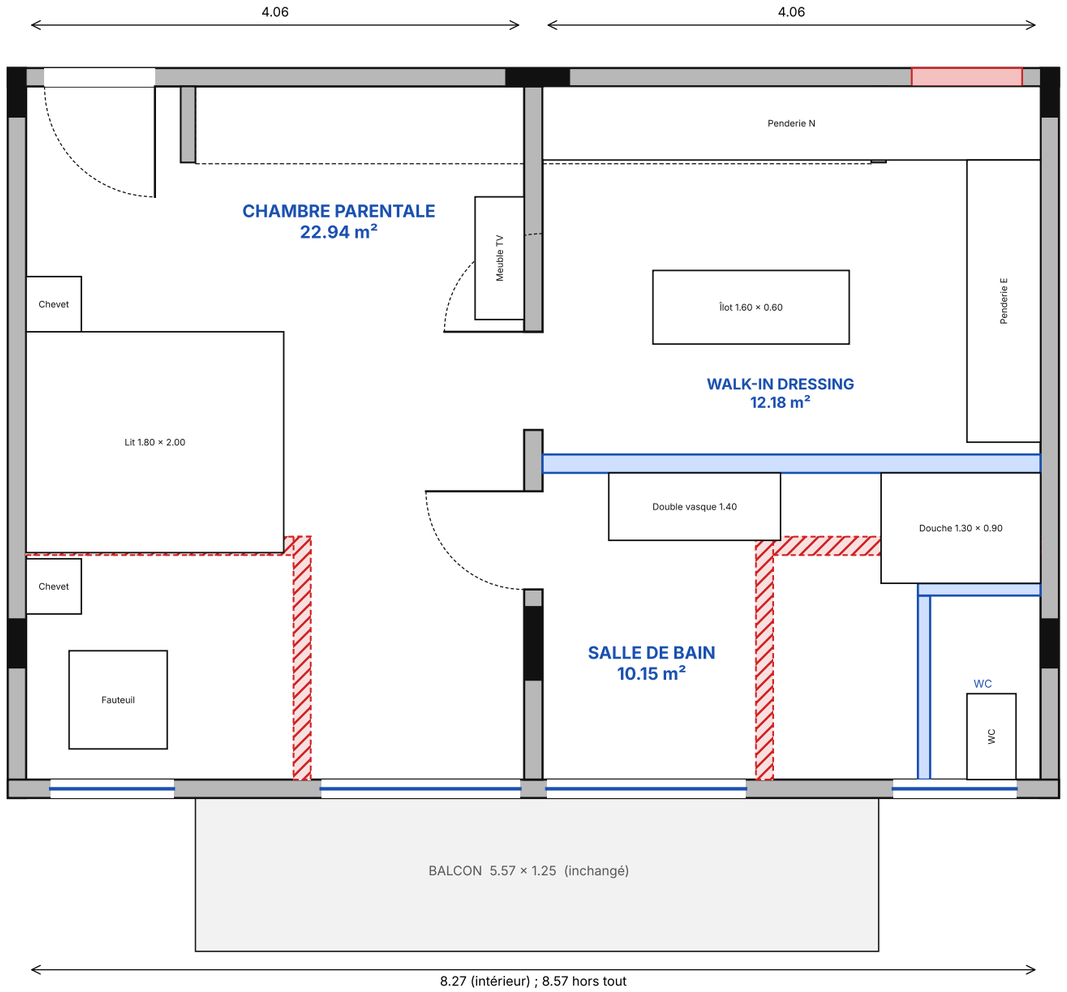


```
CONTRÔLE DES DÉGAGEMENTS (règles de l'atelier) : 16 contrôles, 0 échec(s)
CIR-013  Dressing : allée îlot / penderie nord                0.90 m (mini 0.90)  OK
CIR-013  Dressing : allée îlot / penderie est                 0.96 m (mini 0.90)  OK
CIR-013  Dressing : allée îlot / mur ouest (côté porte)       0.90 m (mini 0.90)  OK
CIR-013  Dressing : allée îlot / cloison sud                  0.90 m (mini 0.90)  OK
CIR-004  Chambre : côté sud du lit (chevet compris, hors chevet)  0.80 m (mini 0.60)  OK
CIR-004  Chambre : côté nord du lit / mur                     0.92 m (mini 0.70)  OK
CIR-005  Chambre : pied du lit / meuble TV                    1.56 m (mini 0.70)  OK
CIR-003  Chambre : devant le placard coulissant (chevet nord)  1.31 m (mini 0.70)  OK
CIR-019  SDB : devant la double vasque                        1.95 m (mini 0.70)  OK
CIR-020  SDB : approche de la douche 0.70                     0.82 m (mini 0.70)  OK
CIR-018  WC : libre devant la cuvette (cabinet fermé 1.50)    0.80 m (mini 0.60)  OK
CIR-030  Porte SDB : manœuvre côté chambre (0.80) / lit       1.16 m (mini 0.00)  OK
CIR-002  Chambre : fauteuil / chevet sud (ponctuel)           0.30 m (mini 0.30)  OK
CHB-005  Chambre : surface (m2) et largeur 4.06 >= 2.70      22.94 m (mini 9.00)  OK
SDE-005  Douche italienne >= 1.20 x 0.90 (1.30 x 0.90)        1.30 m (mini 1.20)  OK
SDE-007  WC : axe à >= 0.40 des murs (cabinet 0.90 : 0.45)    0.45 m (mini 0.40)  OK
```

MODIFICATIONS (hors structure : aucun poteau, aucune poutre, aucune dalle touchés)
- démolir 4 cloisons légères : les deux petits WC (x4) ;
- construire 3 cloisons légères : séparation SDB / dressing, cabinet WC ;
- percer 2 portes 0.80 dans la cloison centrale (conservée, linteaux) ;
- fermer la porte NE (maçonnerie 0.90 × 2.20) ; façade, balcon, baies : inchangés ;
- plomberie : WC ouest déposé et bouché ; SDB sur l'emplacement du WC est ;
- baie de la SDB : vitrage dépoli (intimité), reste ouvrante ; VMC dressing.

Légende : rouge hachuré = démolition ; bleu = neuf ; rouge plein = fermeture.

Maître d'ouvrage : Mohamed BADIANE

Projet de construction d'une villa résidentielle sis à MBAO

R+1 - SUITE PARENTALE - PROPOSITION A

Échelle 1:50 (A3) - cotes en mètres - APS - indice A - 02/11/2026

dnfengineeringsav@gmail.com · 76 235 64 39 / 76 141 32 23

Scat Urbam Villa 67h 17086 Dakar / Liberté

D&F ENGINEERING