

MAITRE D'OUVRAGE:

MOHAMED BADIANE

PROJET:

PROJET DE CONSTRUCTION D UNE VILLA RESIDENTIELLE SIS A MBAO

TITRE: 3D FACADE

ECH:	DWG No: 001	CAD: APS
DWR:	DATE DE FIN	

D&F ENGINEERING
Confort at home
Tel (+221) 76-141-32-23
Tel (+221) 77-234-03-20
Email: dnfengineeringsav@gmail.com



MAITRE D'OUVRAGE:

MOHAMED BADIANE

PROJET:

PROJET DE CONSTRUCTION D UNE VILLA RESIDENTIELLE SIS A MBAO

TITRE: 3D FACADE

ECH:	DWG No: 002	CAD: APS
DWR:		DATE DE FIN

D&F ENGINEERING
Confort at home
Tel (+221) 76-141-32-23
Tel (+221) 77-234-03-20
Email: dnfengineeringsav@gmail.com





MAITRE D'OUVRAGE:

MOHAMED BADIANE

PROJET:

PROJET DE CONSTRUCTION D UNE VILLA RESIDENTIELLE SIS A MBAO

TITRE: 3D FACADE

ECH:	DWG No: 003	CAD: APS
DWR:	DATE DE FIN	

D&F ENGINEERING
Confort at home
Tel (+221) 76-141-32-23
Tel (+221) 77-234-03-20
Email: dnfengineeringsav@gmail.com





MAITRE D'OUVRAGE: MOHAMED BADIANE	PROJET: PROJET DE CONSTRUCTION D UNE VILLA RESIDENTIELLE SIS A MBAO	TITRE: SEJOUR RDC	D&F ENGINEERING Confort at home Tel (+221) 76-141-32-23 Tel (+221) 77-234-03-20 Email: dnfengineeringsav@gmail.com
		ECH: / DWG No: 004 / CAD: APS	
		DWR: / DATE DE FIN	





MAITRE D'OUVRAGE:

MOHAMED BADIANE

PROJET:

PROJET DE CONSTRUCTION D UNE VILLA RESIDENTIELLE SIS A MBAO

TITRE: SEJOUR RDC

ECH:	DWG No: 005	CAD: APS
DWR:	DATE DE FIN	

D&F ENGINEERING
Confort at home
Tel (+221) 76-141-32-23
Tel (+221) 77-234-03-20
Email: dnfengineeringsav@gmail.com





MAITRE D'OUVRAGE:

MOHAMED BADIANE

PROJET:

PROJET DE CONSTRUCTION D UNE VILLA RESIDENTIELLE SIS A MBAO

TITRE: ESCALIER - JARDIN

ECH:	DWG No: 006	CAD: APS
DWR:	DATE DE FIN	

D&F ENGINEERING
Confort at home
Tel (+221) 76-141-32-23
Tel (+221) 77-234-03-20
Email: dnfengineeringsav@gmail.com





MAITRE D'OUVRAGE:

MOHAMED BADIANE

PROJET:

PROJET DE CONSTRUCTION D UNE VILLA RESIDENTIELLE SIS A MBAO

TITRE: CHAMBRE - TOIL - RDC

ECH:	DWG No: 007	CAD: APS
DWR:	DATE DE FIN	

D&F ENGINEERING
Confort at home
Tel (+221) 76-141-32-23
Tel (+221) 77-234-03-20
Email: dnfengineeringsav@gmail.com





MAITRE D'OUVRAGE:

MOHAMED BADIANE

PROJET:

PROJET DE CONSTRUCTION D UNE VILLA RESIDENTIELLE SIS A MBAO

TITRE: CHAMBRE ETAGE

ECH:	DWG No: 008	CAD: APS
DWR:	DATE DE FIN	

D&F ENGINEERING
Confort at home
Tel (+221) 76-141-32-23
Tel (+221) 77-234-03-20
Email: dnfengineeringsav@gmail.com





MAITRE D'OUVRAGE:

MOHAMED BADIANE

PROJET:

PROJET DE CONSTRUCTION D UNE VILLA RESIDENTIELLE SIS A MBAO

TITRE: CUISINE - SEJOUR - ETAGE

ECH:	DWG No: 009	CAD: APS
DWR:	DATE DE FIN	

D&F ENGINEERING
Confort at home
Tel (+221) 76-141-32-23
Tel (+221) 77-234-03-20
Email: dnfengineeringsav@gmail.com



MAITRE D'OUVRAGE:

MOHAMED BADIANE


PROJET:

PROJET DE CONSTRUCTION D UNE VILLA RESIDENTIELLE SIS A MBAO


TITRE: FACADE 2D

ECH:	DWG No: 010	CAD: APS
DWR:	DATE DE FIN	


D&F ENGINEERING
Confort at home
Tel (+221) 76-141-32-23
Tel (+221) 77-234-03-20
Email: dnfengineeringsav@gmail.com

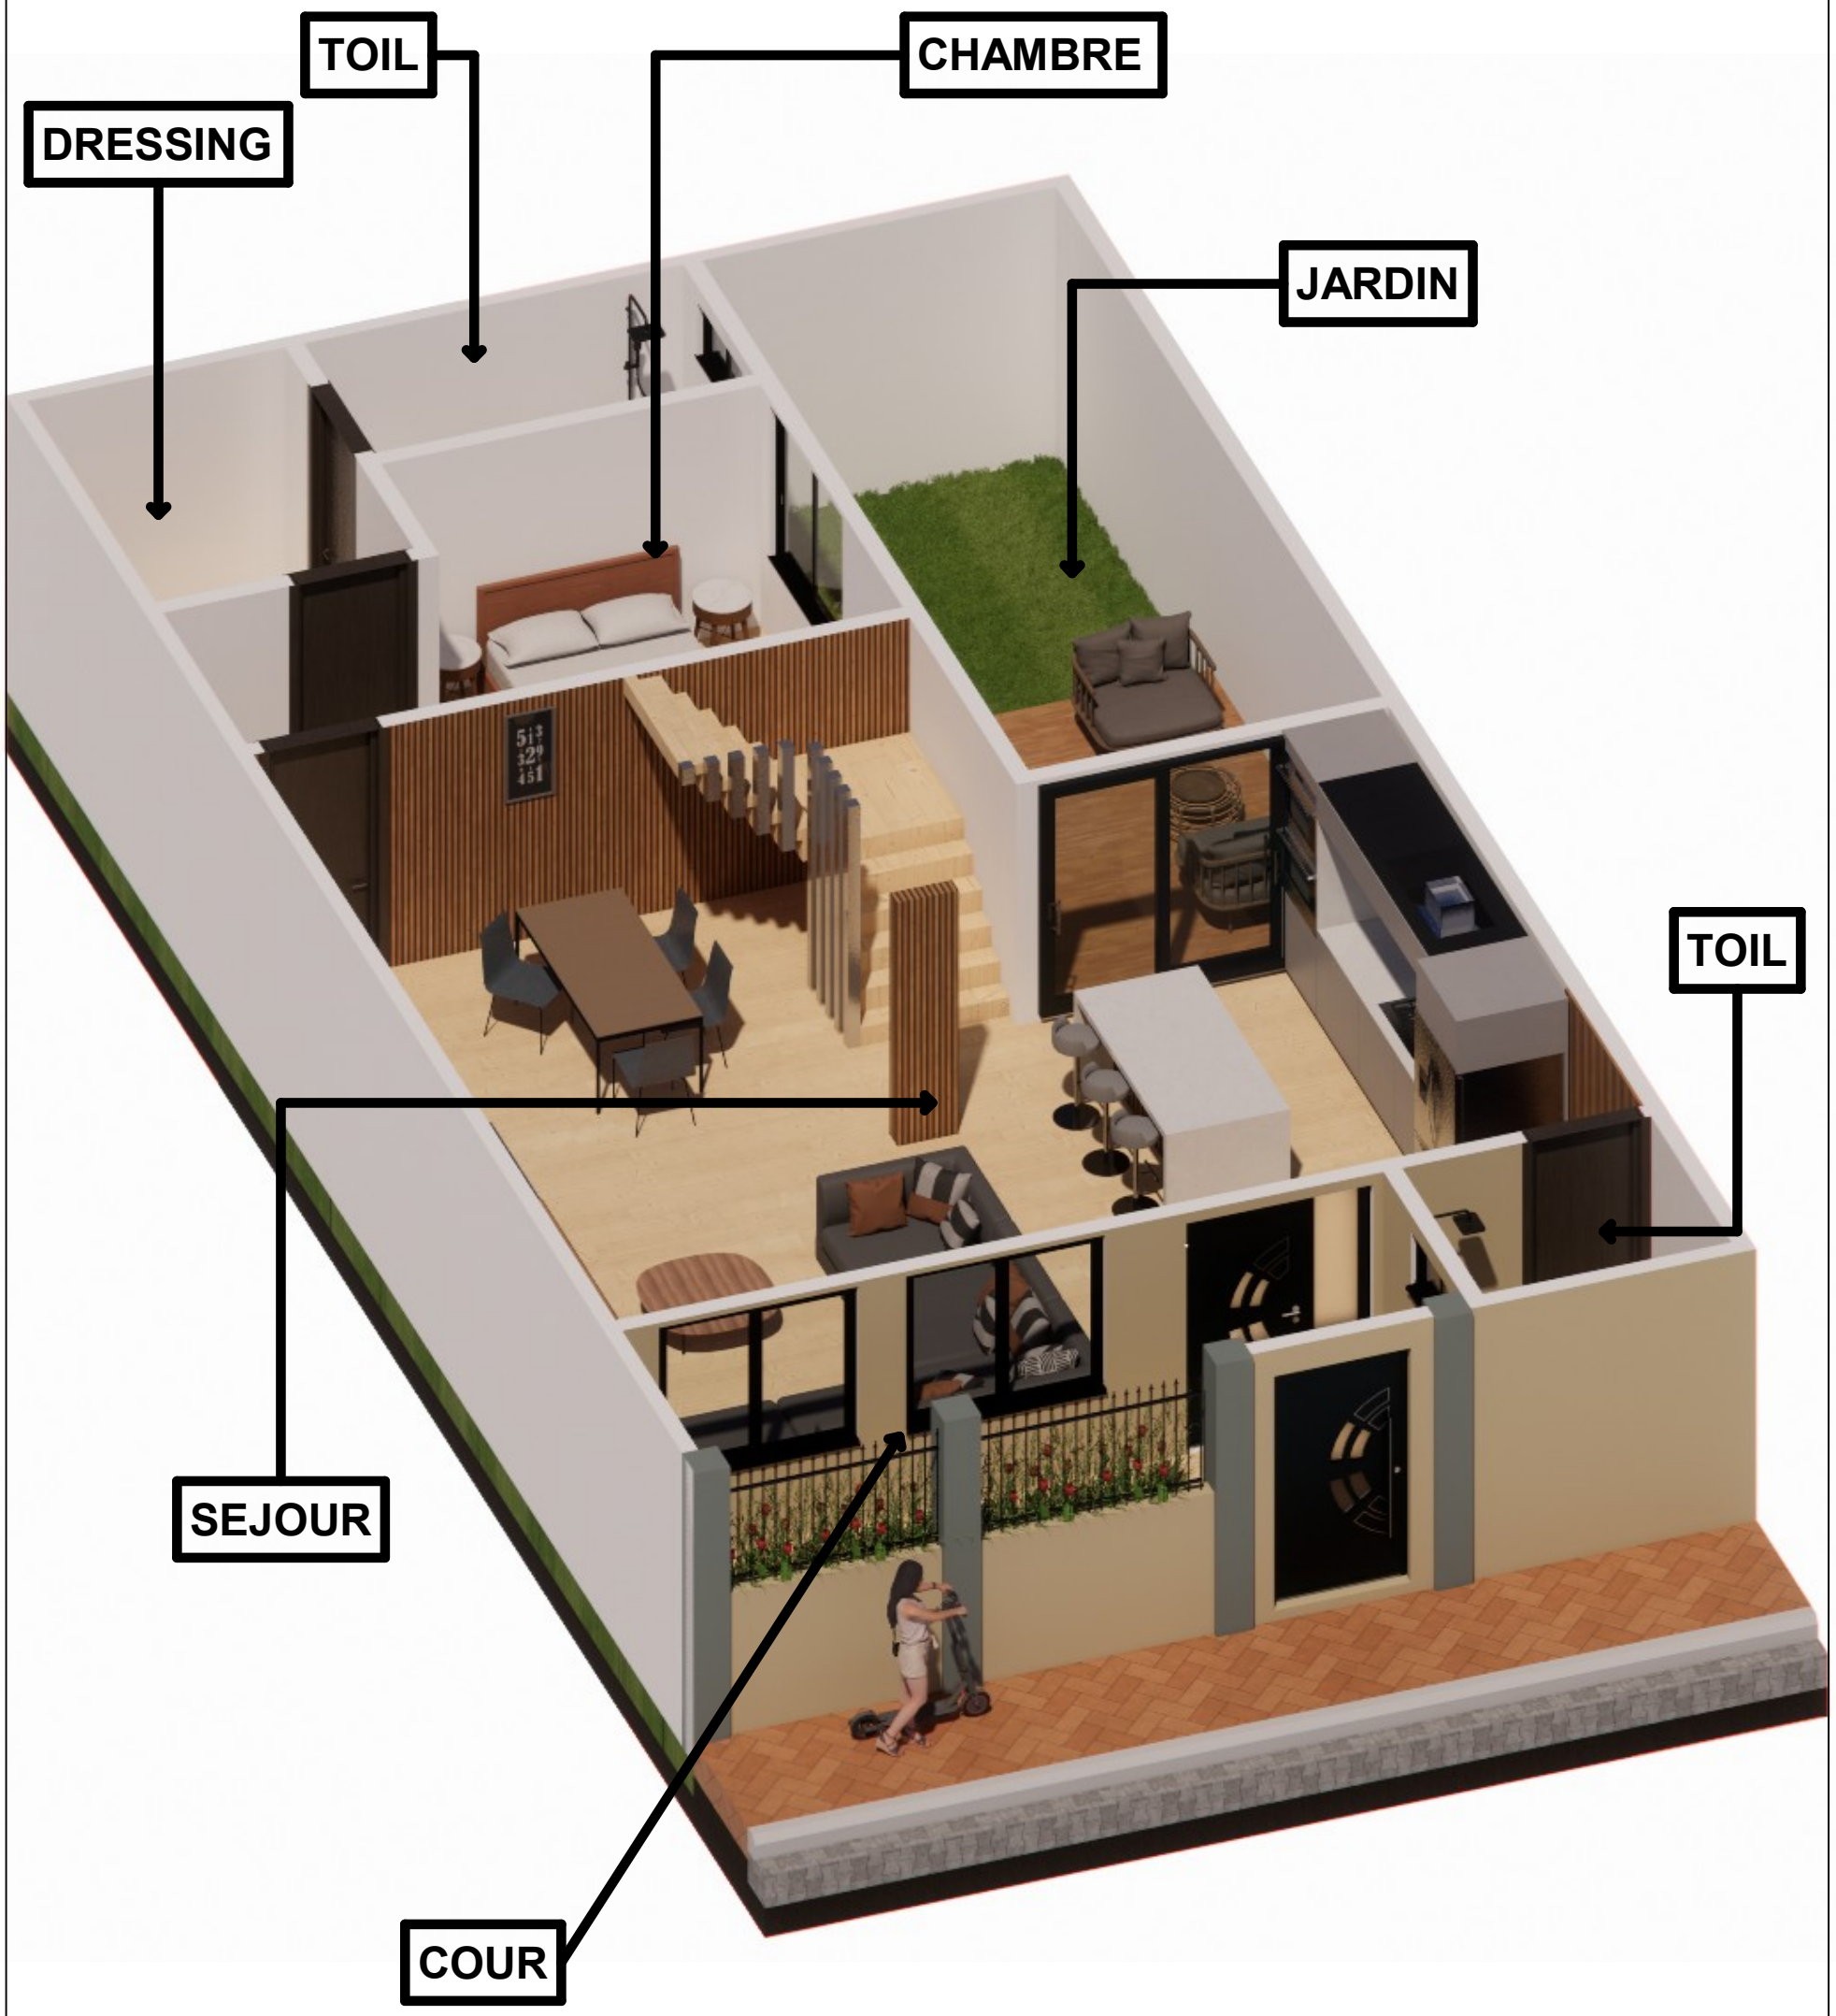


MAITRE D'OUVRAGE: MOHAMED BADIANE	PROJET: PROJET DE CONSTRUCTION D UNE VILLA RESIDENTIELLE SIS A MBAO	TITRE: RDC MODEL	D&F ENGINEERING Confort at home Tel (+221) 76-141-32-23 Tel (+221) 77-234-03-20 Email: dnfengineeringsav@gmail.com
		ECH: / DWG No: 011 / CAD: APS	
		DWR: / DATE DE FIN	

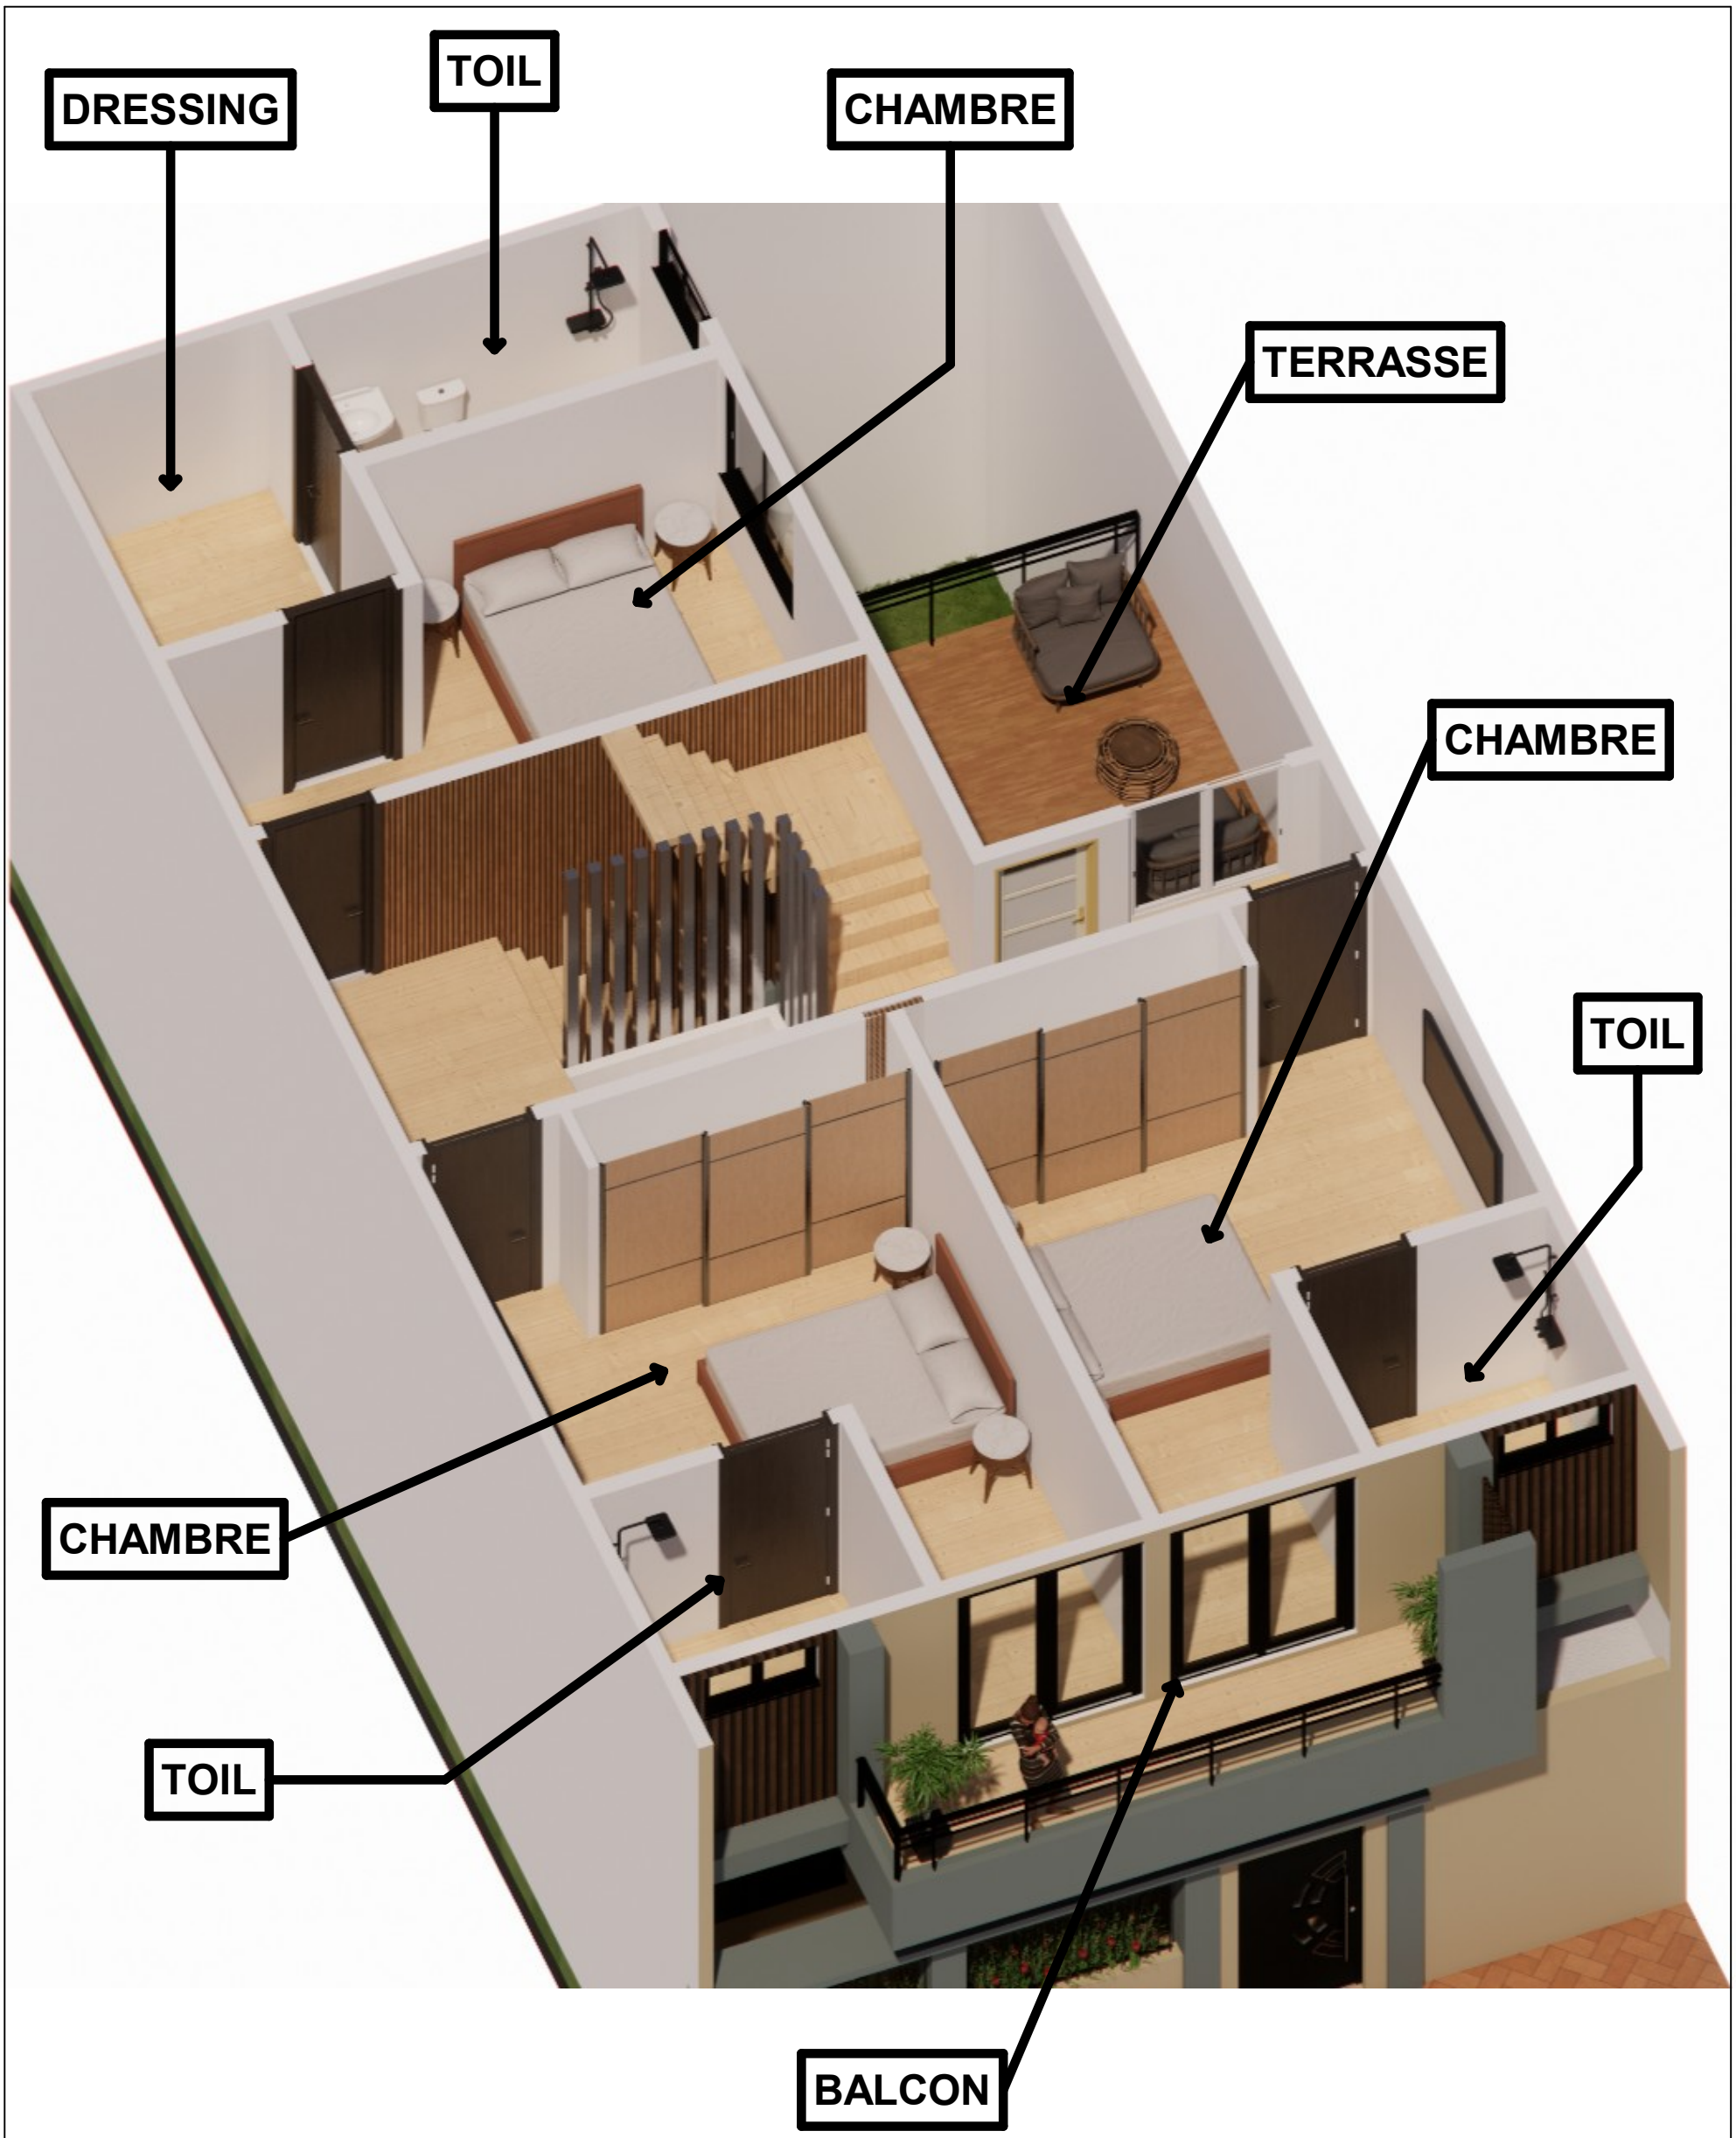


MAITRE D'OUVRAGE: MOHAMED BADIANE	PROJET: PROJET DE CONSTRUCTION D UNE VILLA RESIDENTIELLE SIS A MBAO	TITRE: ETAGE 01 MODEL	D&F ENGINEERING Confort at home
		ECH: / DWG No: 012 / CAD: APS	Tel (+221) 76-141-32-23
		DWR: / DATE DE FIN	Tel (+221) 77-234-03-20
			Email: dnfengineeringsav@gmail.com

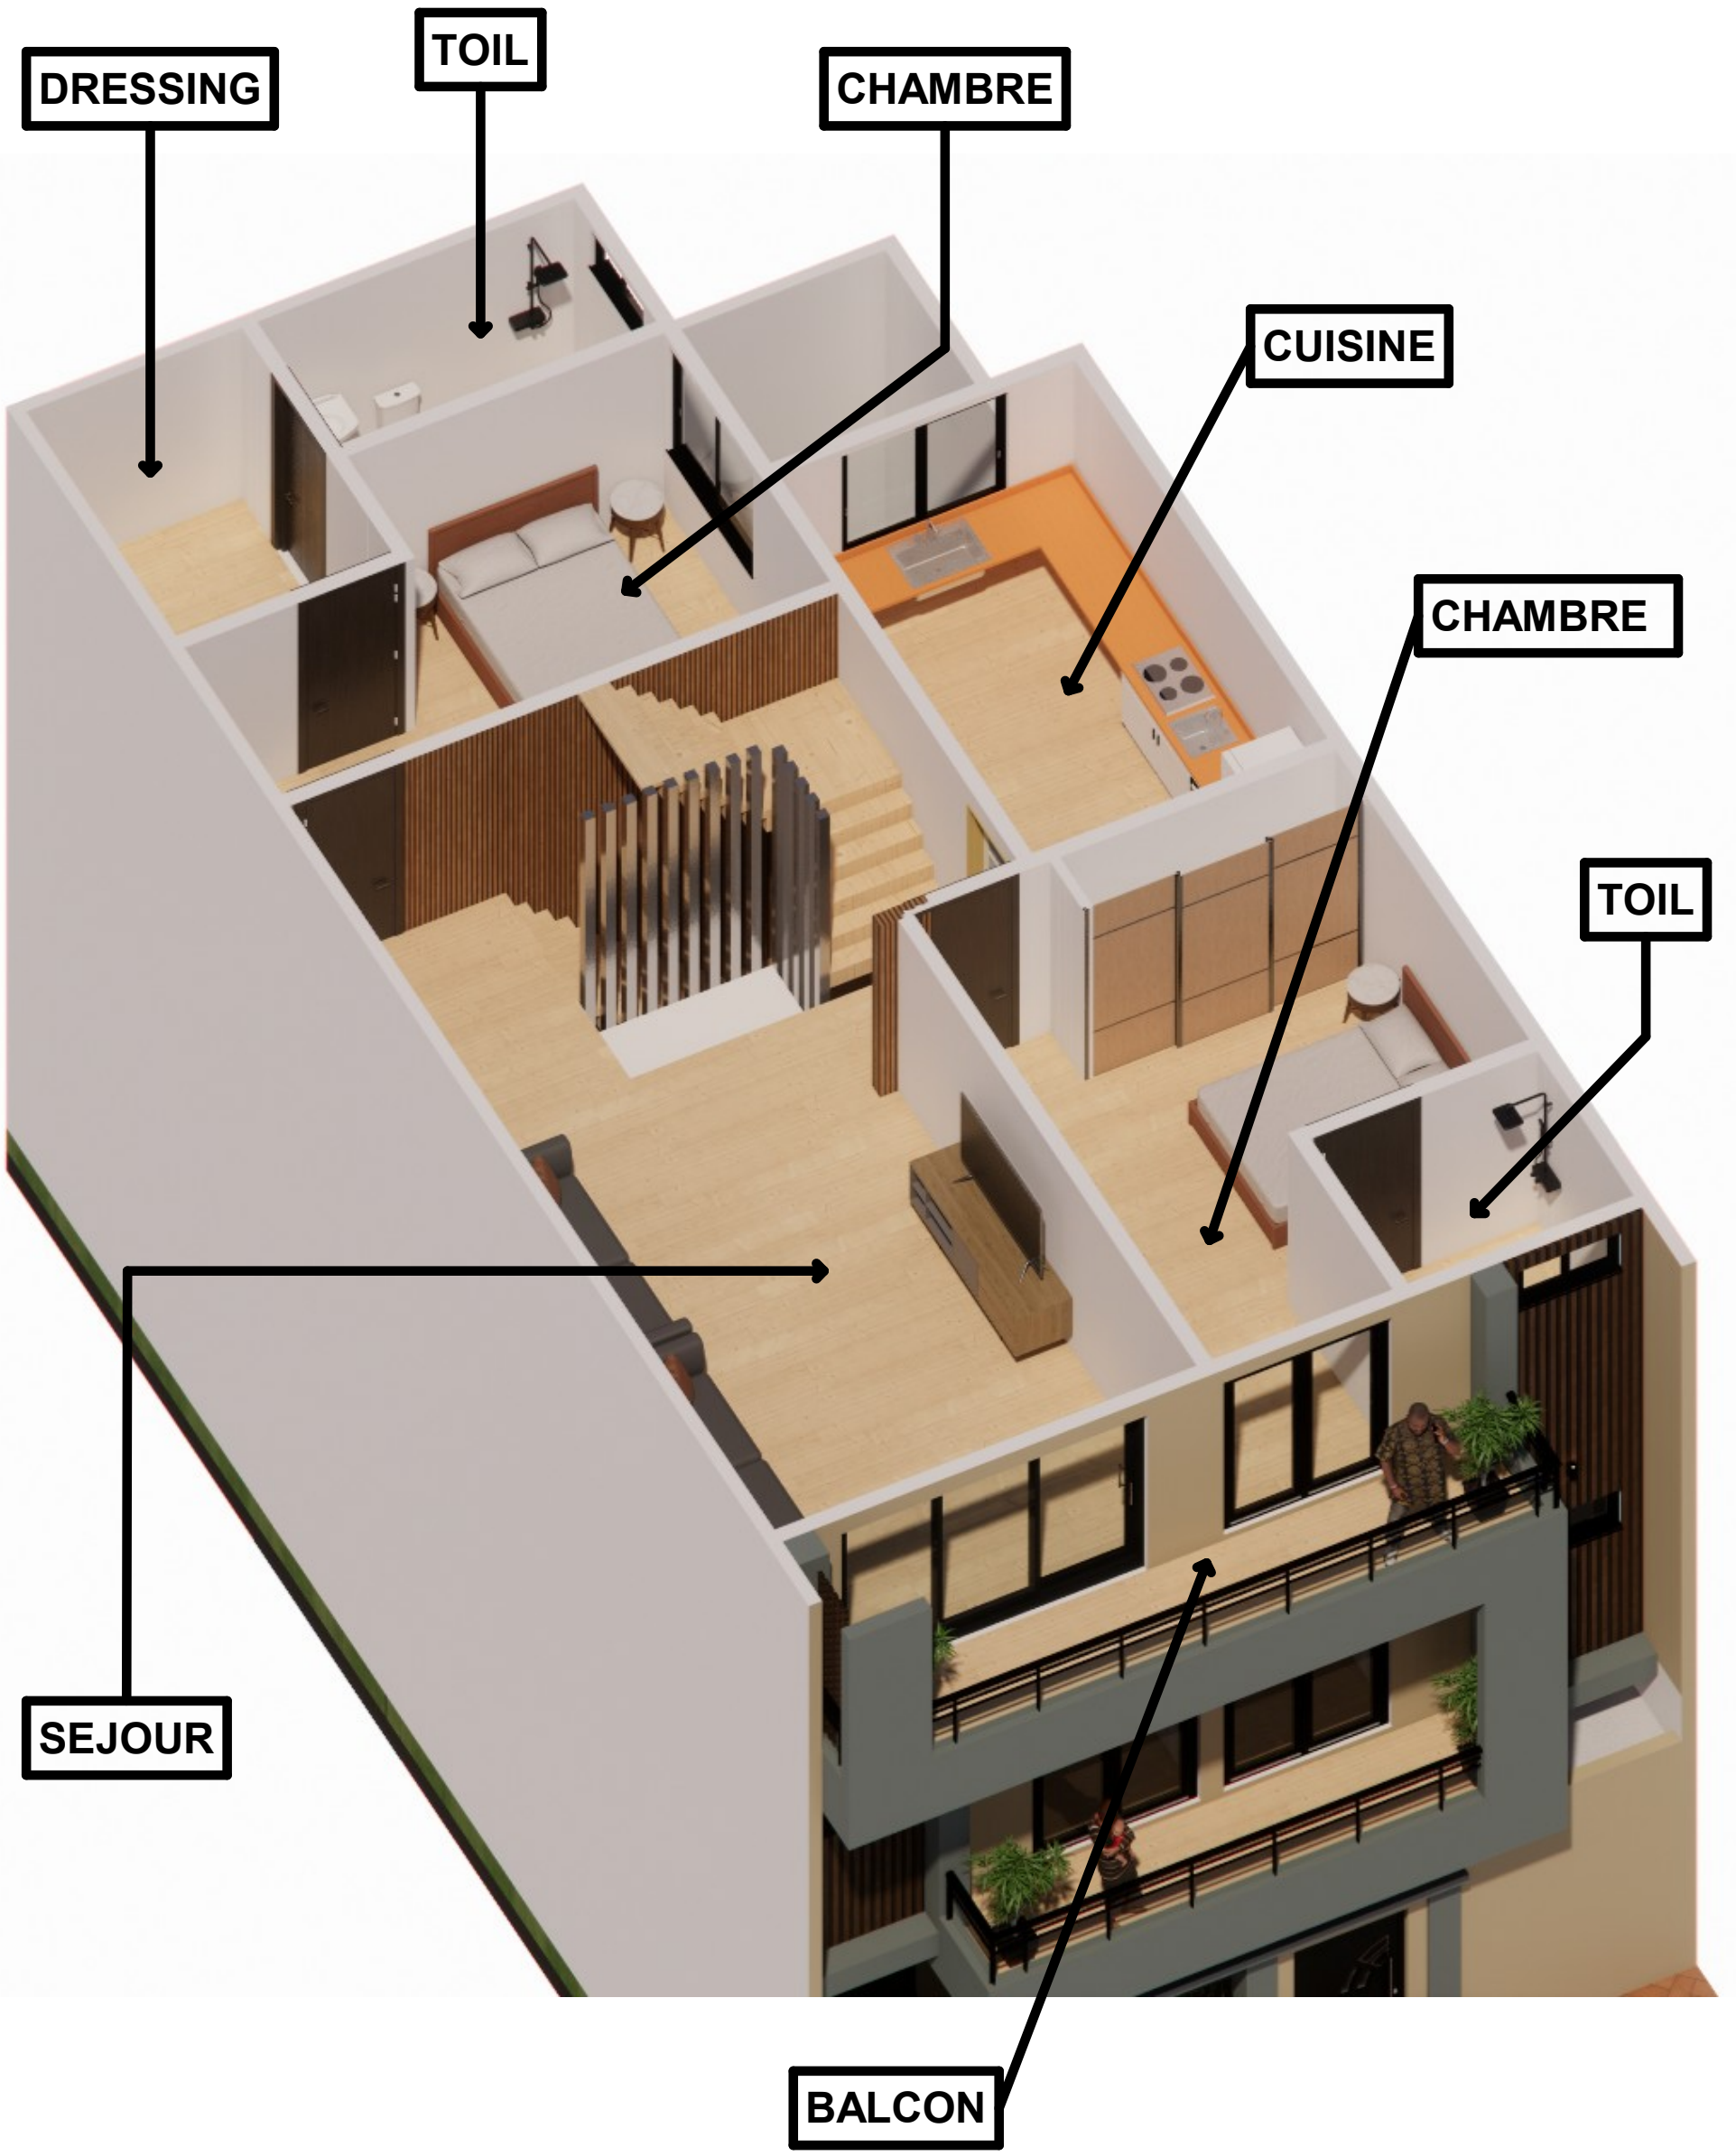

MAITRE D'OUVRAGE: MOHAMED BADIANE	PROJET: PROJET DE CONSTRUCTION D UNE VILLA RESIDENTIELLE SIS A MBAO	TITRE: ETAGE 02 MODEL ECH: / DWG No: 013 / CAD: APS DWR: / DATE DE FIN	D&F ENGINEERING Confort at home Tel (+221) 76-141-32-23 Tel (+221) 77-234-03-20 Email: dnfengineeringsav@gmail.com

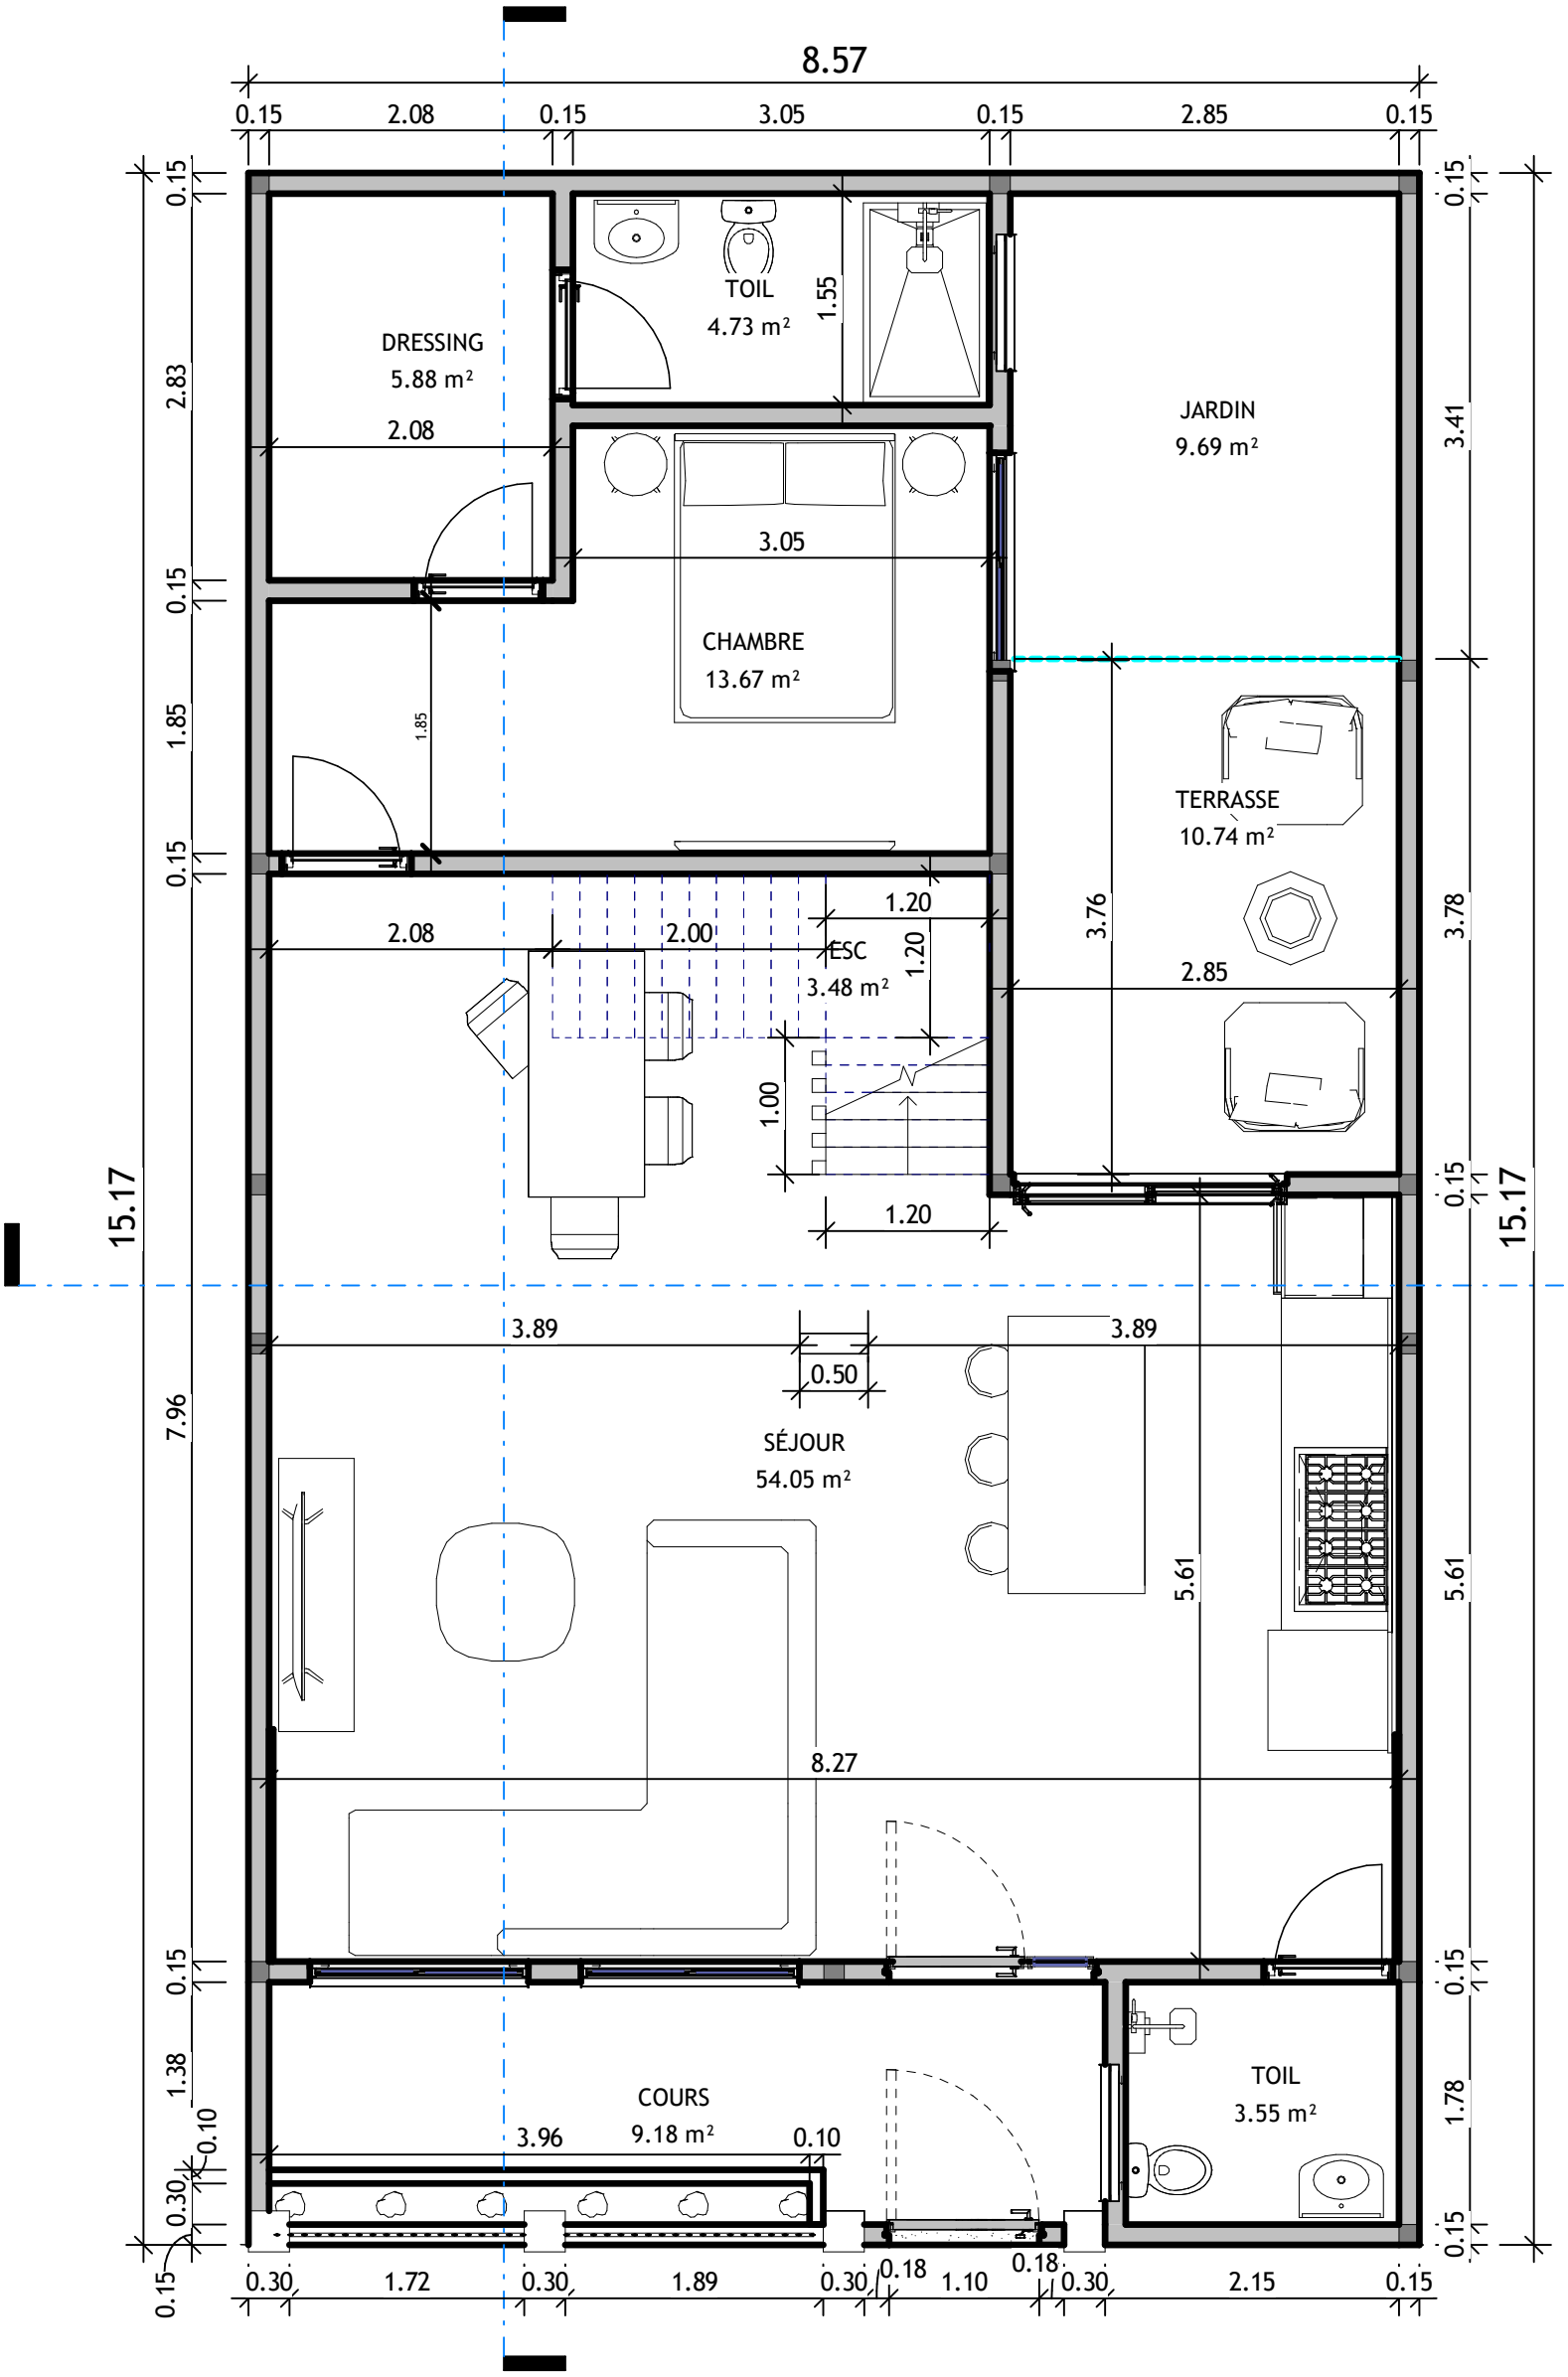

MAITRE D'OUVRAGE: MOHAMED BADIANE	PROJET: PROJET DE CONSTRUCTION D UNE VILLA RESIDENTIELLE SIS A MBAO	TITRE: RDC COTÉ	D&F ENGINEERING
		ECH: 1 : 50 / DWG No: 014 / CAD: APS	Confort at home
		DWR: / DATE DE FIN	Tel (+221) 76-141-32-23 Tel (+221) 77-234-03-20 Email: dnfengineeringsav@gmail.com

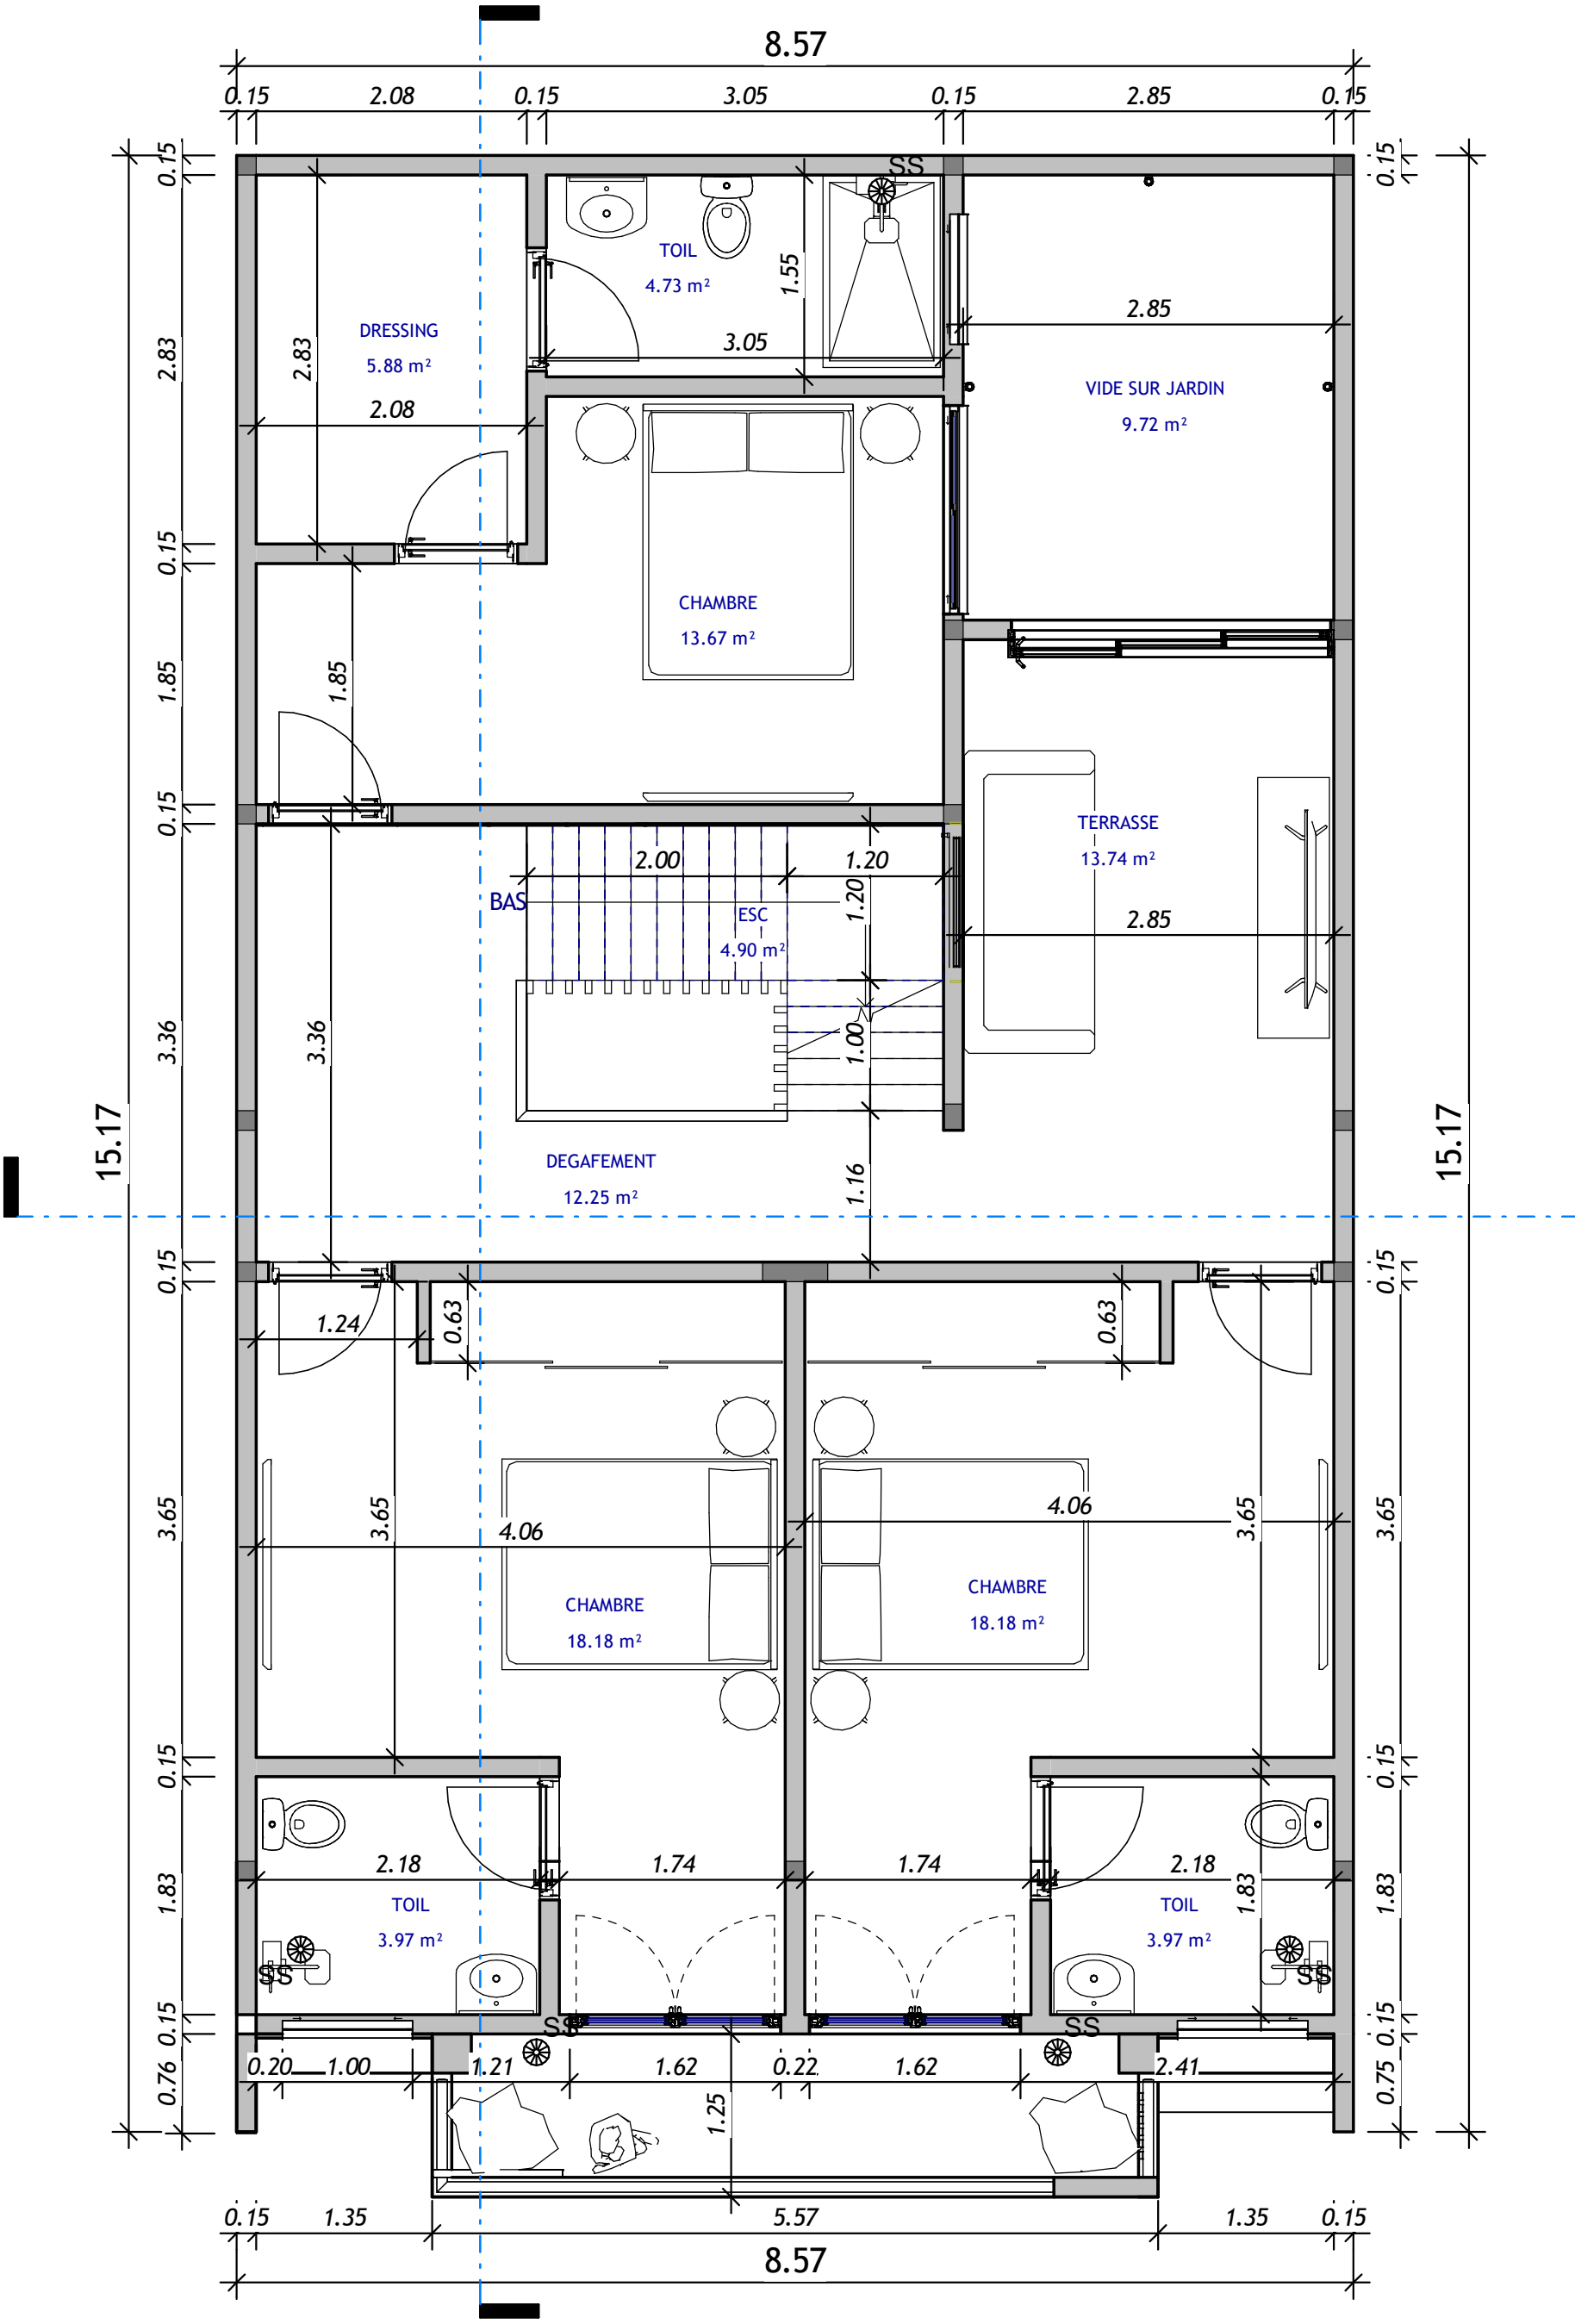

Maitre d'ouvrage:

Mohamed BADIANE


Projet:

PROJET DE CONSTRUCTION D UNE VILLA RESIDENTIELLE SIS A MBAO

Titre: R+1 COTÉ


10/09/25	DWG No: 015	Cad APS
DWR E.H.S.F	ECH: 1 : 50	

D&F ENGINEERING
Confort at home
Tel (+221) 76-141-32-23
Tel (+221) 77-234-03-20
Email: dnfengineeringsav@gmail.com

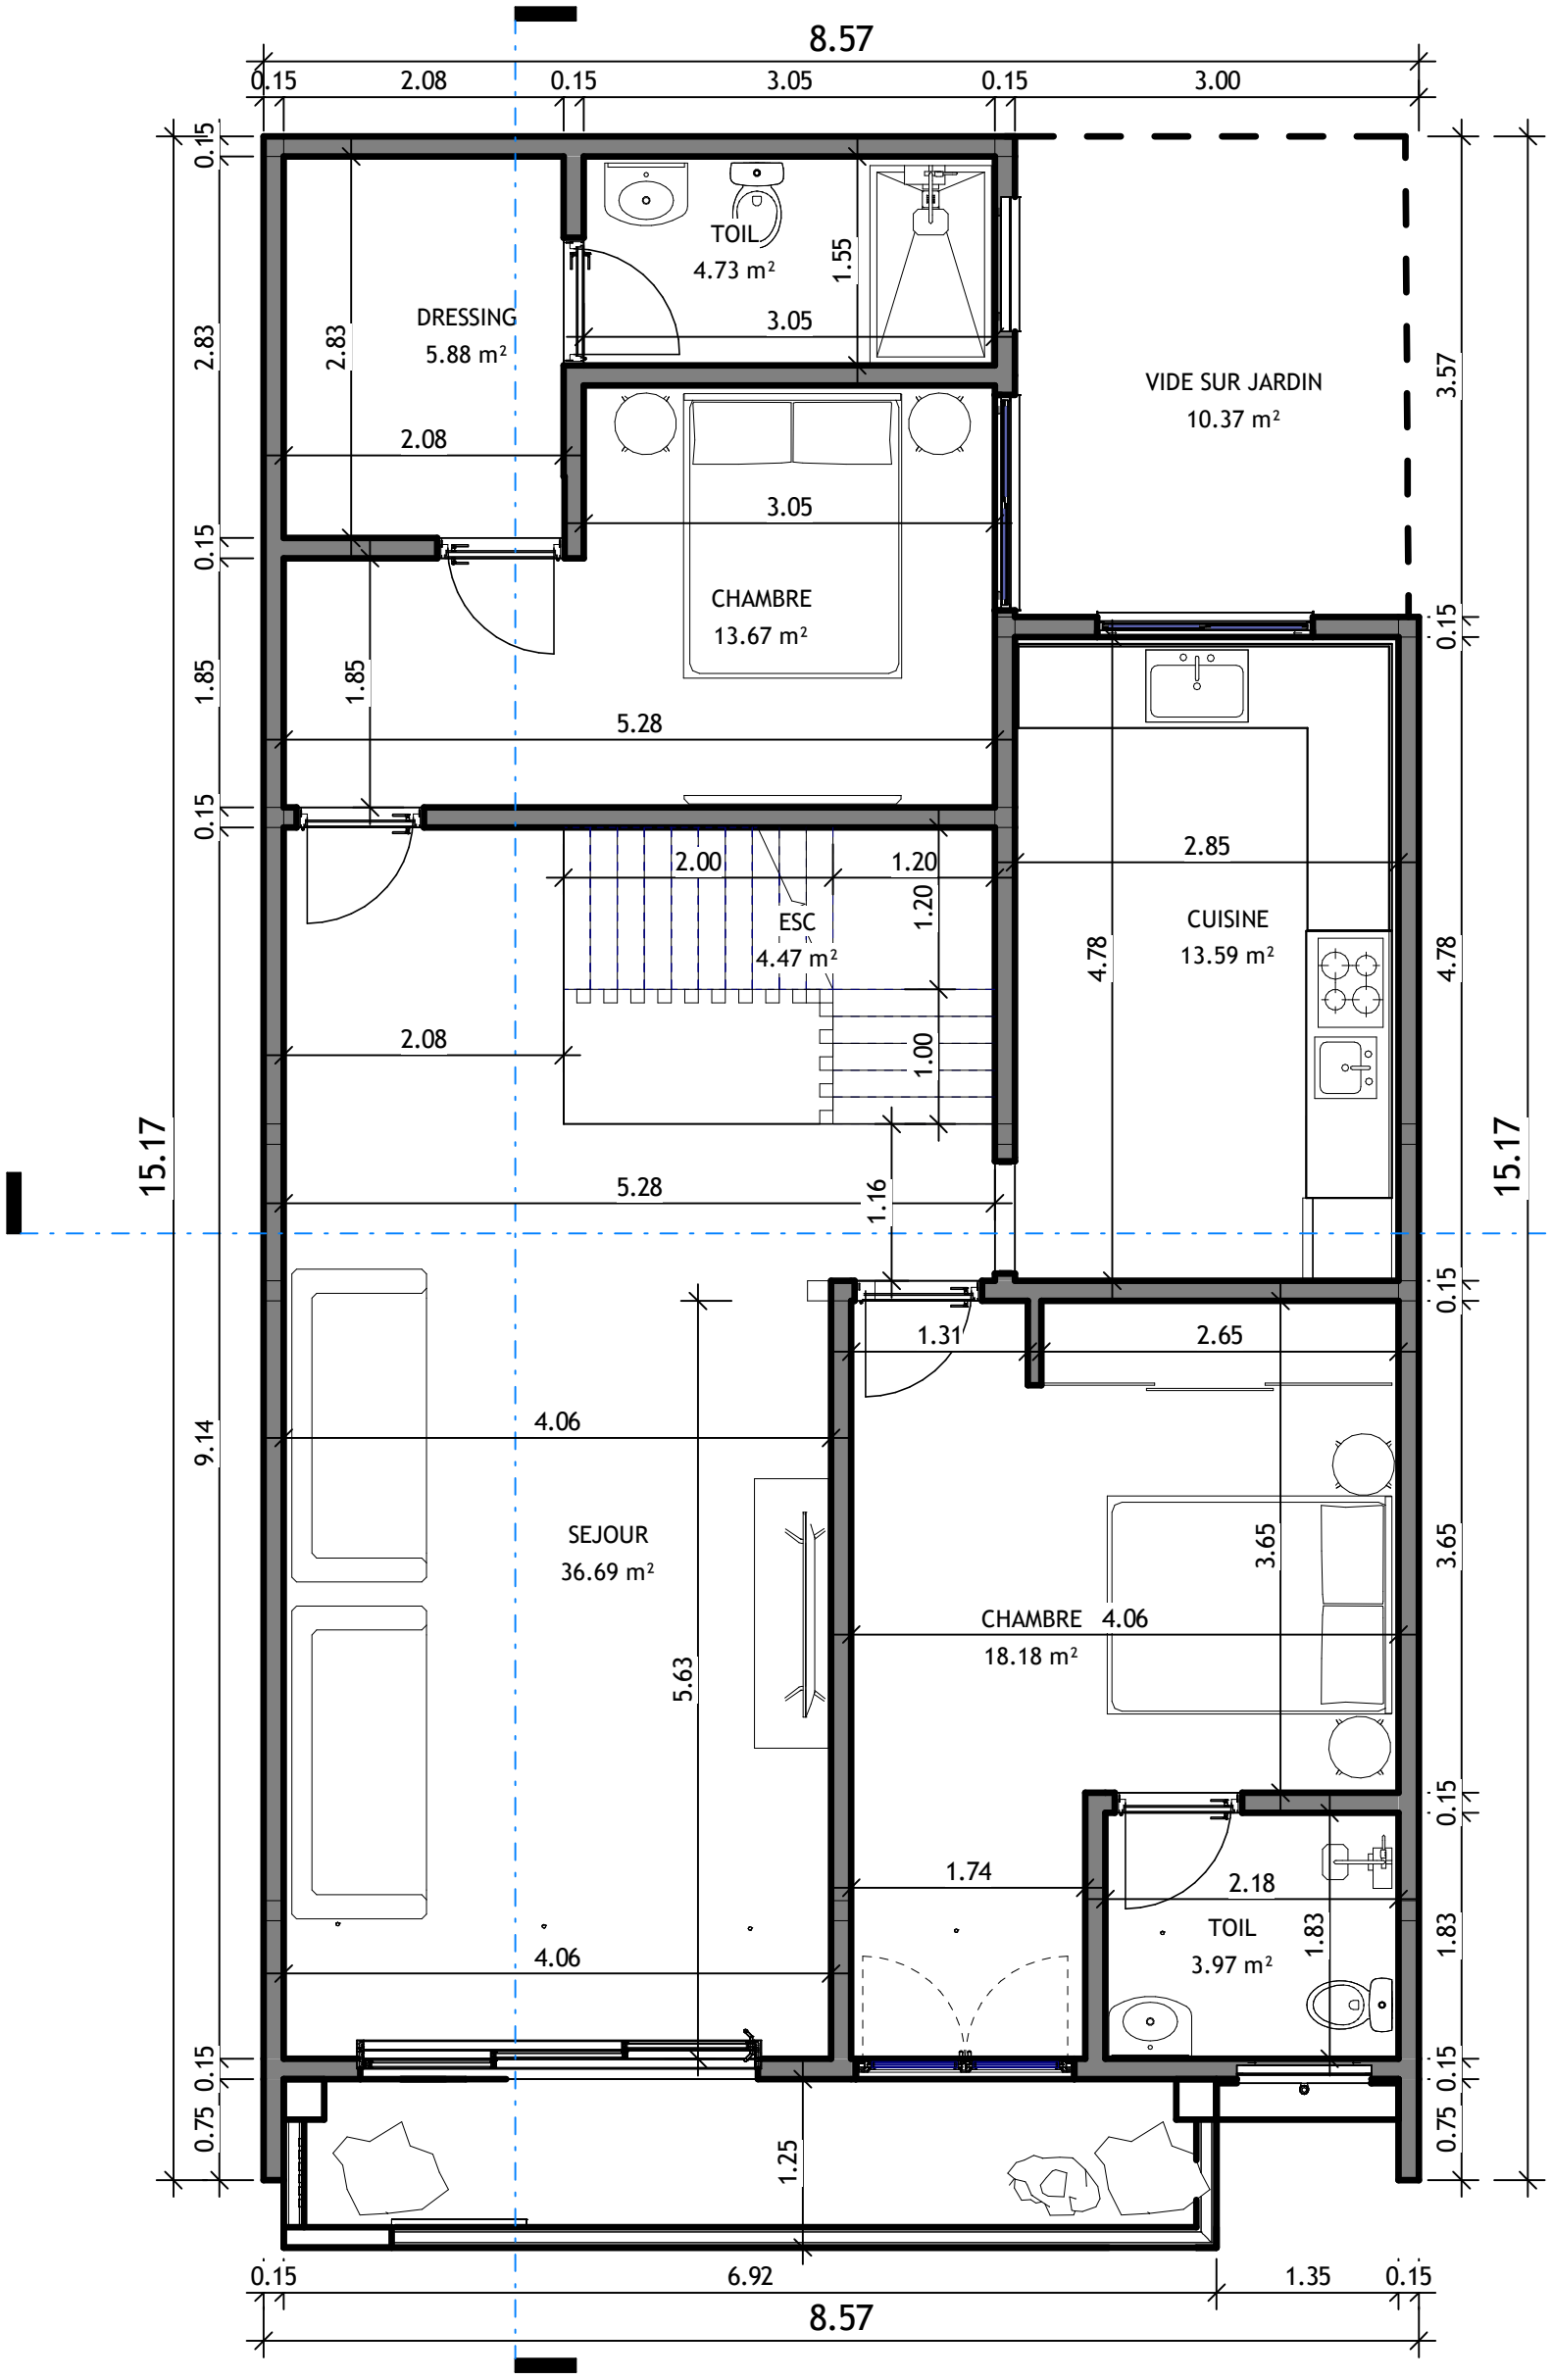


MAITRE D'OUVRAGE: MOHAMED BADIANE	PROJET: PROJET DE CONSTRUCTION D UNE VILLA RESIDENTIELLE SIS A MBAO	TITRE: R+2 COTÉ	
		ECH: 1 : 50	DWG No: 016
		CAD: APS	
		DWR:	DATE DE FIN

D&F ENGINEERING
Confort at home
Tel (+221) 76-141-32-23
Tel (+221) 77-234-03-20
Email: dnfengineeringsav@gmail.com

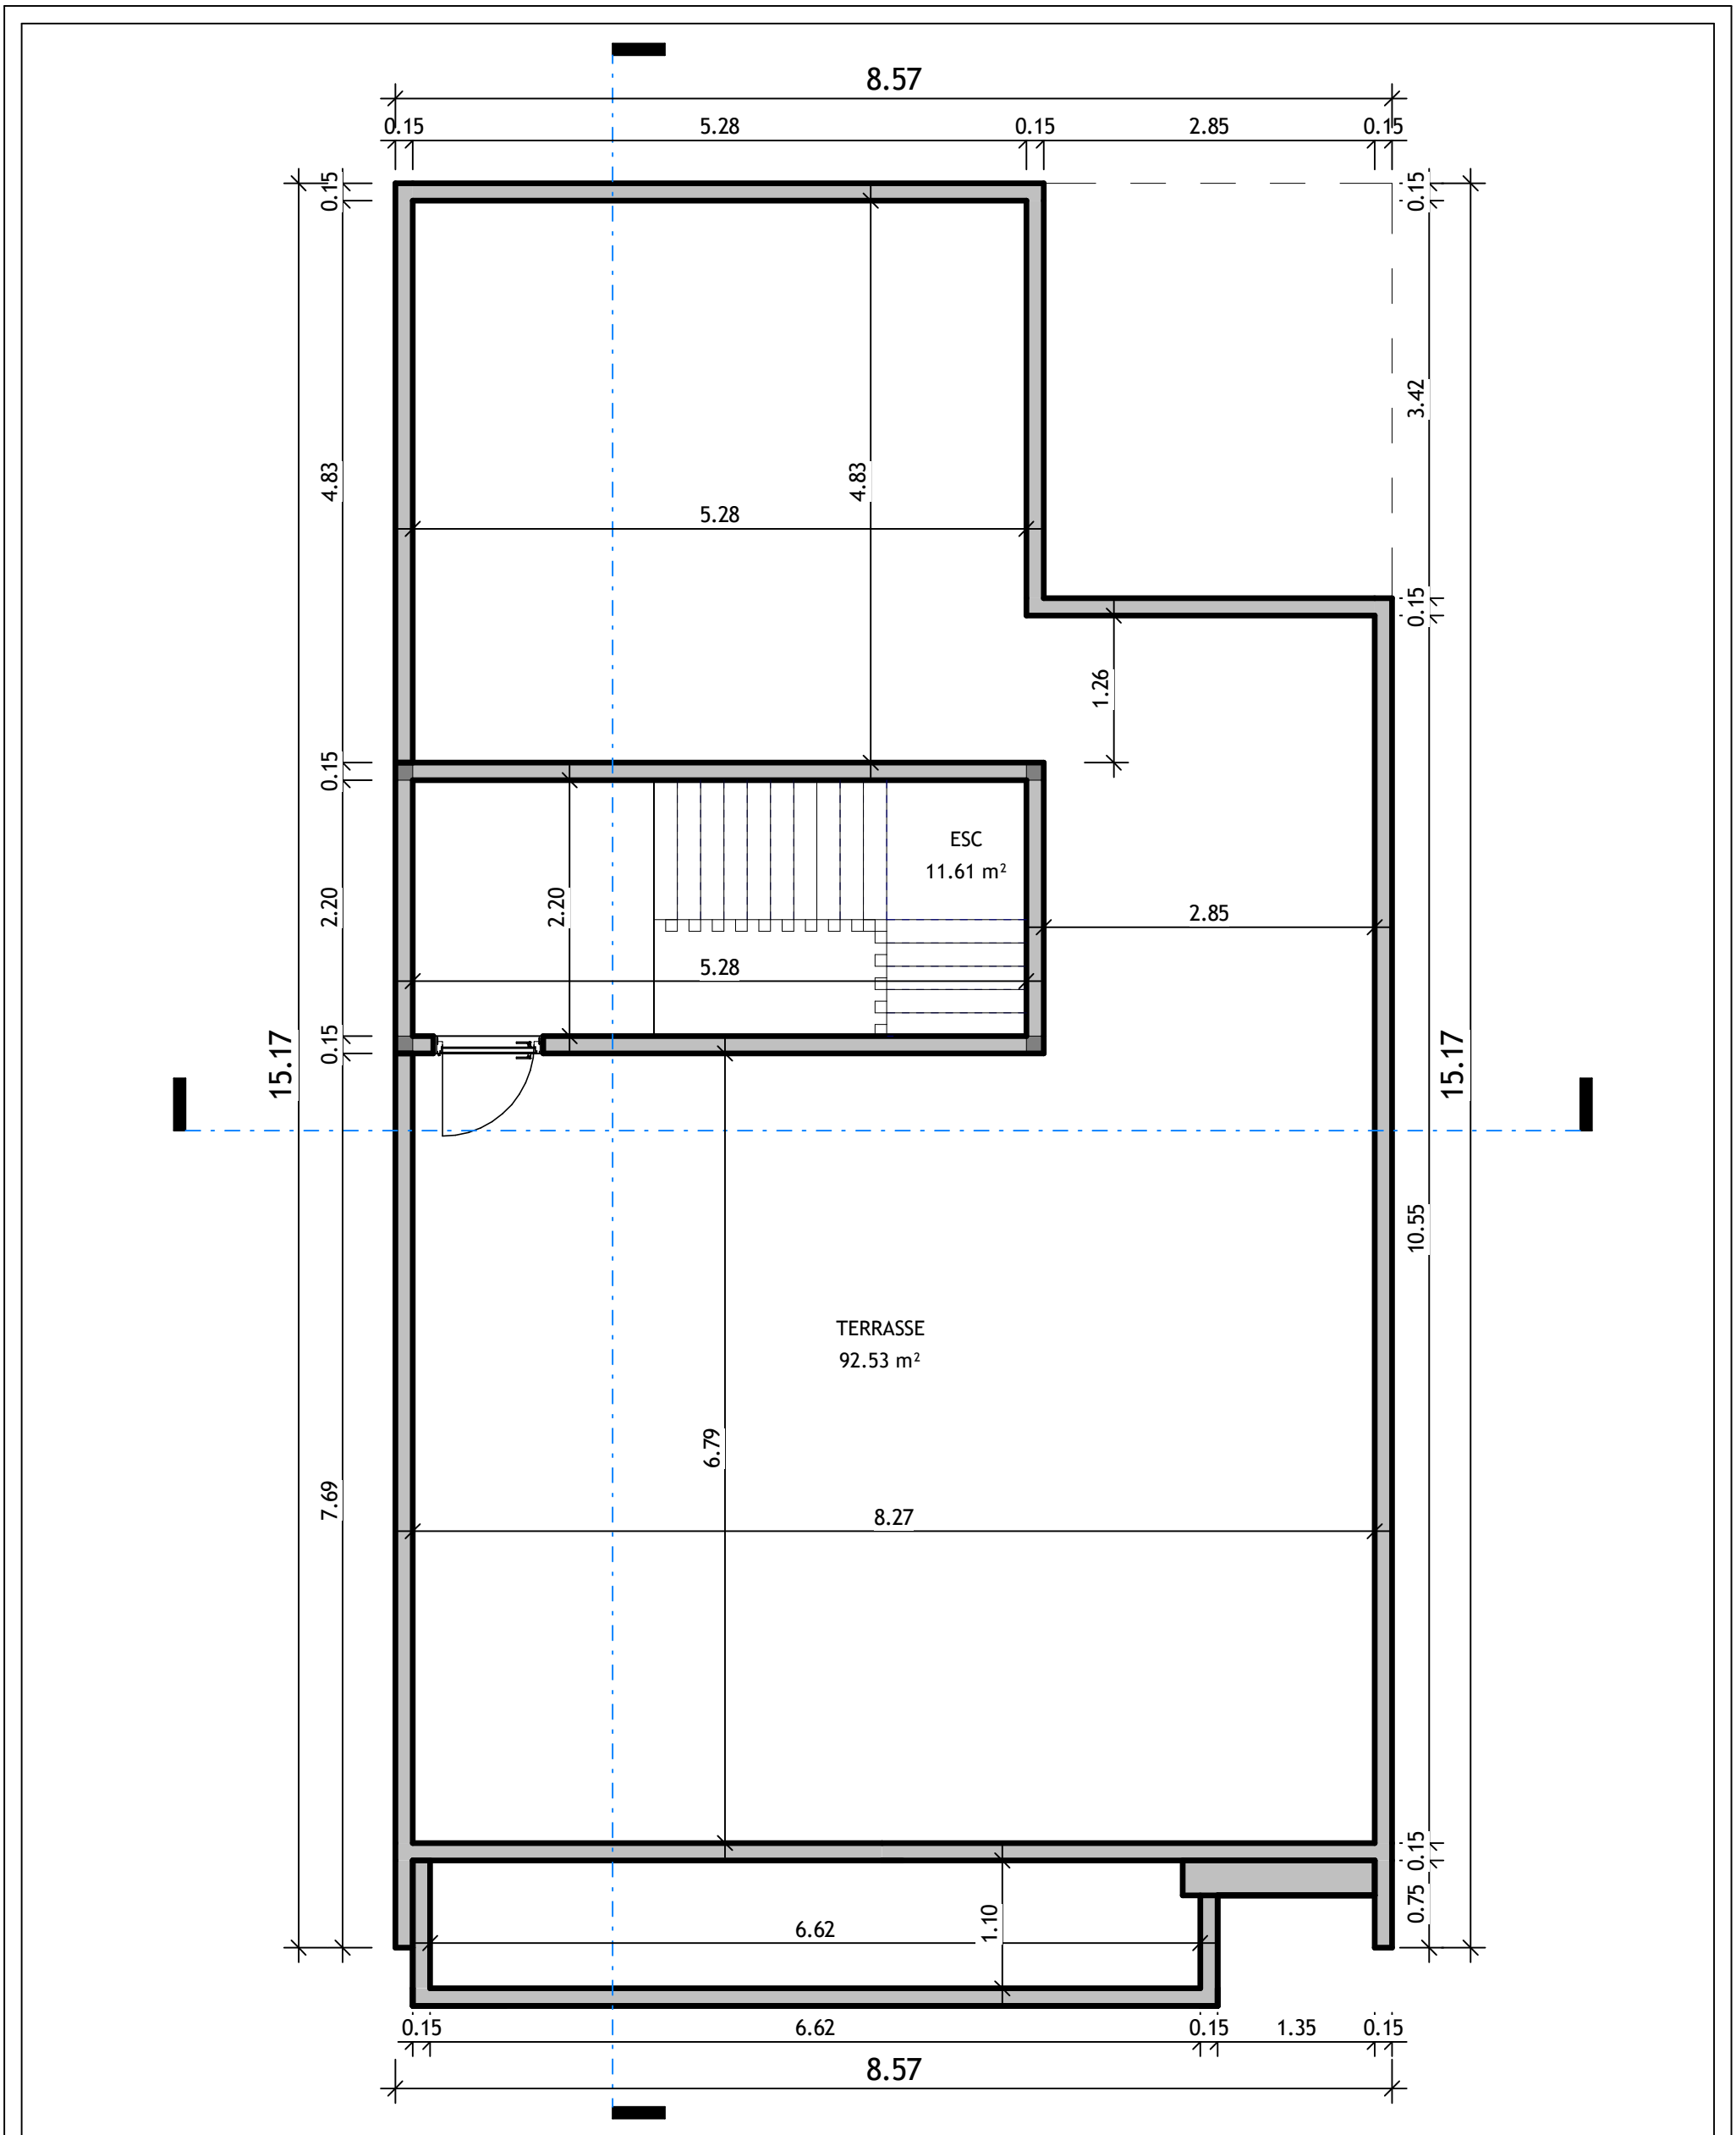

MAITRE D'OUVRAGE: MOHAMED BADIANE	PROJET: PROJET DE CONSTRUCTION D UNE VILLA RESIDENTIELLE SIS A MBAO	TITRE: TERRASSE COTÉ	D&F ENGINEERING
		ECH: 1 : 50 DWG No: 017 CAD: APS	Tel (+221) 76-141-32-23
		DWR: DATE DE FIN	Tel (+221) 77-234-03-20
			Email: dnfengineeringsav@gmail.com

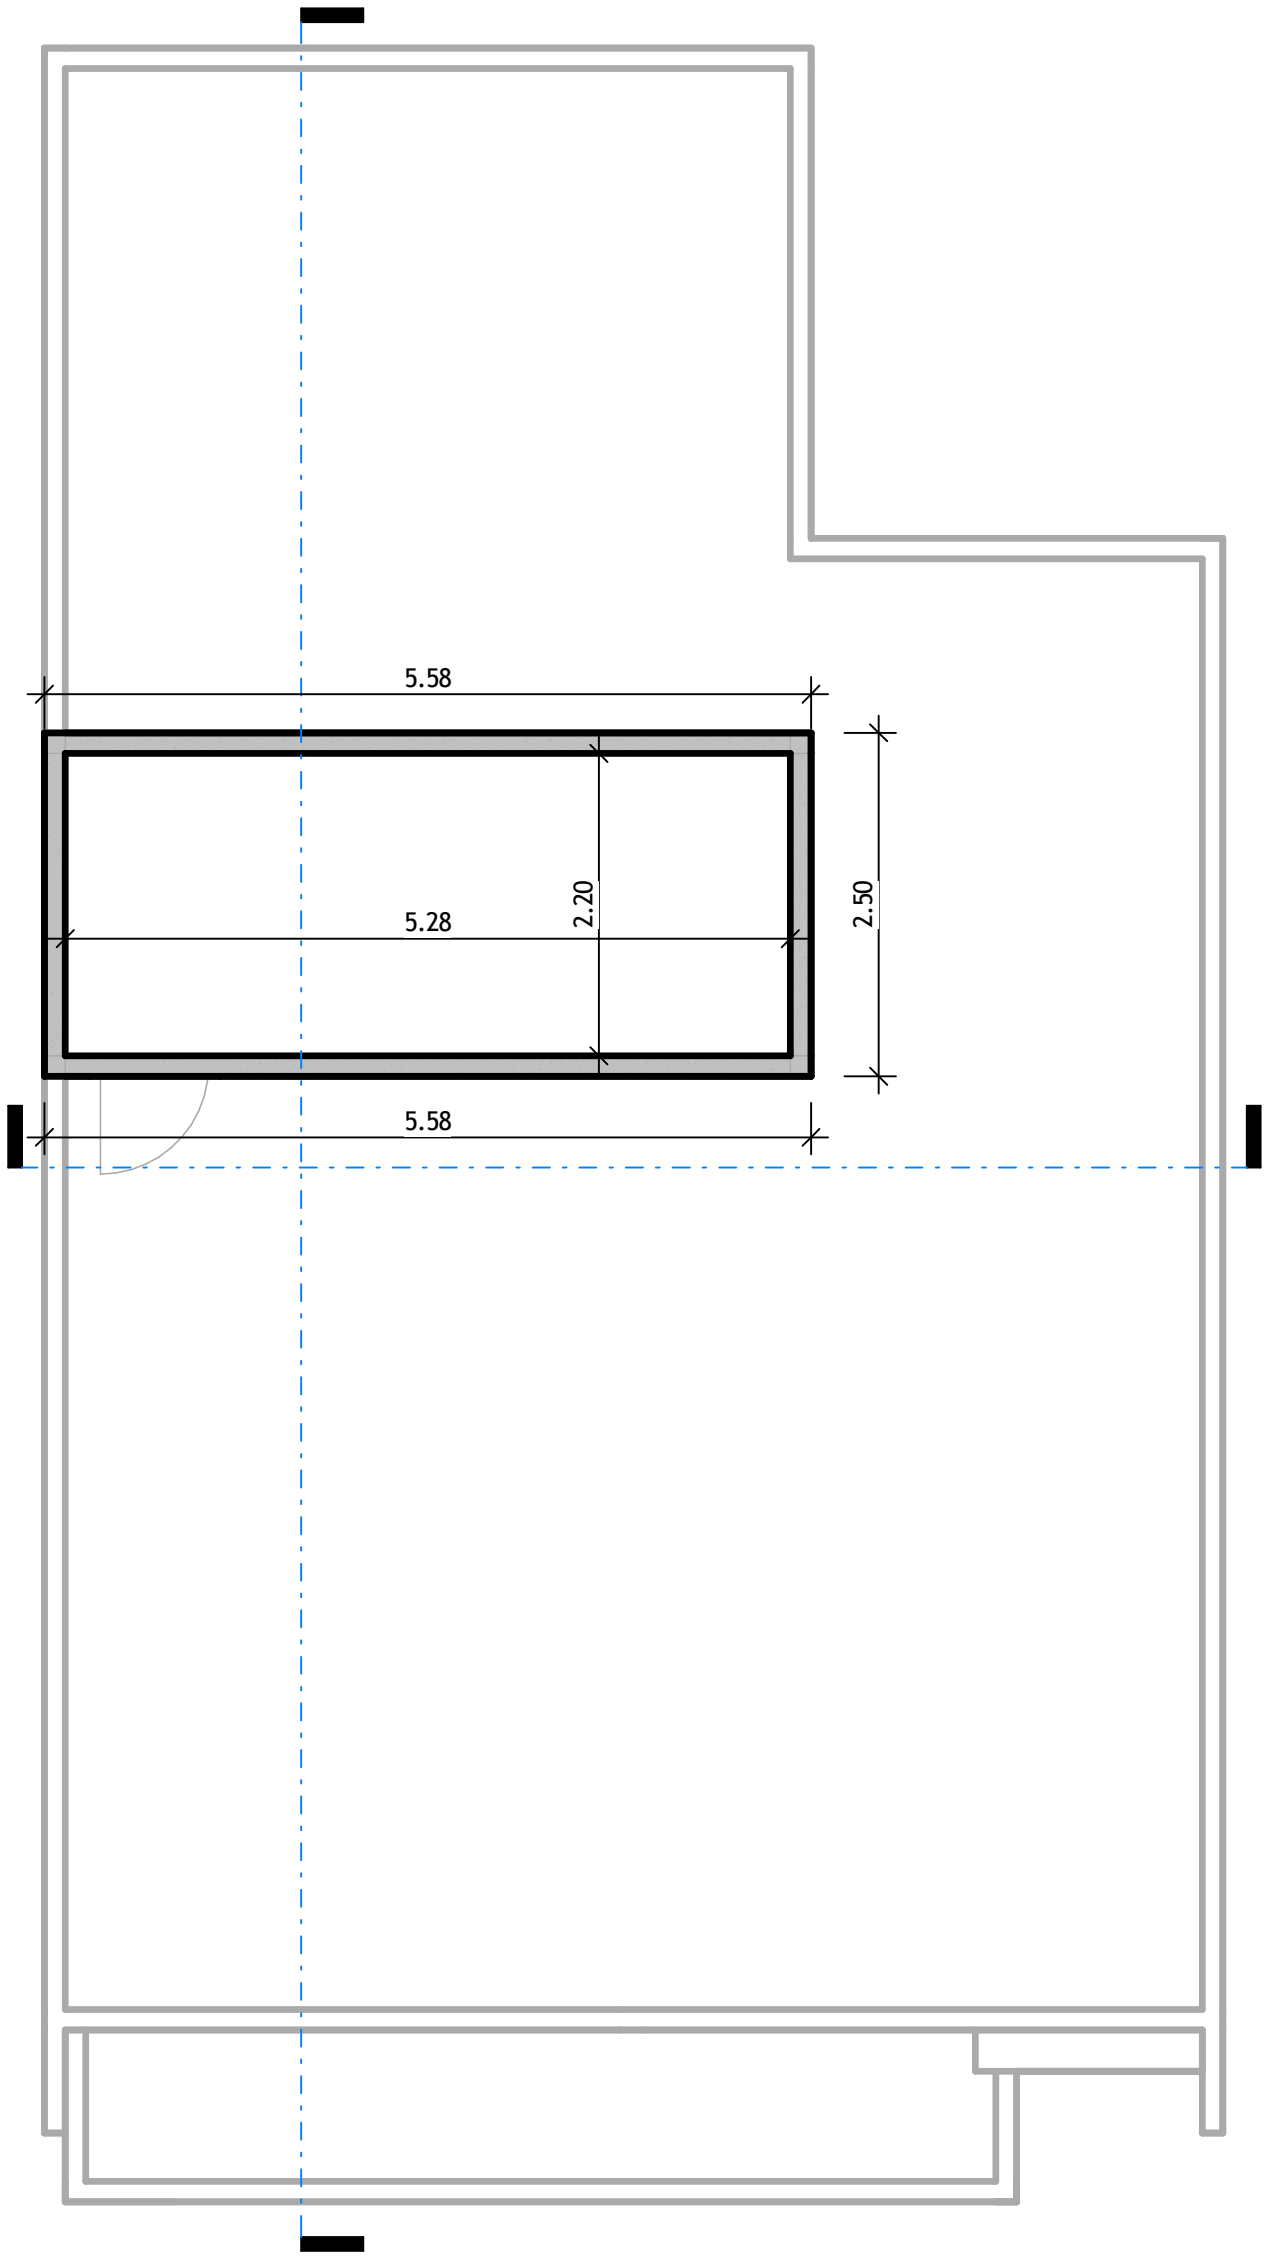

MAITRE D'OUVRAGE:

MOHAMED BADIANE

PROJET:


PROJET DE CONSTRUCTION D UNE VILLA RESIDENTIELLE SIS A MBAO

TITRE: EDICULE COTÉ

ECH: 1 : 50 | DWG No: 018 | CAD: APS

DWR: | DATE DE FIN

D&F ENGINEERING
Confort at home
Tel (+221) 76-141-32-23
Tel (+221) 77-234-03-20
Email: dnfengineeringsav@gmail.com

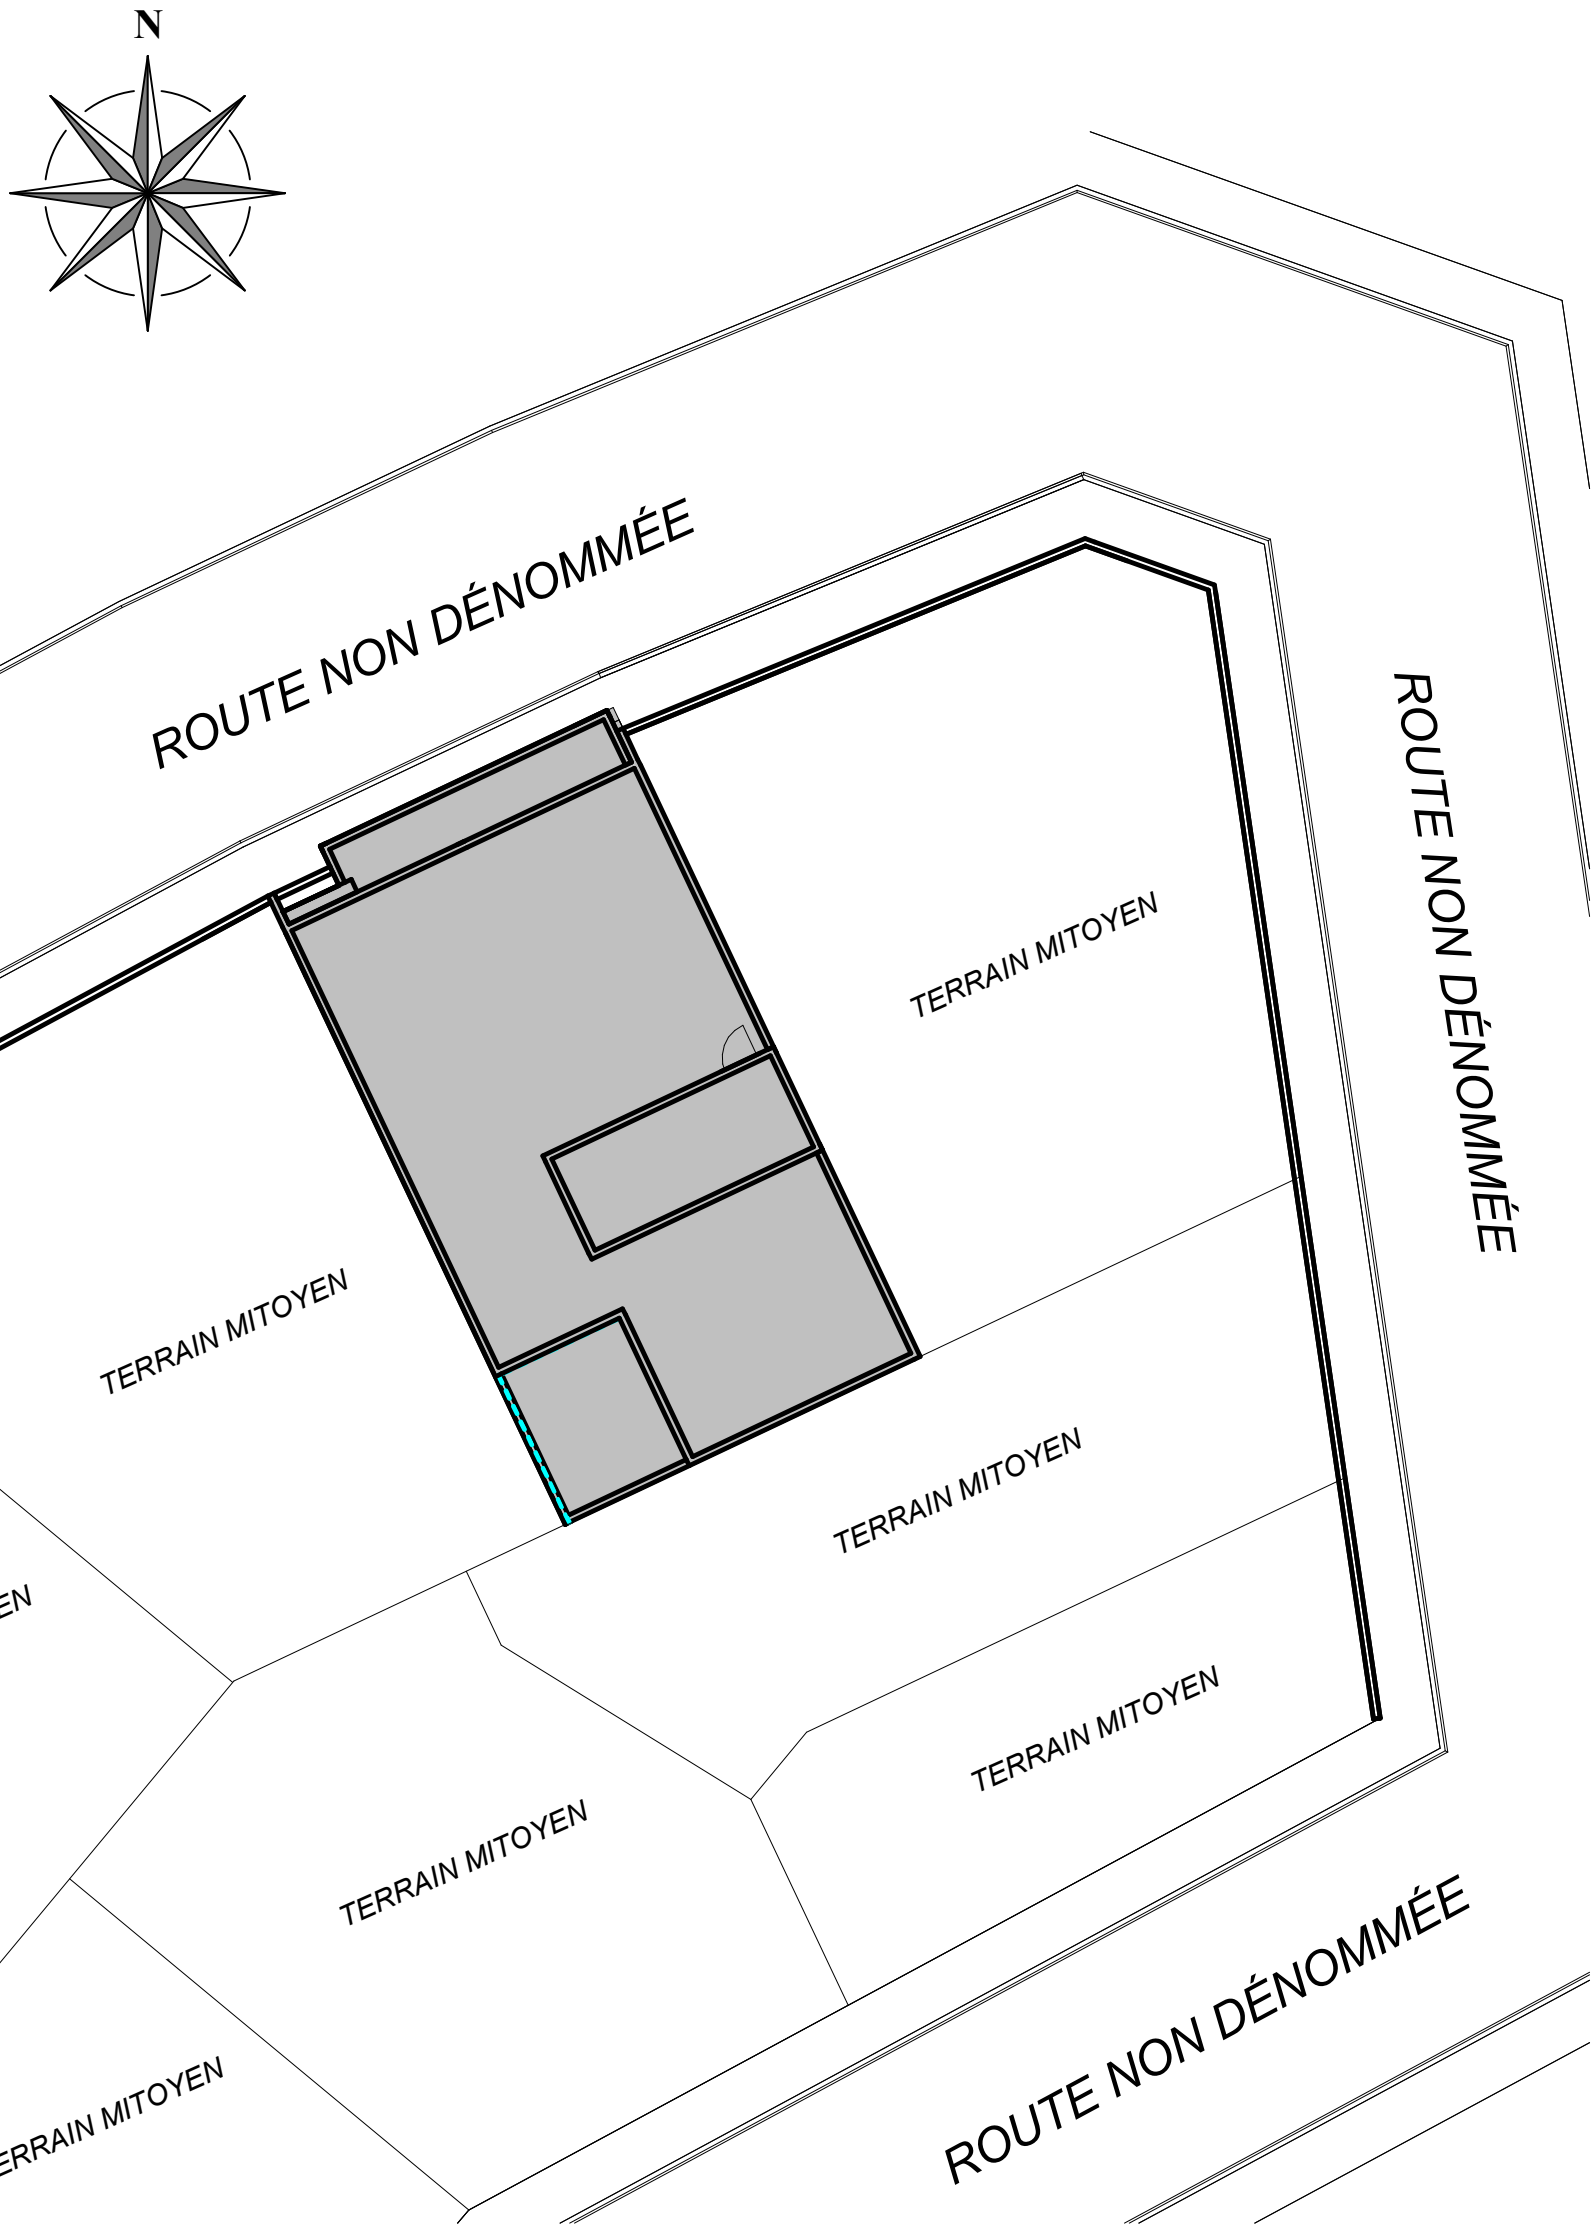

MAITRE D'OUVRAGE:

MOHAMED BADIANE


PROJET:

PROJET DE CONSTRUCTION D UNE VILLA RESIDENTIELLE SIS A MBAO

TITRE: PLAN DE MASSE

ECH:1 : 150	DWG No: 019	CAD: APS
DWR:	DATE DE FIN	

D&F ENGINEERING
Confort at home
Tel (+221) 76-141-32-23
Tel (+221) 77-234-03-20
Email: dnfengineeringsav@gmail.com

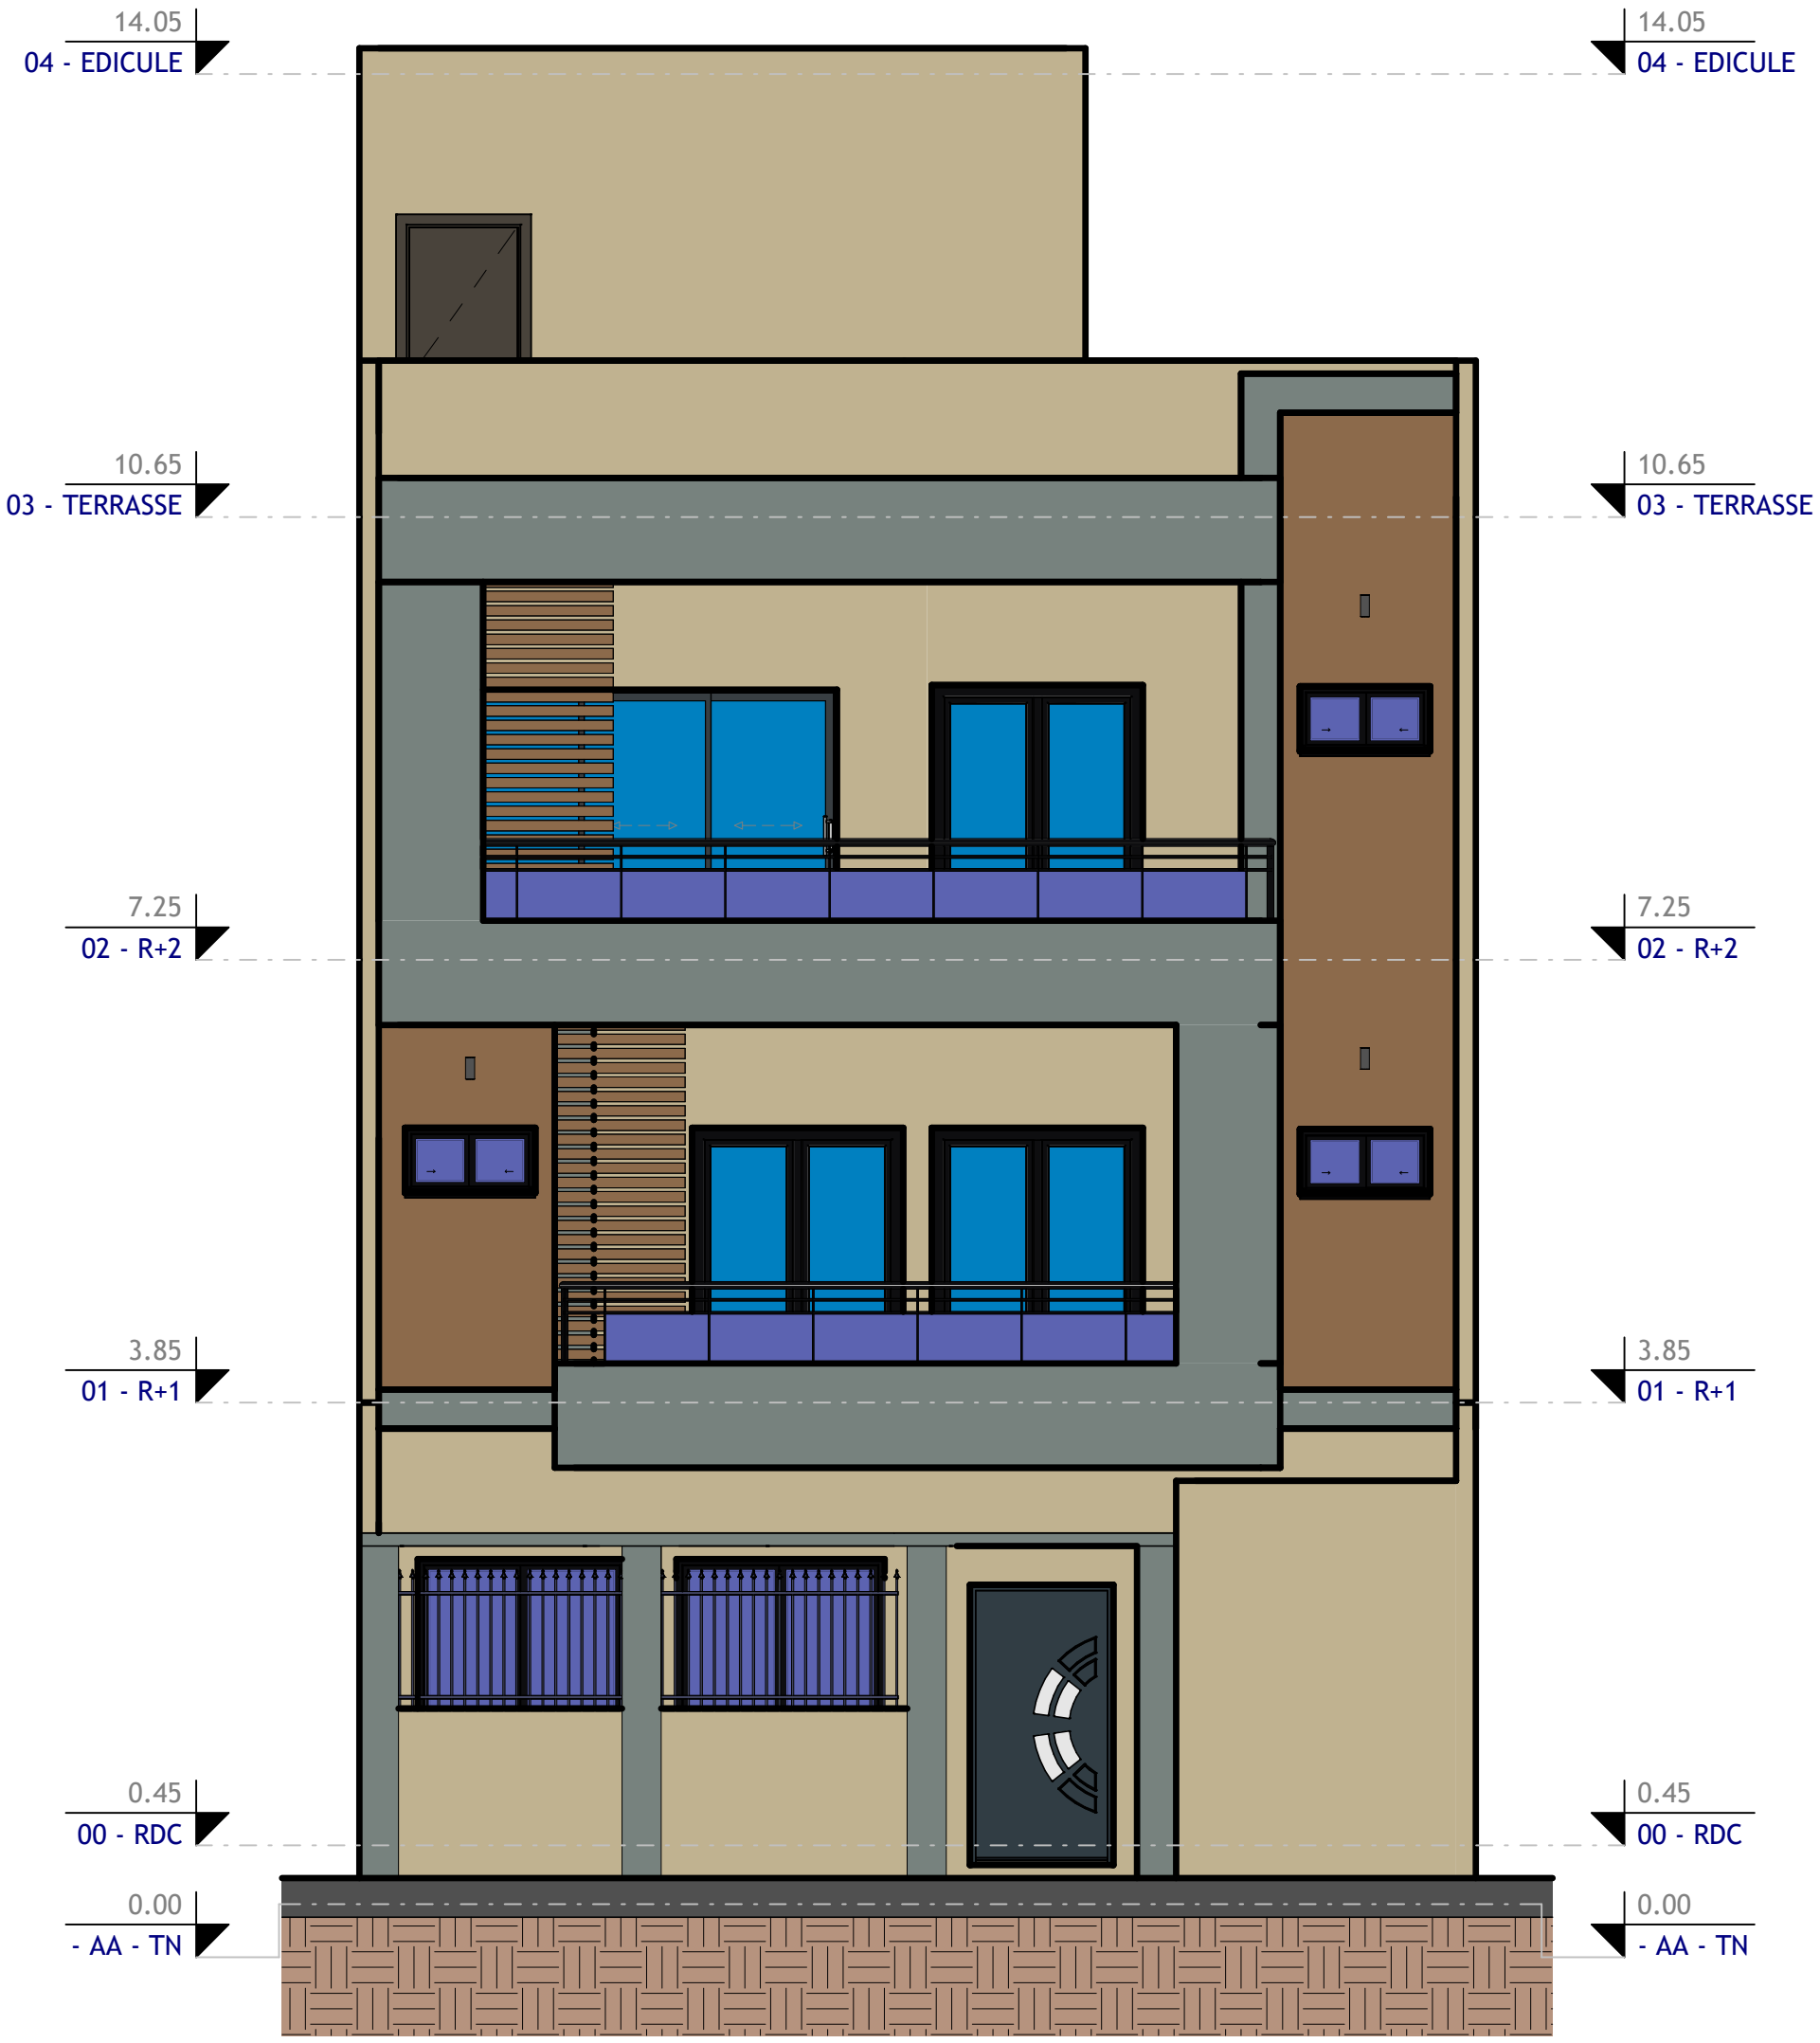

MAITRE D'OUVRAGE:

MOHAMED BADIANE


PROJET:

PROJET DE CONSTRUCTION D UNE VILLA RESIDENTIELLE SIS A MBAO

TITRE: FACADE

ECH: 1 : 50	DWG No: 020	CAD: APS
DWR:	DATE DE FIN	

D&F ENGINEERING
Confort at home
Tel (+221) 76-141-32-23
Tel (+221) 77-234-03-20
Email: dnfengineeringsav@gmail.com

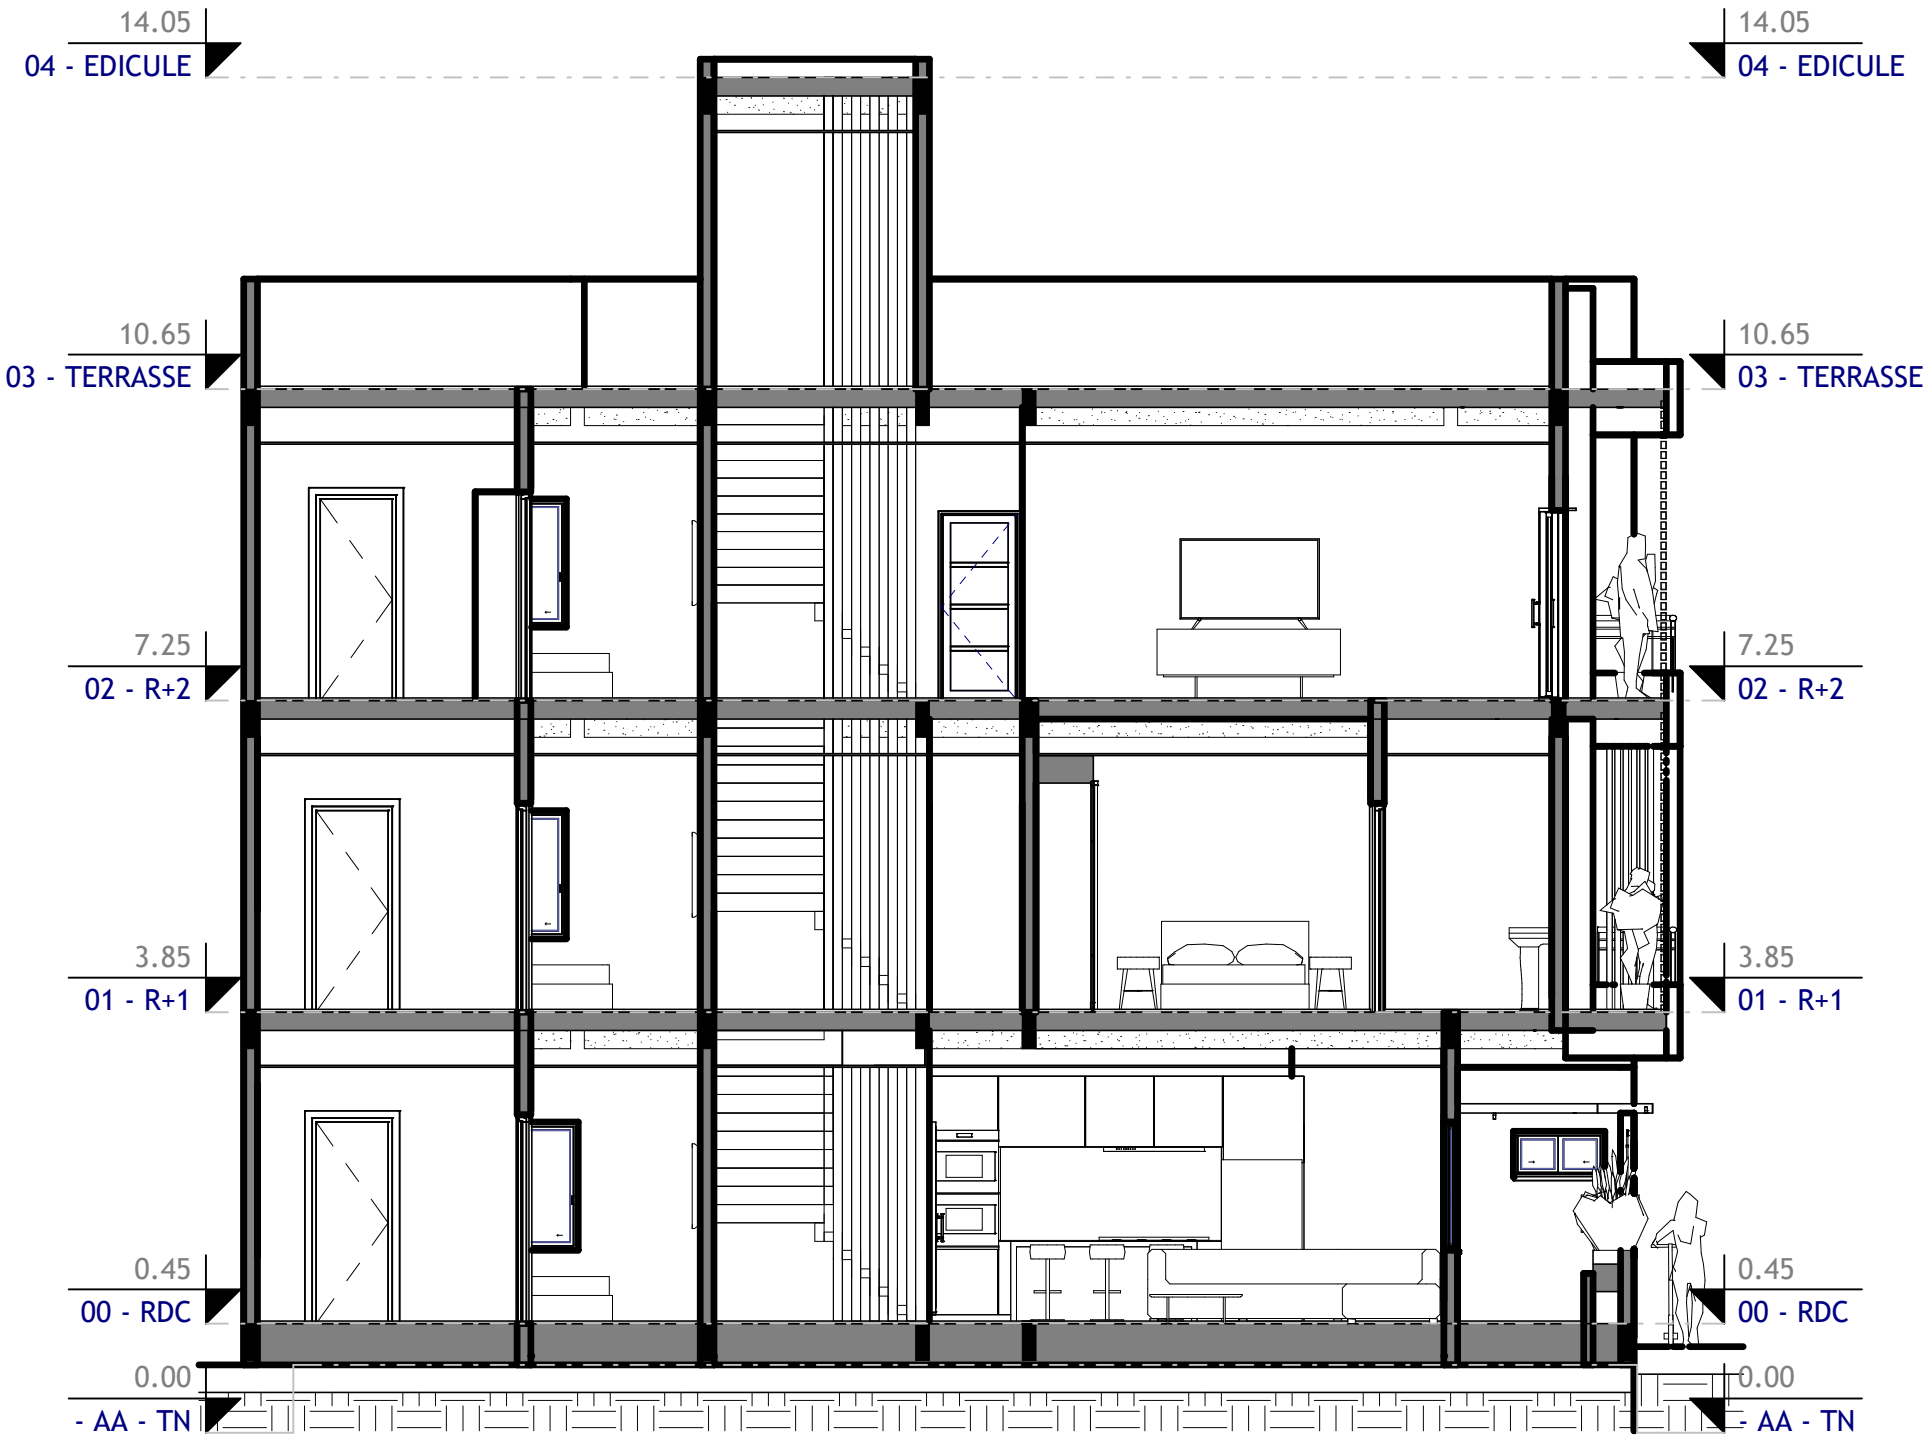

MAITRE D'OUVRAGE:

MOHAMED BADIANE


PROJET:

PROJET DE CONSTRUCTION D UNE VILLA RESIDENTIELLE SIS A MBAO

TITRE: COUPE LONGITUDINALE

ECH: 1 : 75	DWG No: 021	CAD: APS
DWR:	DATE DE FIN	

D&F ENGINEERING
Confort at home
Tel (+221) 76-141-32-23
Tel (+221) 77-234-03-20
Email: dnfengineeringsav@gmail.com

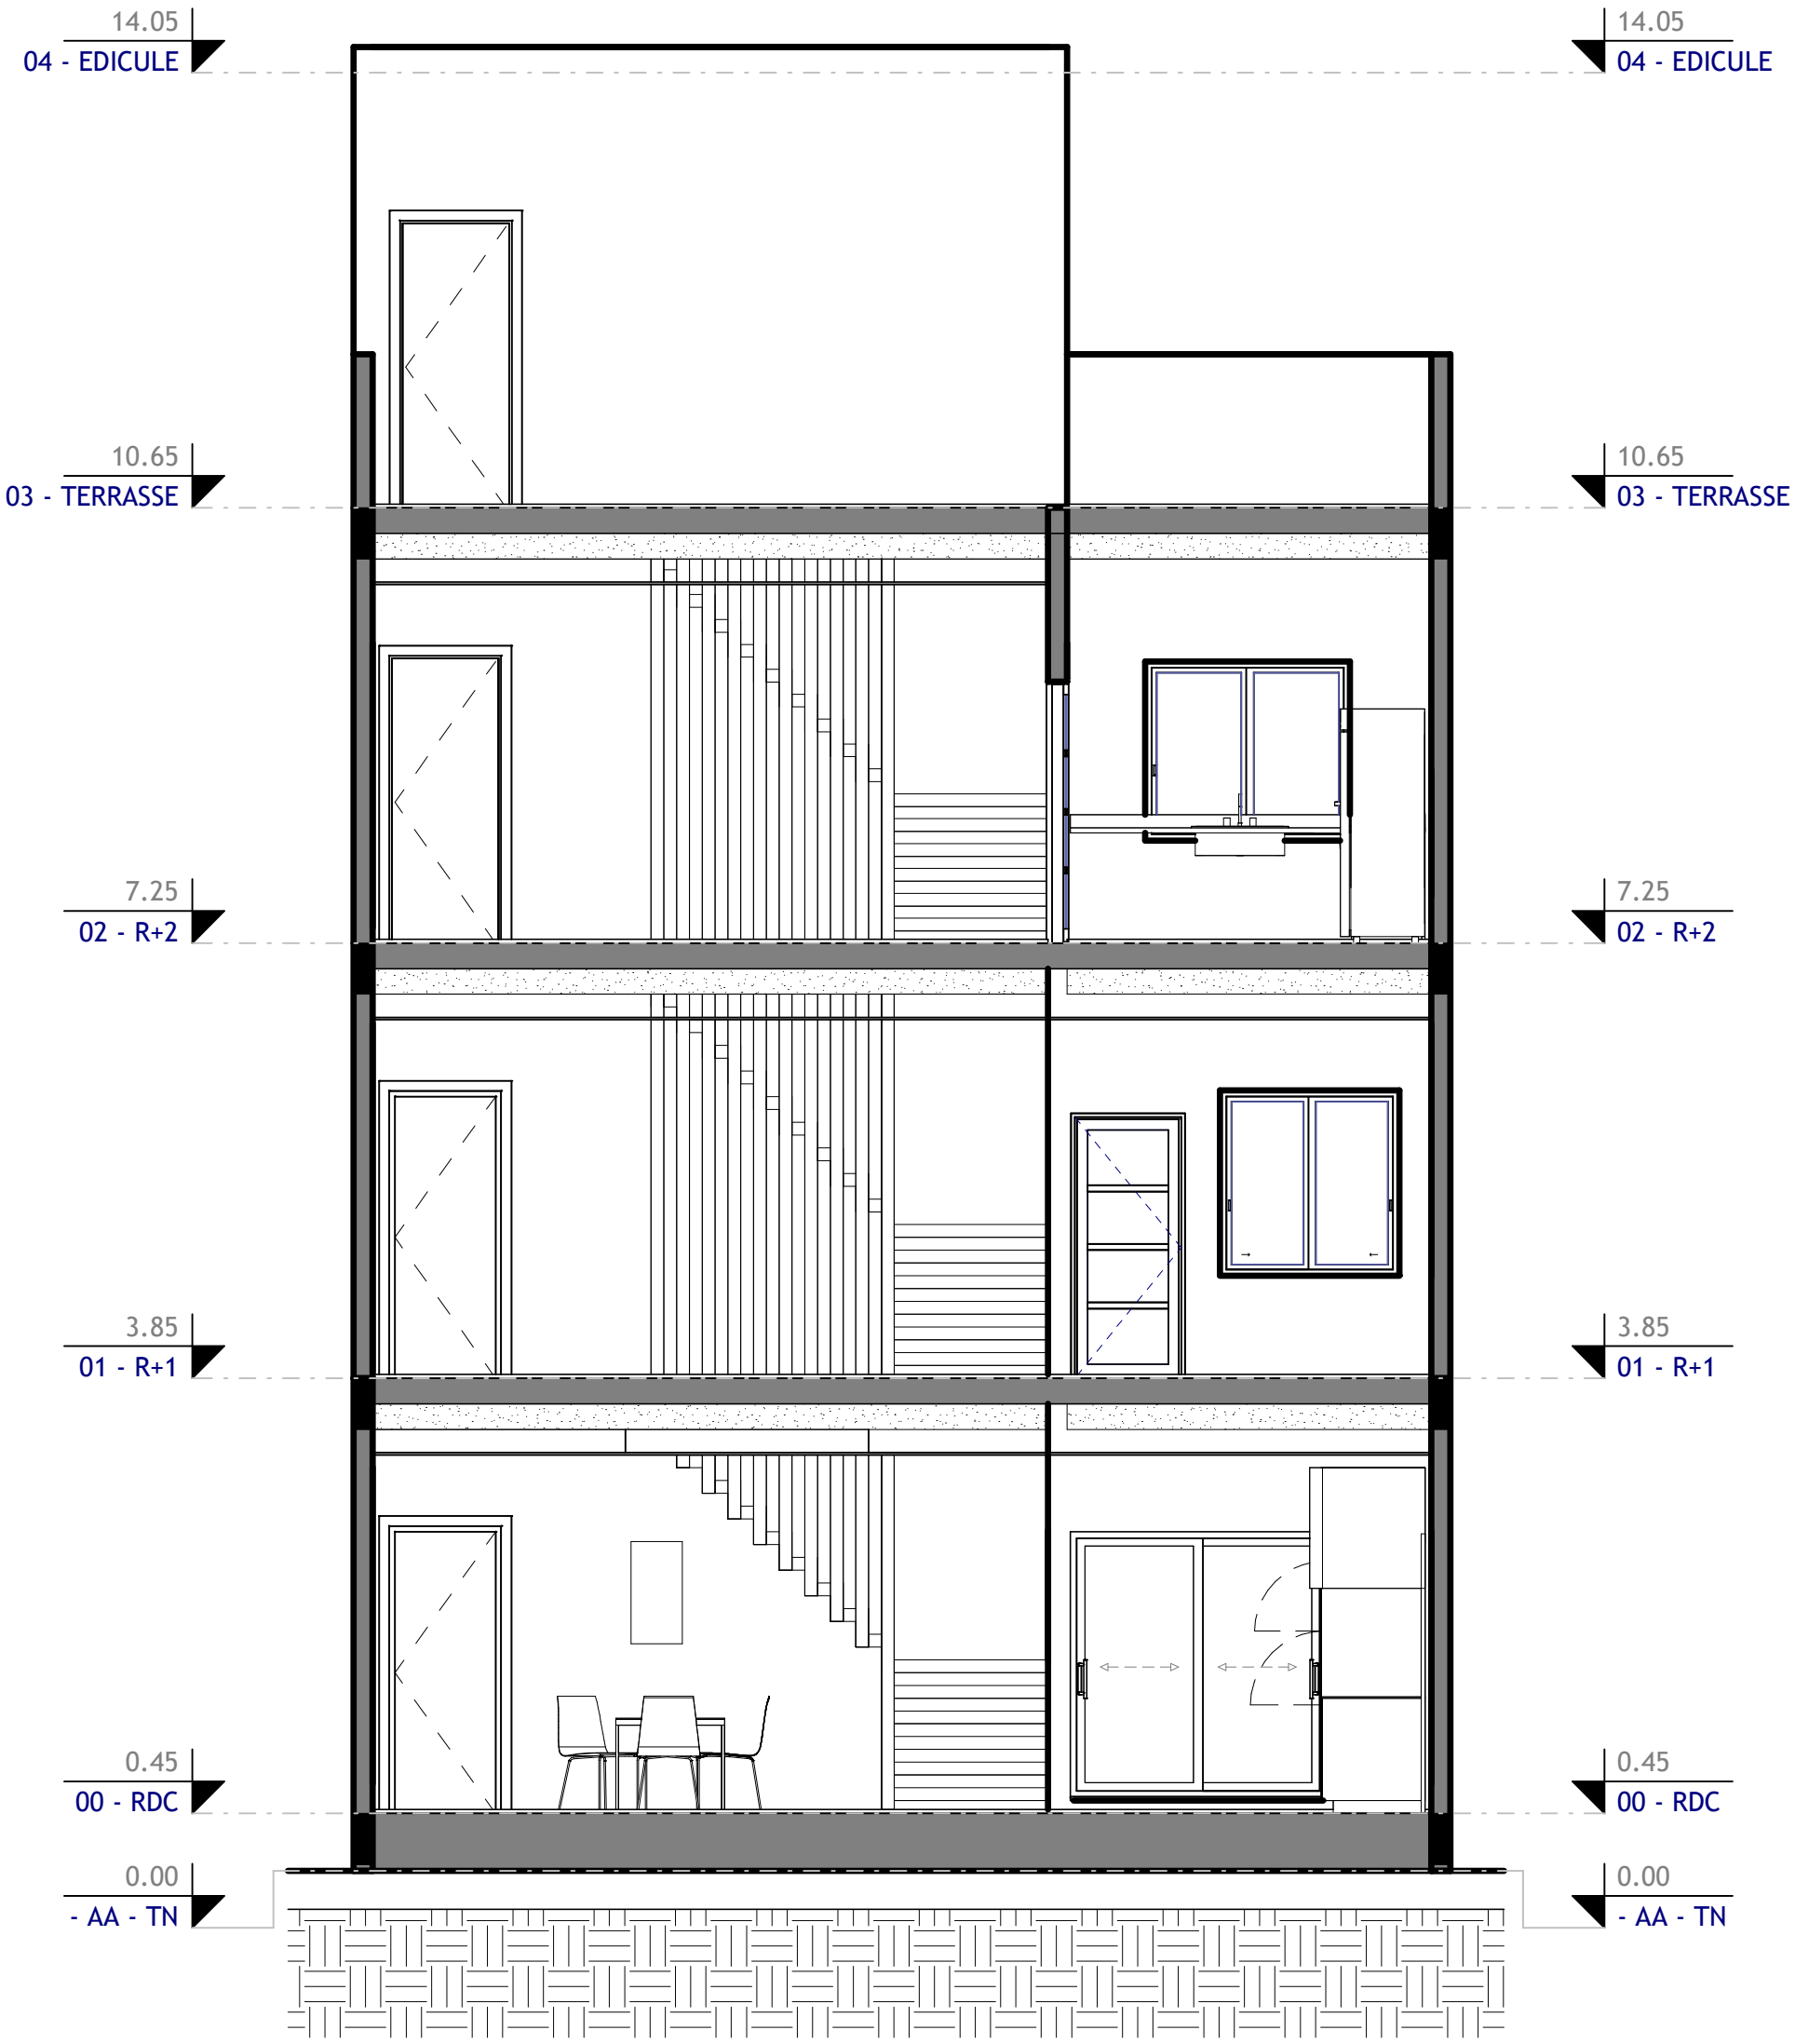

MAITRE D'OUVRAGE:

MOHAMED BADIANE

PROJET:

PROJET DE CONSTRUCTION D UNE VILLA RESIDENTIELLE SIS A MBAO

TITRE: COUPE TRANSVERSALE

ECH: 1 : 50	DWG No: 022	CAD: APS
DWR:	DATE DE FIN	

D&F ENGINEERING
Confort at home
Tel (+221) 76-141-32-23
Tel (+221) 77-234-03-20
Email: dnfengineeringsav@gmail.com