

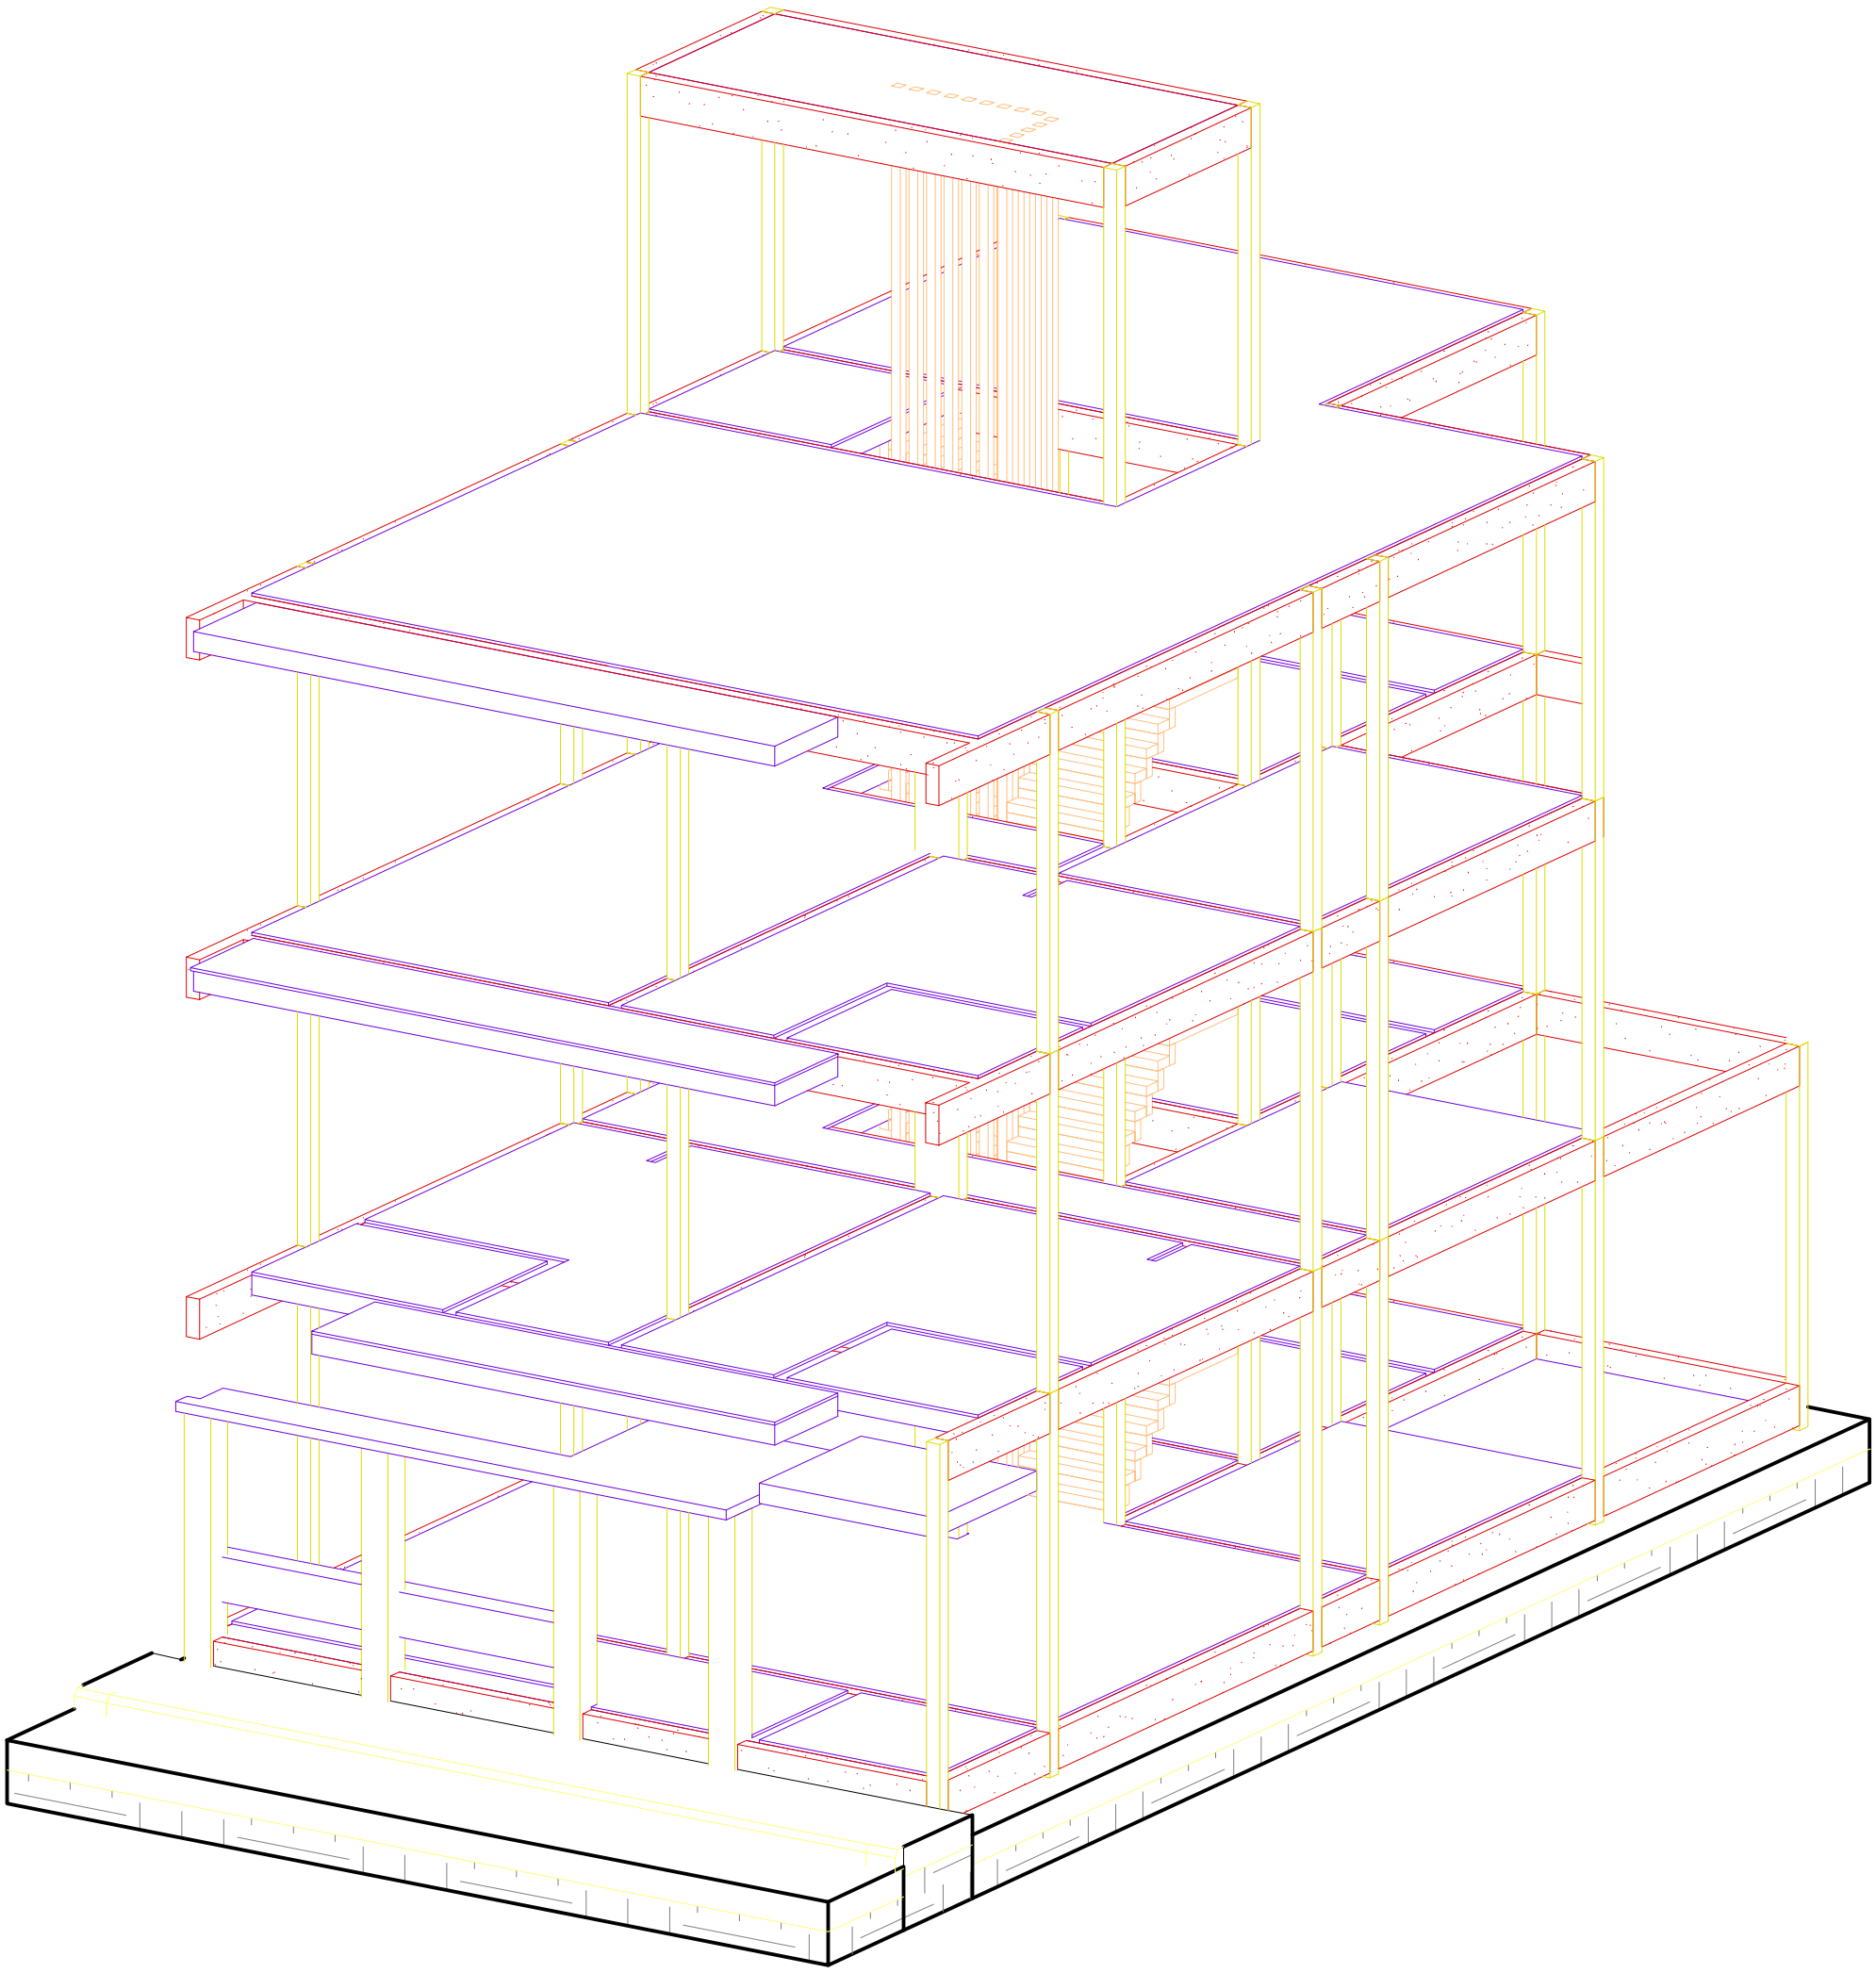



D&F ENGINEERING Confort at home	**D&F ENGINEERING** **D&F ENGINNERING SARL** **SCAT URBAM VILLA 67H** **17086 DAKAR / LIBERTE** **77 234 03 20/ 76 141 32 23**	**Projet Mohamed BADIANE** BATIMENT R+2 USAGE D'HABITATION MBAO	N° d' affaire :		N° PLAN	
			Indice	Date	Début :	
					Dessiné par :MD	
					Vérifié par :	

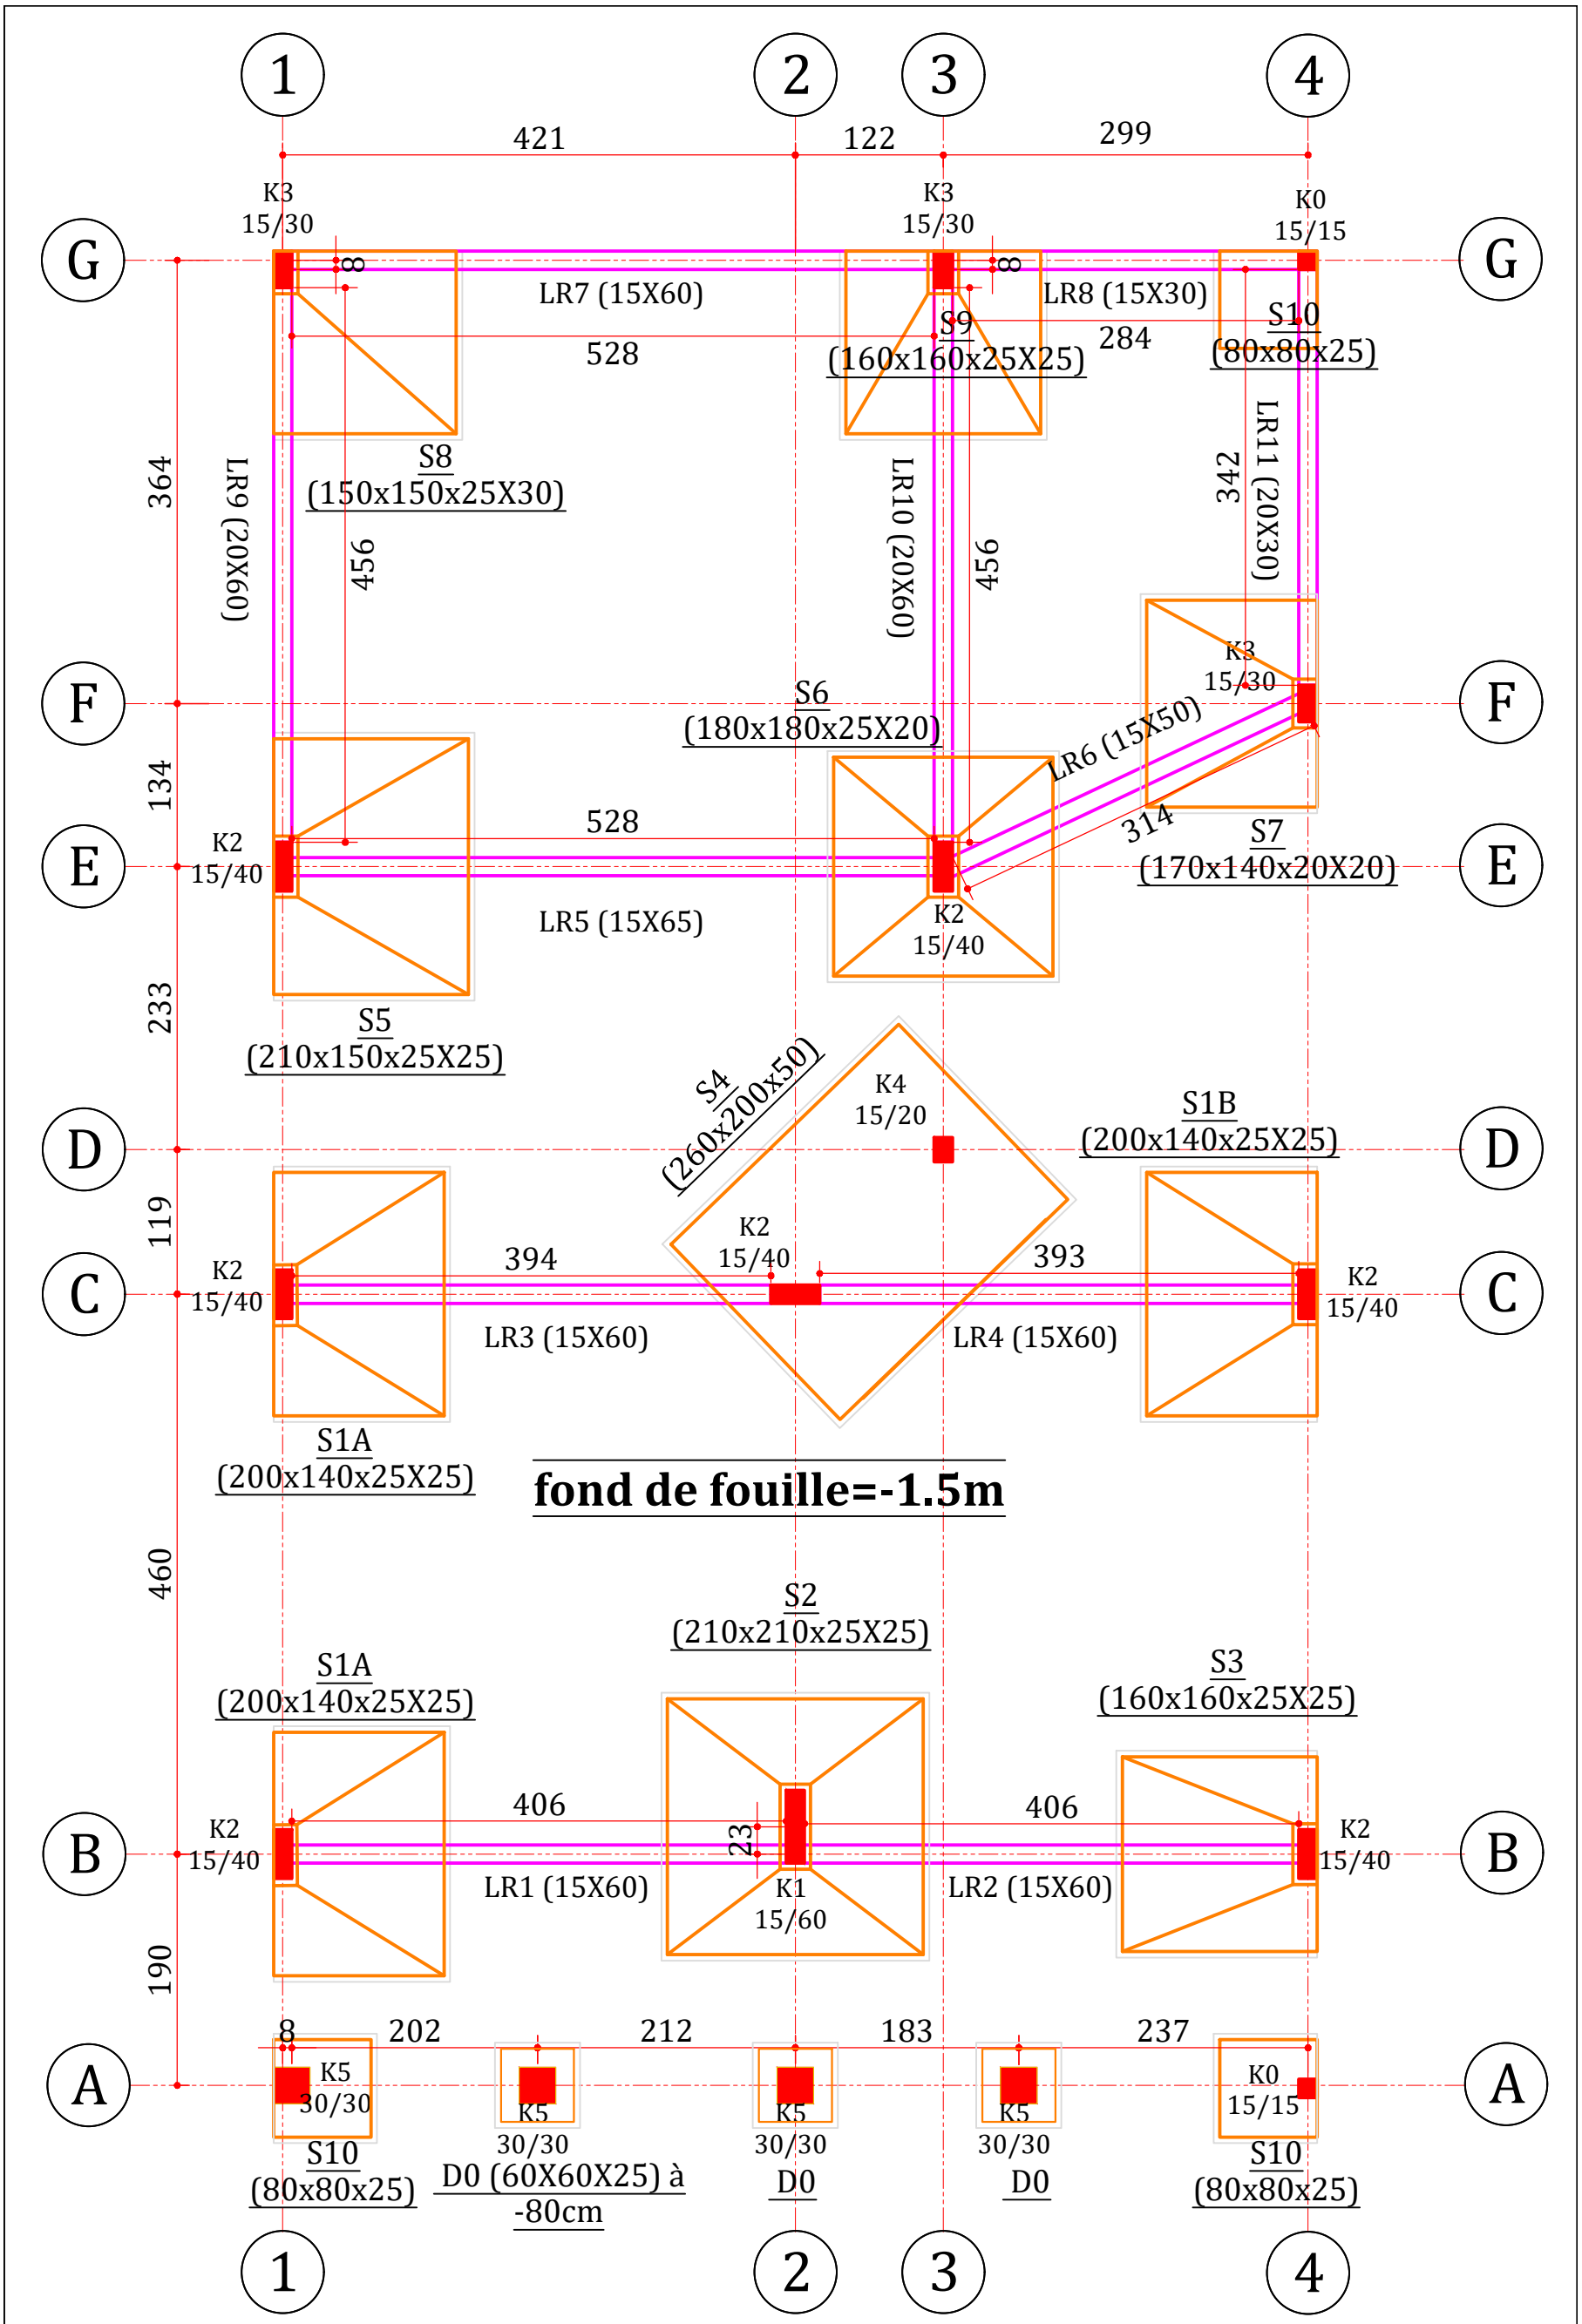


D&F ENGINEERING	**D&F ENGINEERING** **D&F ENGINNERING SARL** **SCAT URBAM VILLA 67H** **17086 DAKAR / LIBERTE** **77 234 03 20/ 76 141 32 23**	**Projet Mohamed BADIANE** COFFRAGE FONDATION	N° d' affaire :		N° PLAN
			Indice / Date		Début :
					Dessiné par :MD
					Vérifié par :

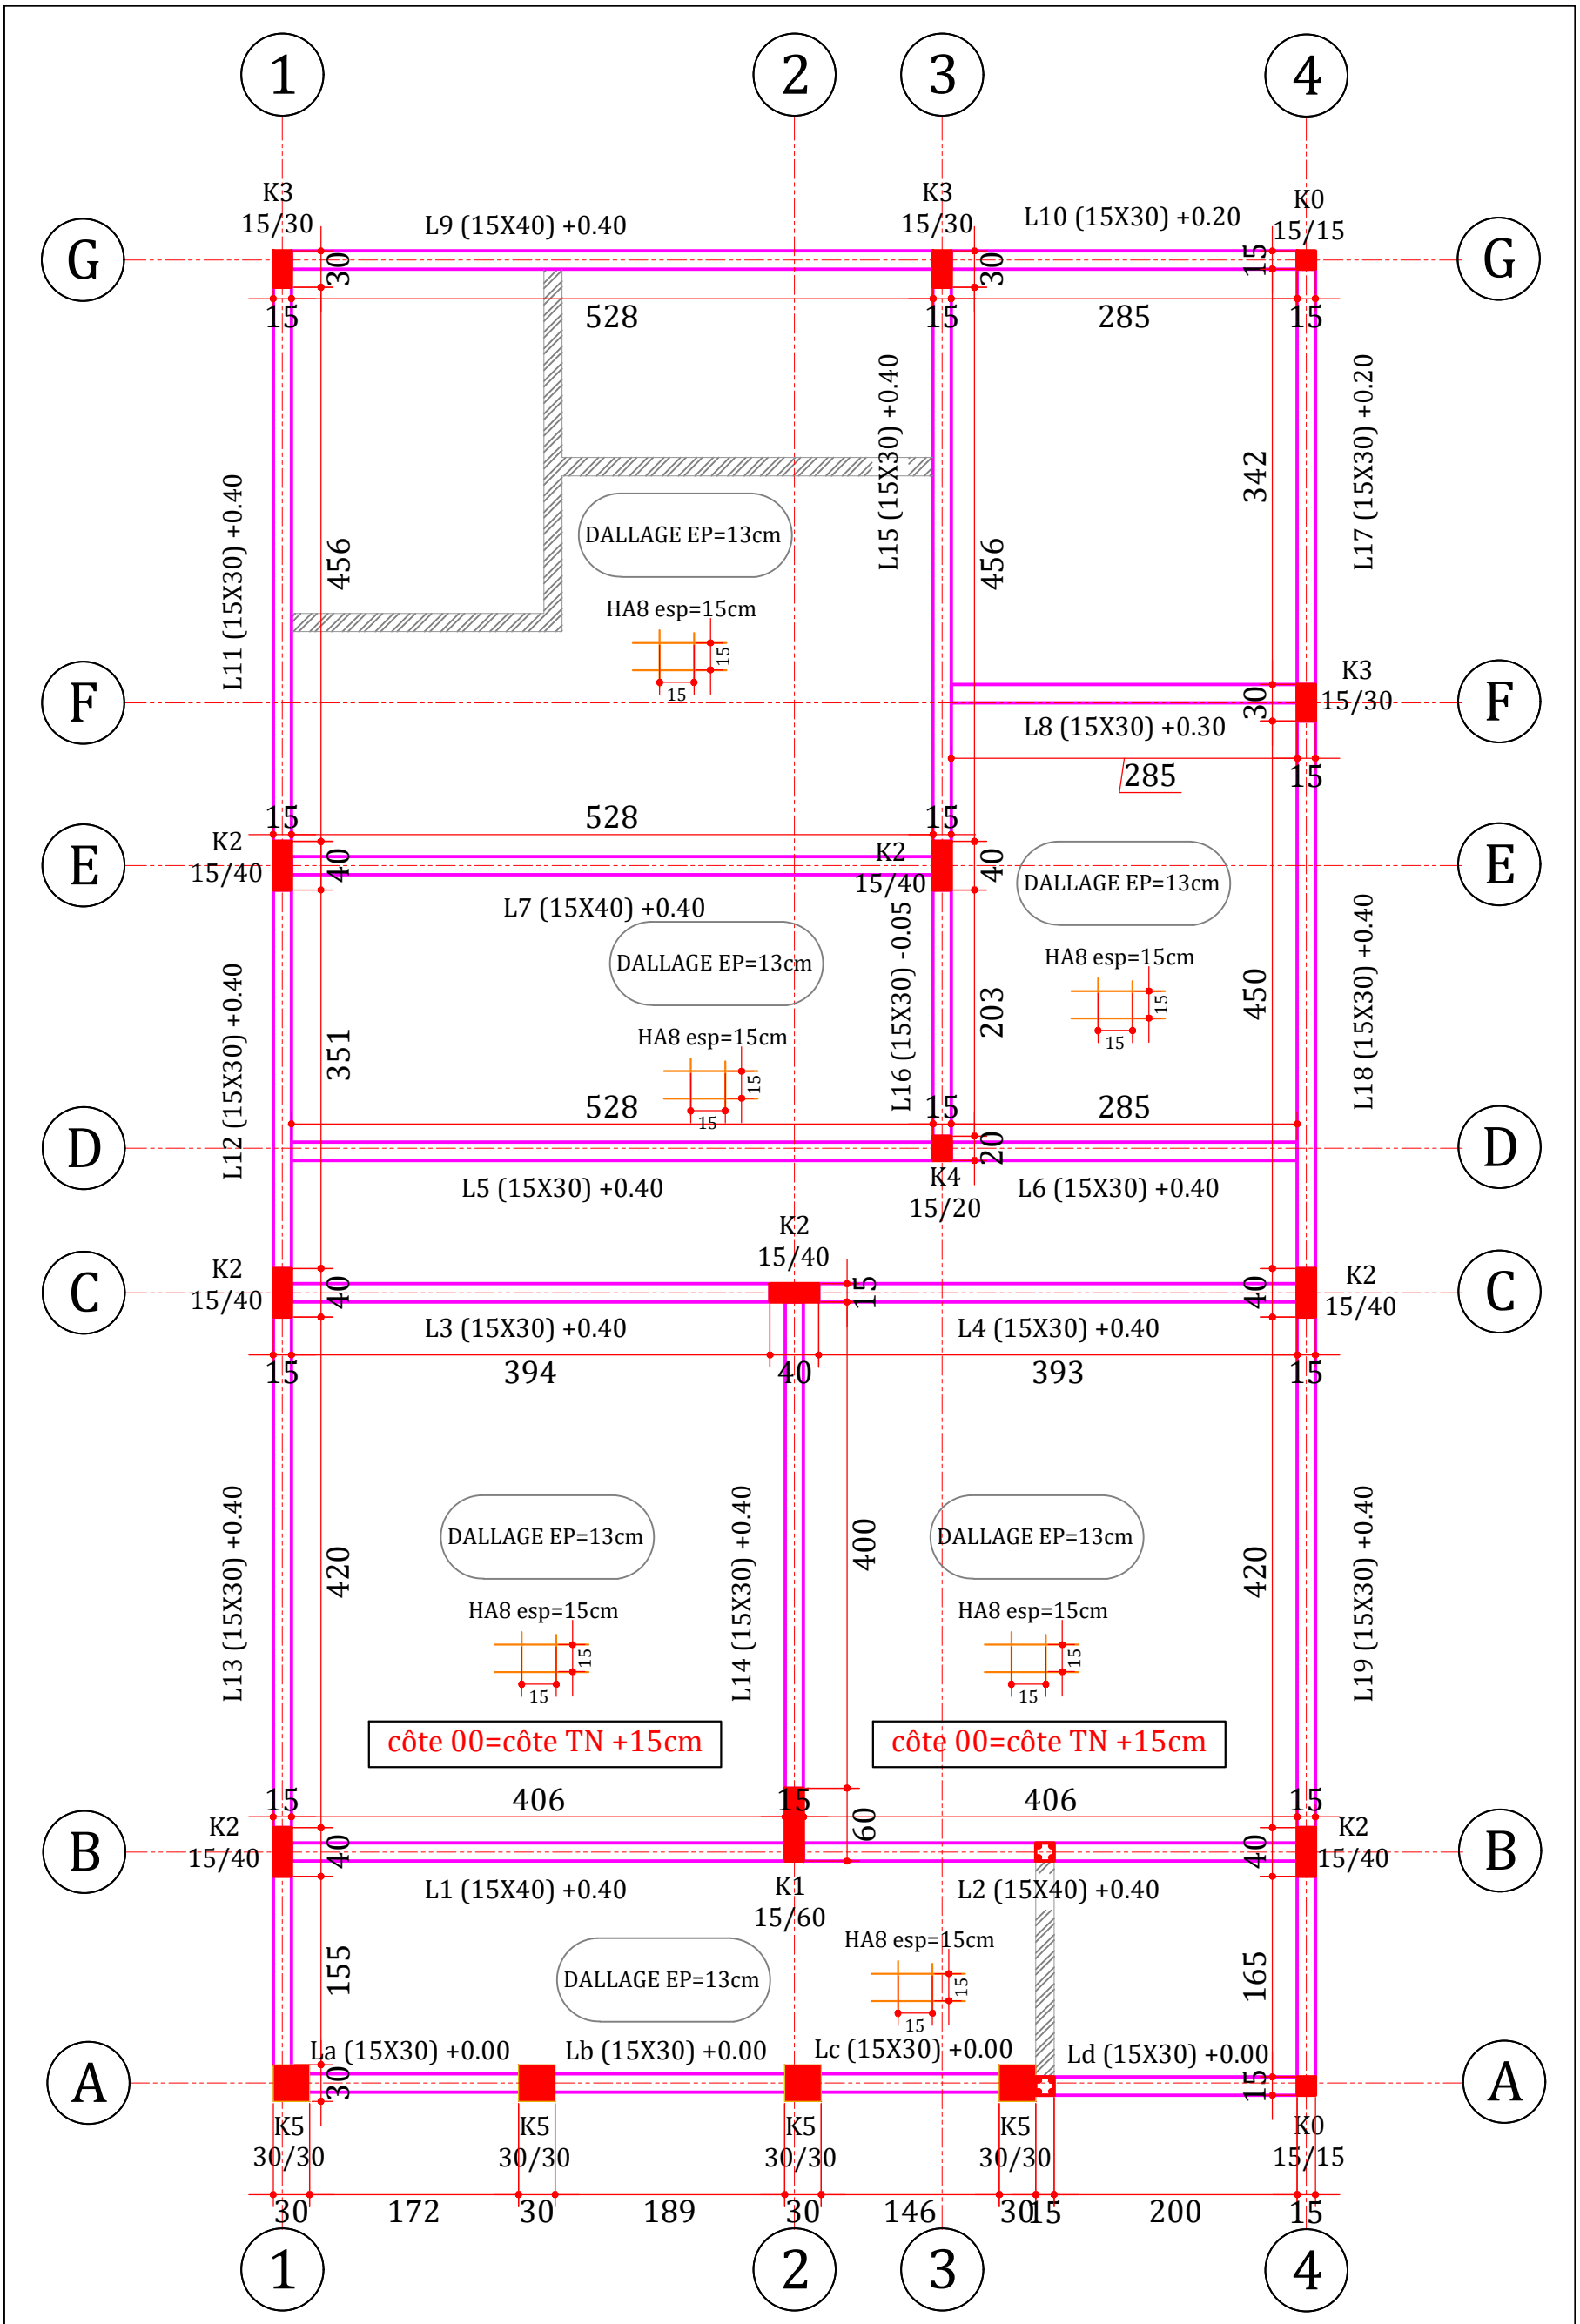


D&F ENGINEERING	**D&F ENGINEERING** **D&F ENGINNERING SARL** **SCAT URBAM VILLA 67H** **17086 DAKAR / LIBERTE** **77 234 03 20/ 76 141 32 23**	**Projet Mohamed BADIANE** COFFRAGE DALLAGE	N° d' affaire :		N° PLAN
			Indice / Date		Début :
					Dessiné par :MD
					Vérifié par :

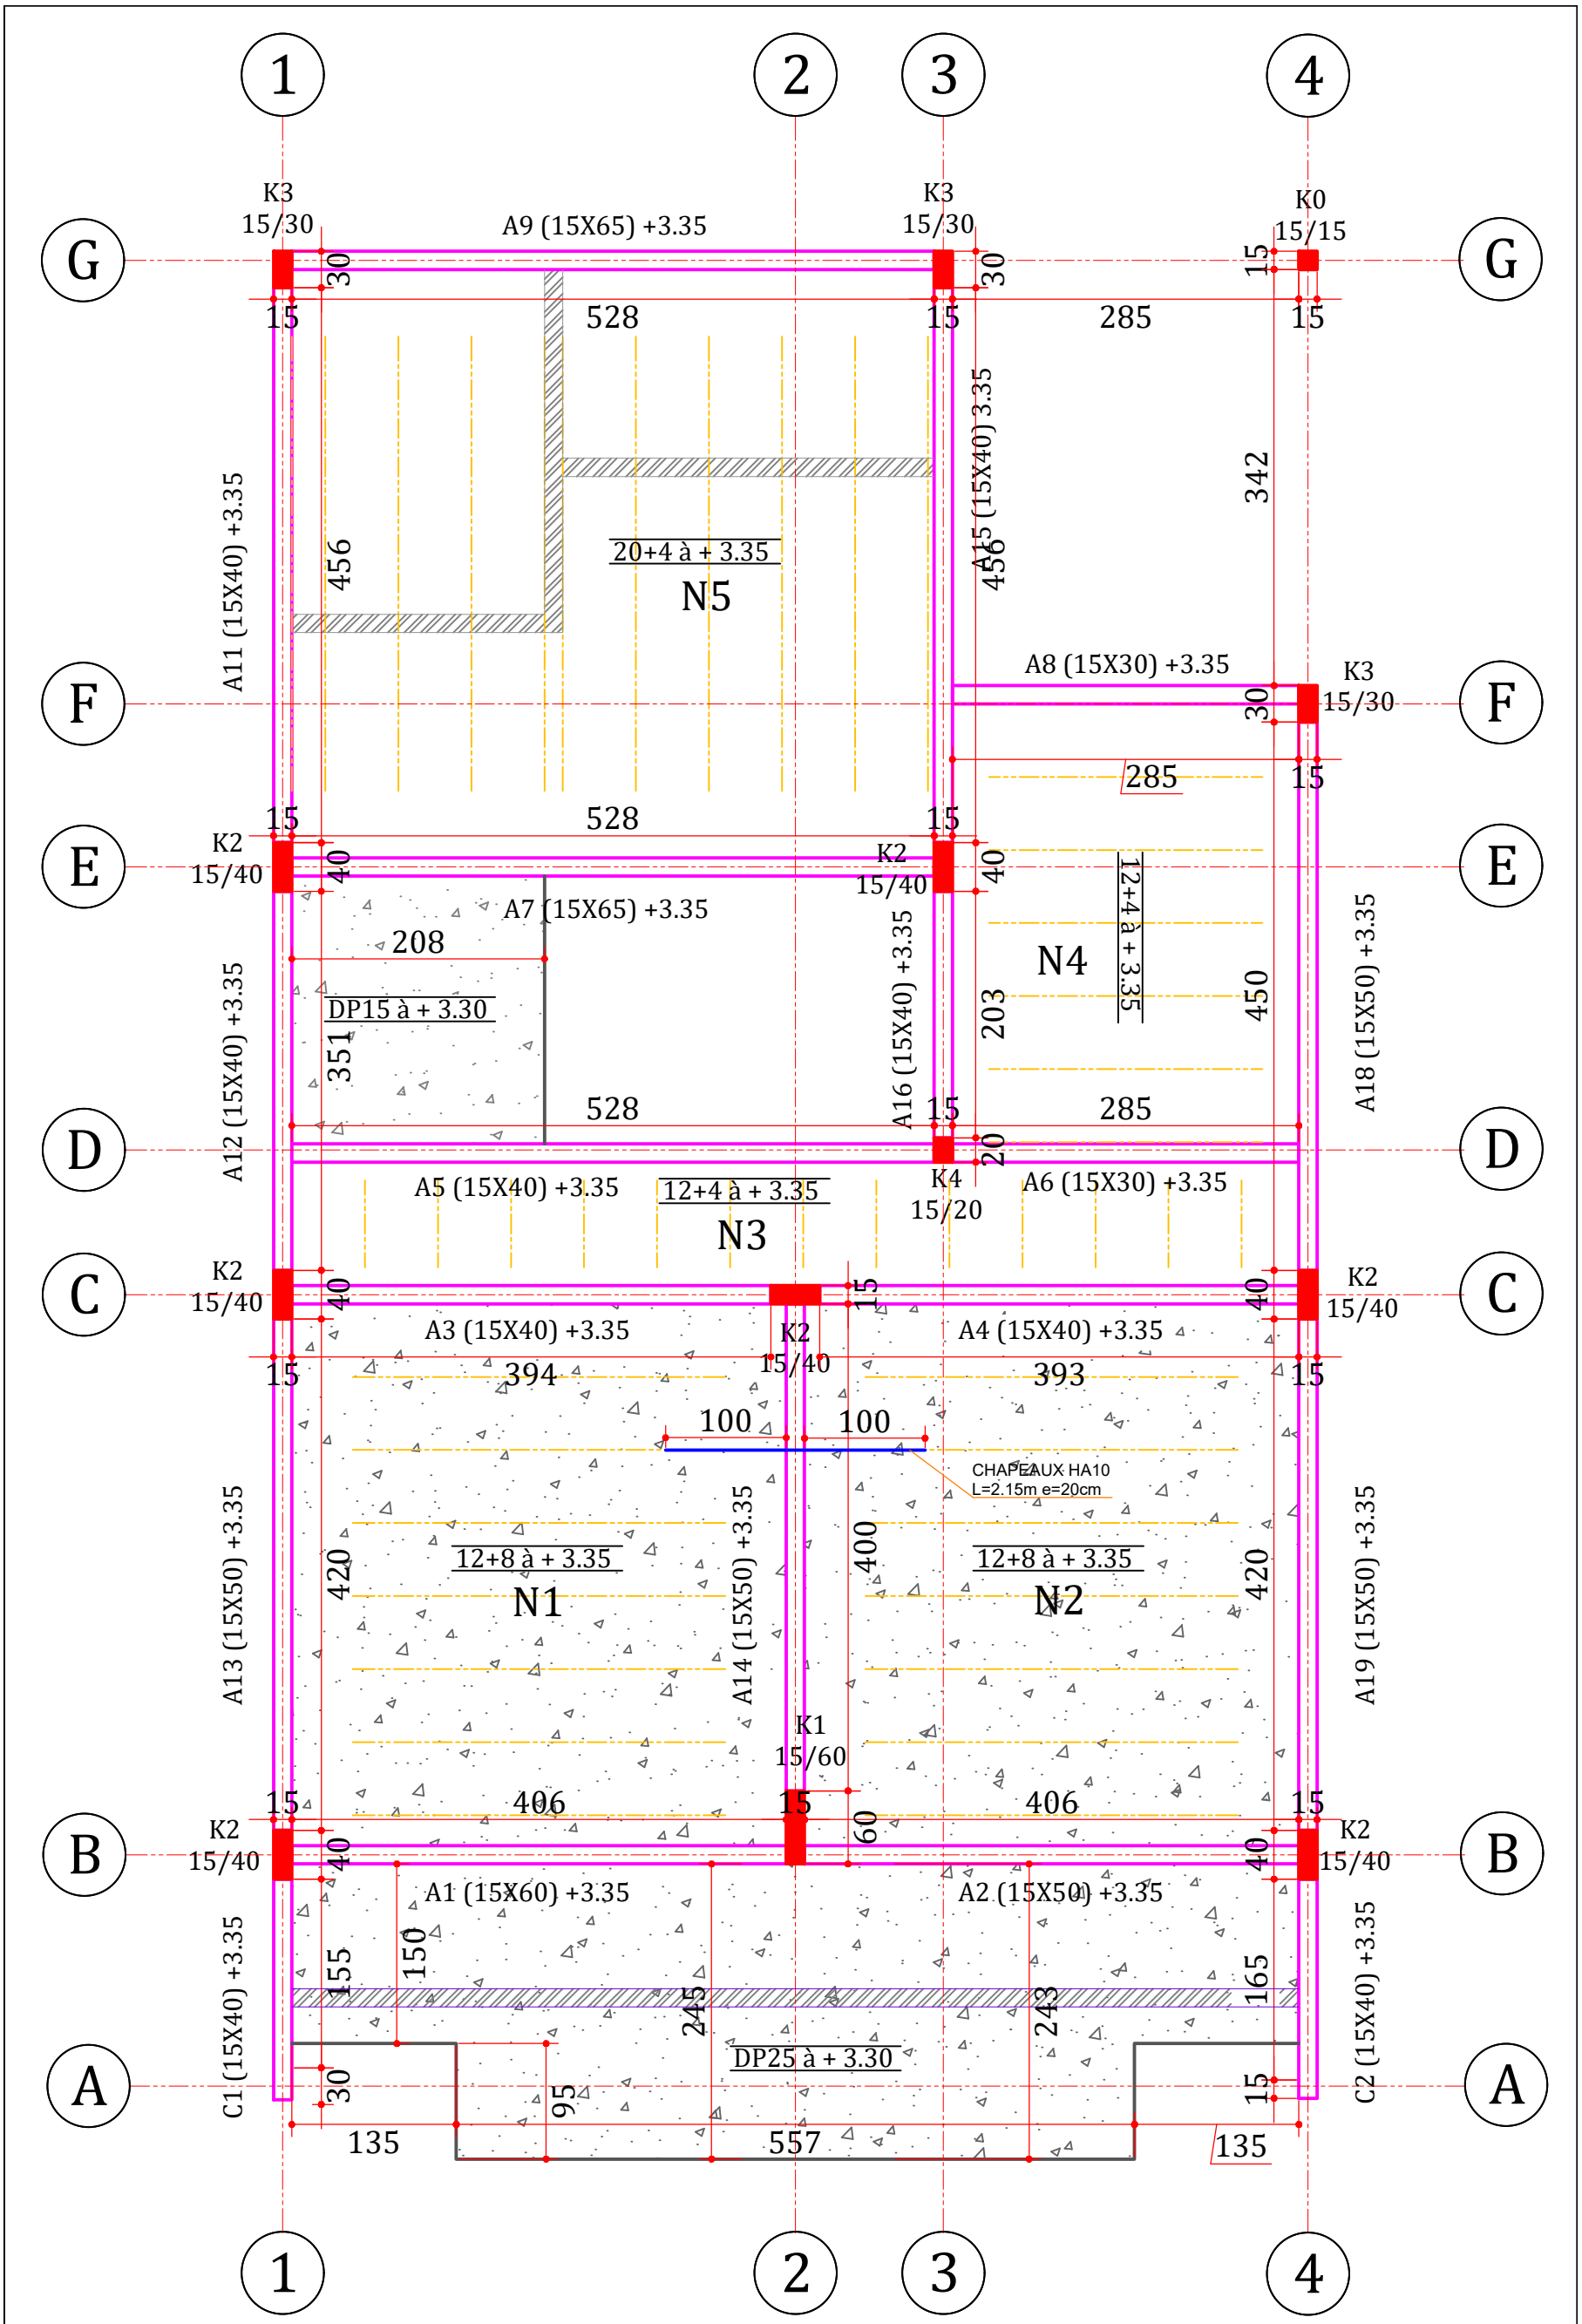


D&F ENGINEERING	**D&F ENGINEERING** **D&F ENGINNERING SARL** **SCAT URBAM VILLA 67H** **17086 DAKAR / LIBERTE** **77 234 03 20/ 76 141 32 23**	**Projet Mohamed BADIANE** COFFRAGE PH RDC	N° d' affaire :	N° PLAN
			Indice / Date	Début :
				Dessiné par :MD
				Vérifié par :

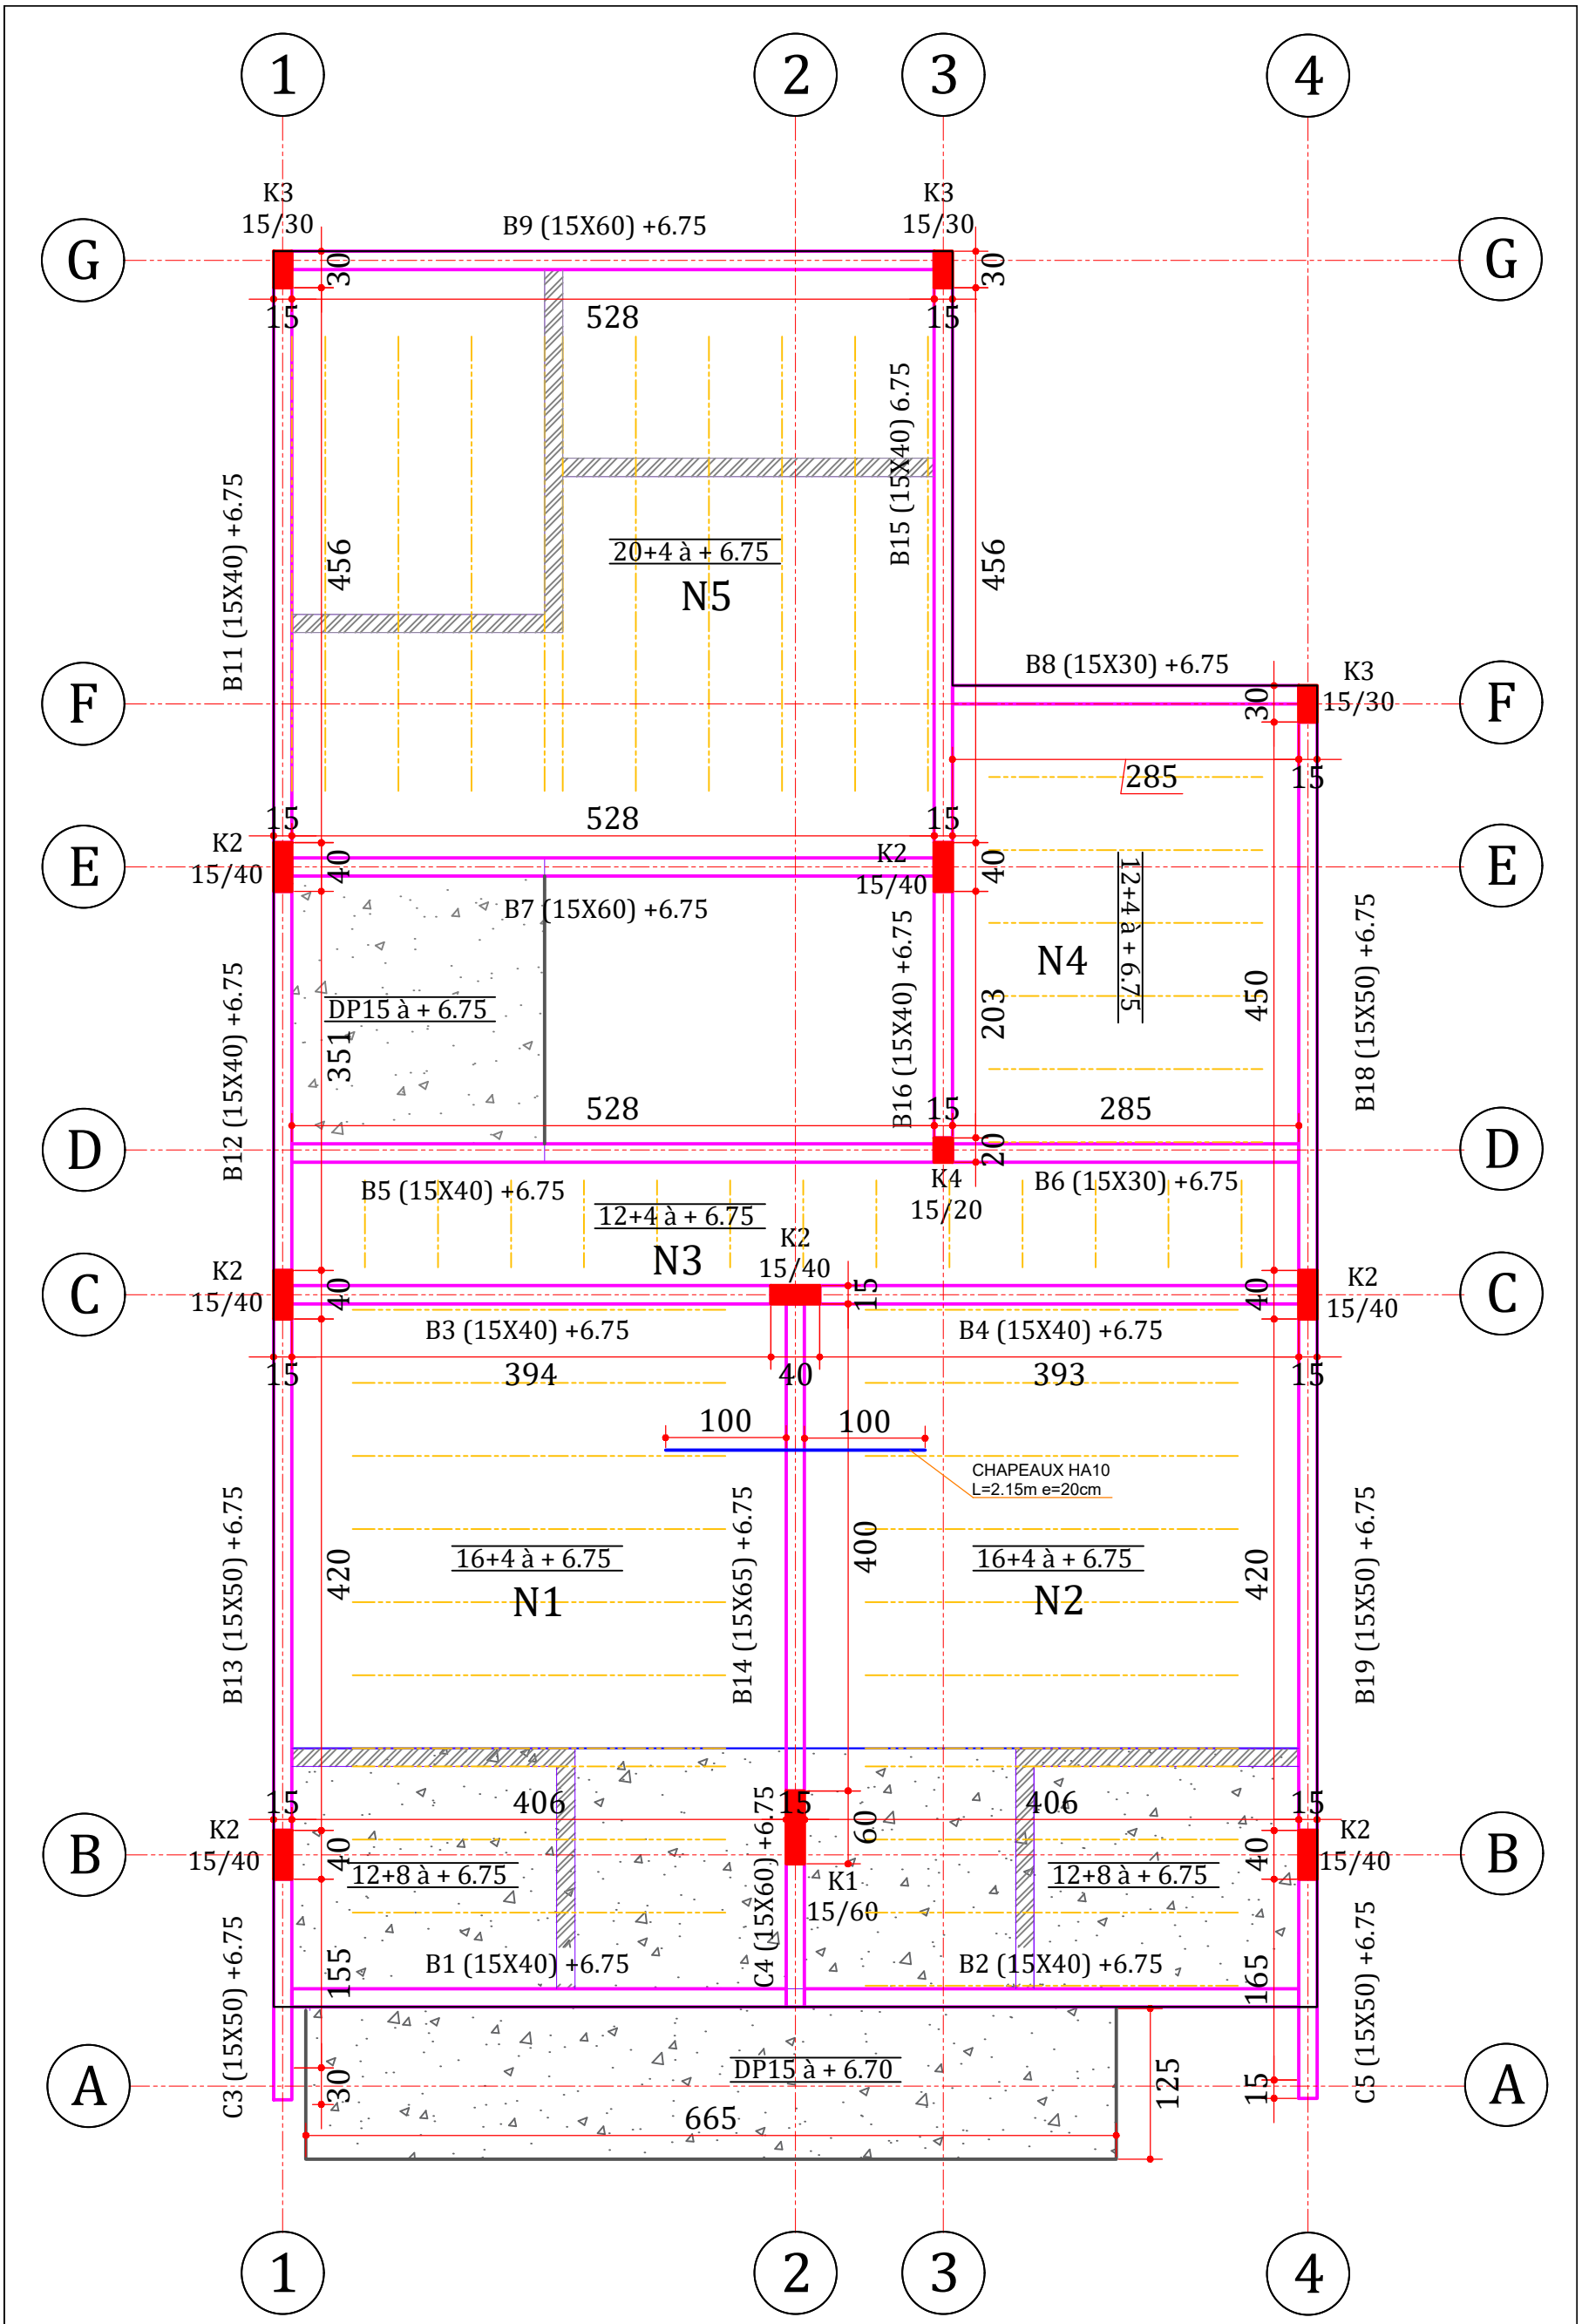


D&F ENGINEERING	**D&F ENGINEERING** **D&F ENGINNERING SARL** **SCAT URBAM VILLA 67H** **17086 DAKAR / LIBERTE** **77 234 03 20/ 76 141 32 23**	**Projet Mohamed BADIANE** COFFRAGE PH ETAGE	N° d' affaire :		N° PLAN
			Indice / Date		Début :
					Dessiné par :MD
					Vérifié par :

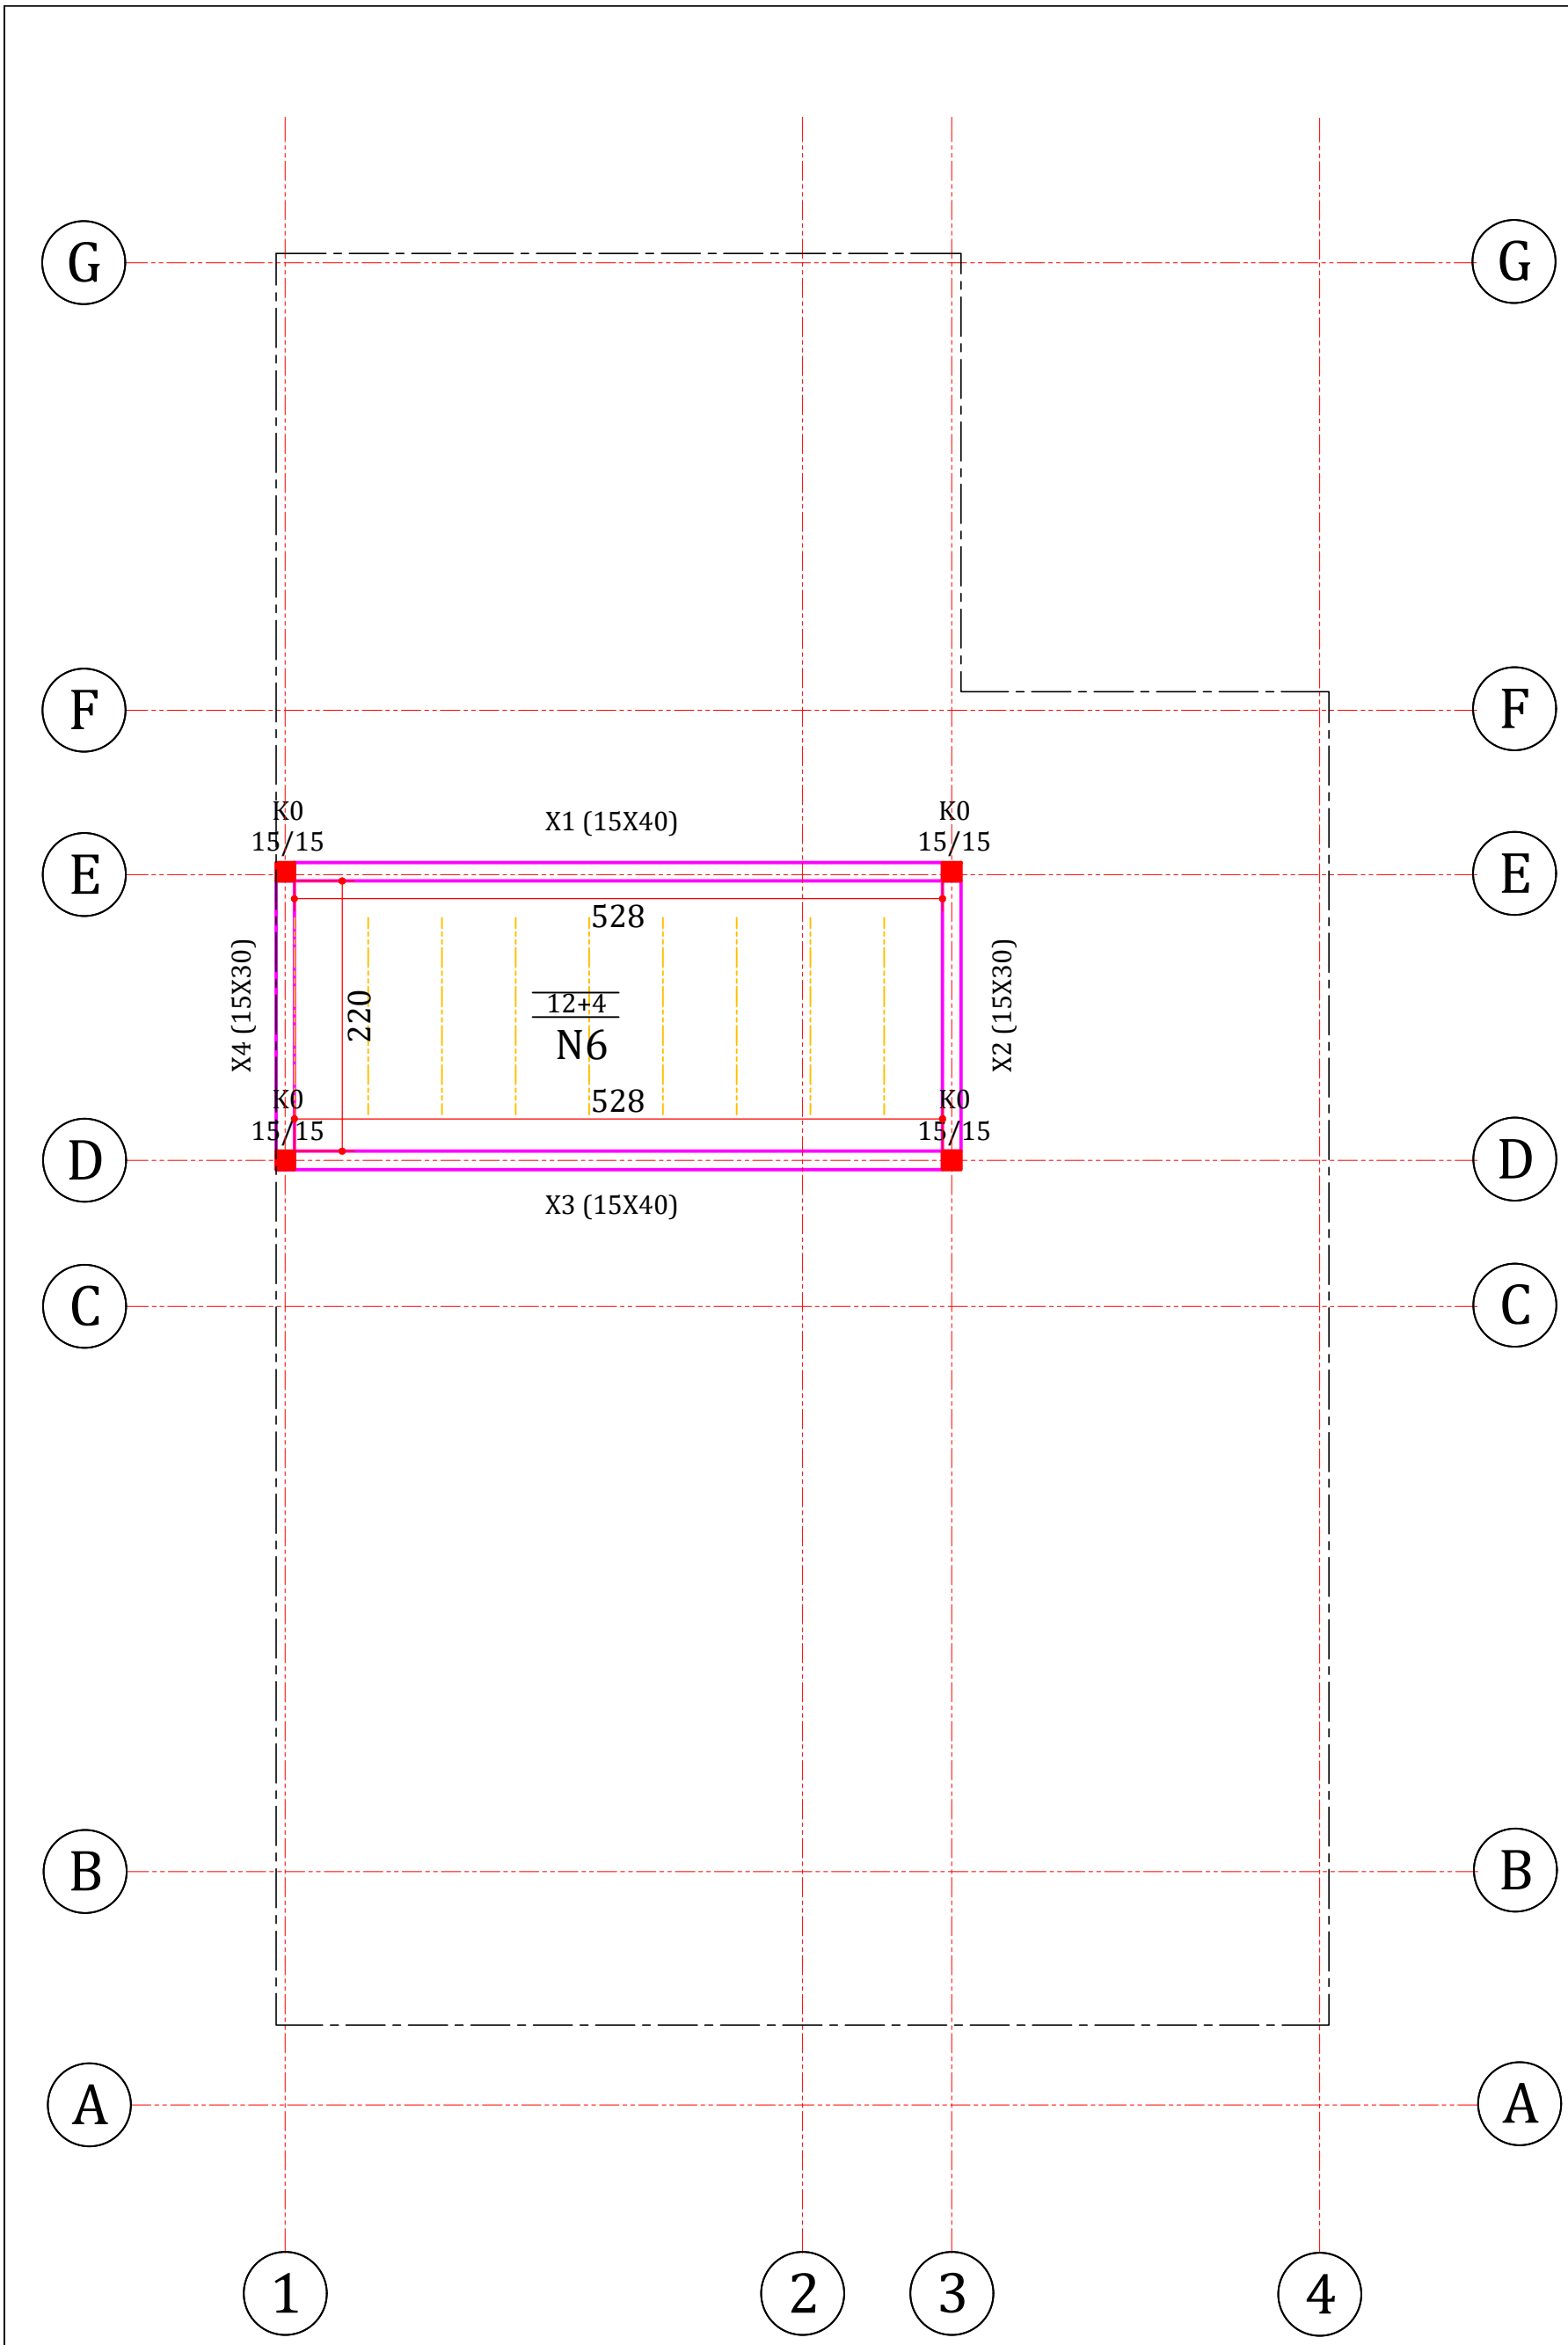


D&F ENGINEERING	**D&F ENGINEERING** **D&F ENGINNERING SARL** **SCAT URBAM VILLA 67H** **17086 DAKAR / LIBERTE** **77 234 03 20/ 76 141 32 23**	**Projet Mohamed BADIANE** COFFRAGE EDICULE	N° d' affaire :		N° PLAN
			Indice / Date		Début :
					Dessiné par :MD
					Vérifié par :

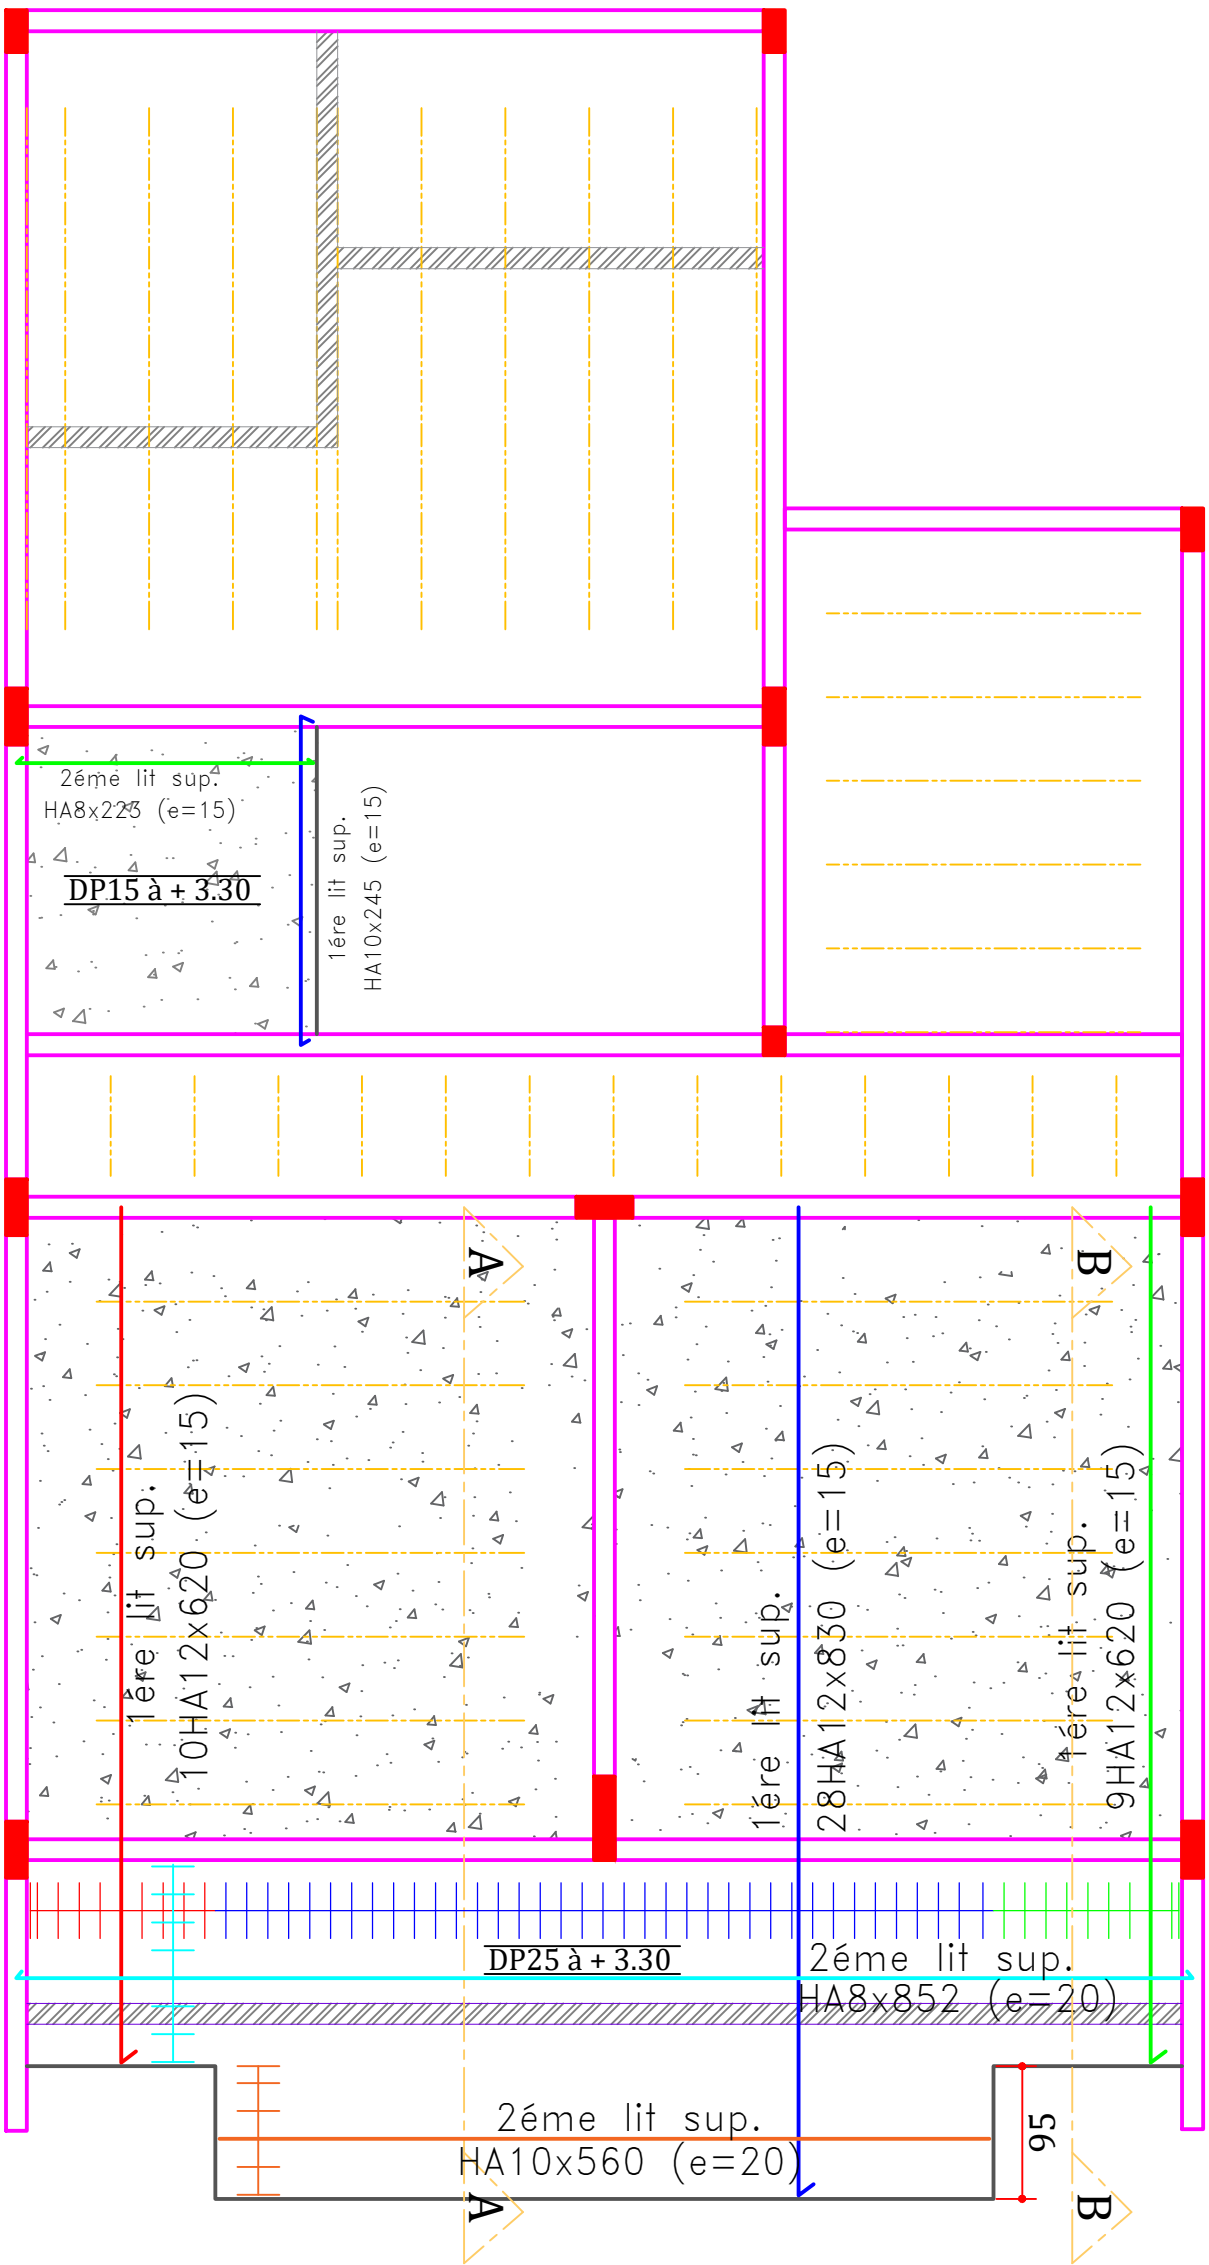


D&F ENGINEERING	**D&F ENGINEERING** **D&F ENGINNERING SARL** **SCAT URBAM VILLA 67H** **17086 DAKAR / LIBERTE** **77 234 03 20/ 76 141 32 23**	**Projet Mohamed BADIANE** FERRAILLAGE DP RDC NAPPE SUPERIEURE	N° d' affaire :		N° PLAN
			Indice / Date		Début :
					Dessiné par :MD
					Vérifié par :

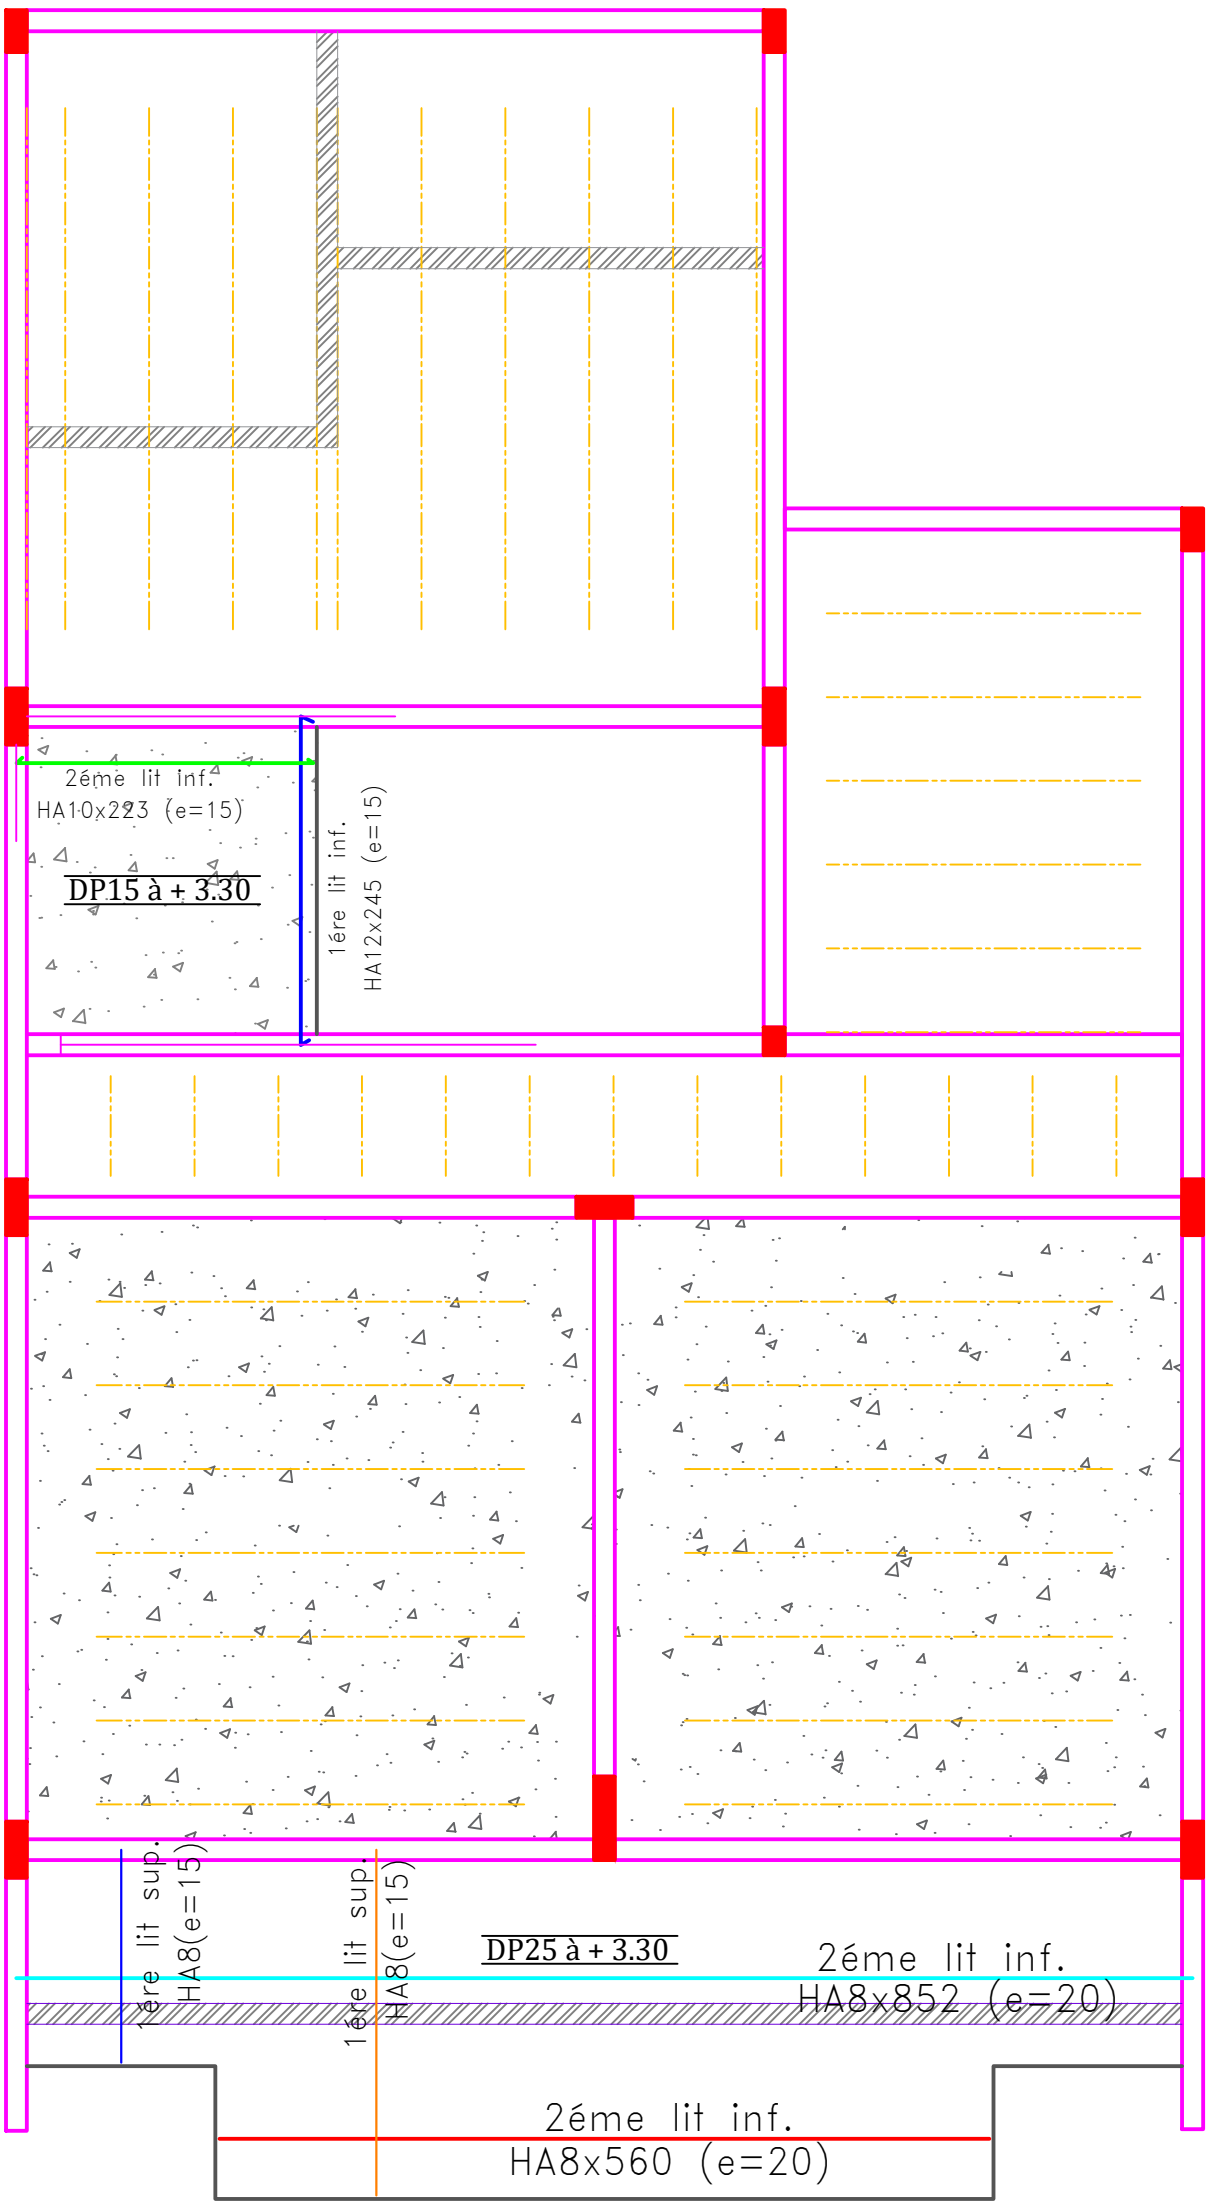


D&F ENGINEERING	**D&F ENGINEERING** **D&F ENGINNERING SARL** **SCAT URBAM VILLA 67H** **17086 DAKAR / LIBERTE** **77 234 03 20/ 76 141 32 23**	**Projet Mohamed BADIANE** FERRAILLAGE DP RDC NAPPE INFERIEURE	N° d' affaire :		N° PLAN
			Indice / Date		Début :
					Dessiné par :MD
					Vérifié par :

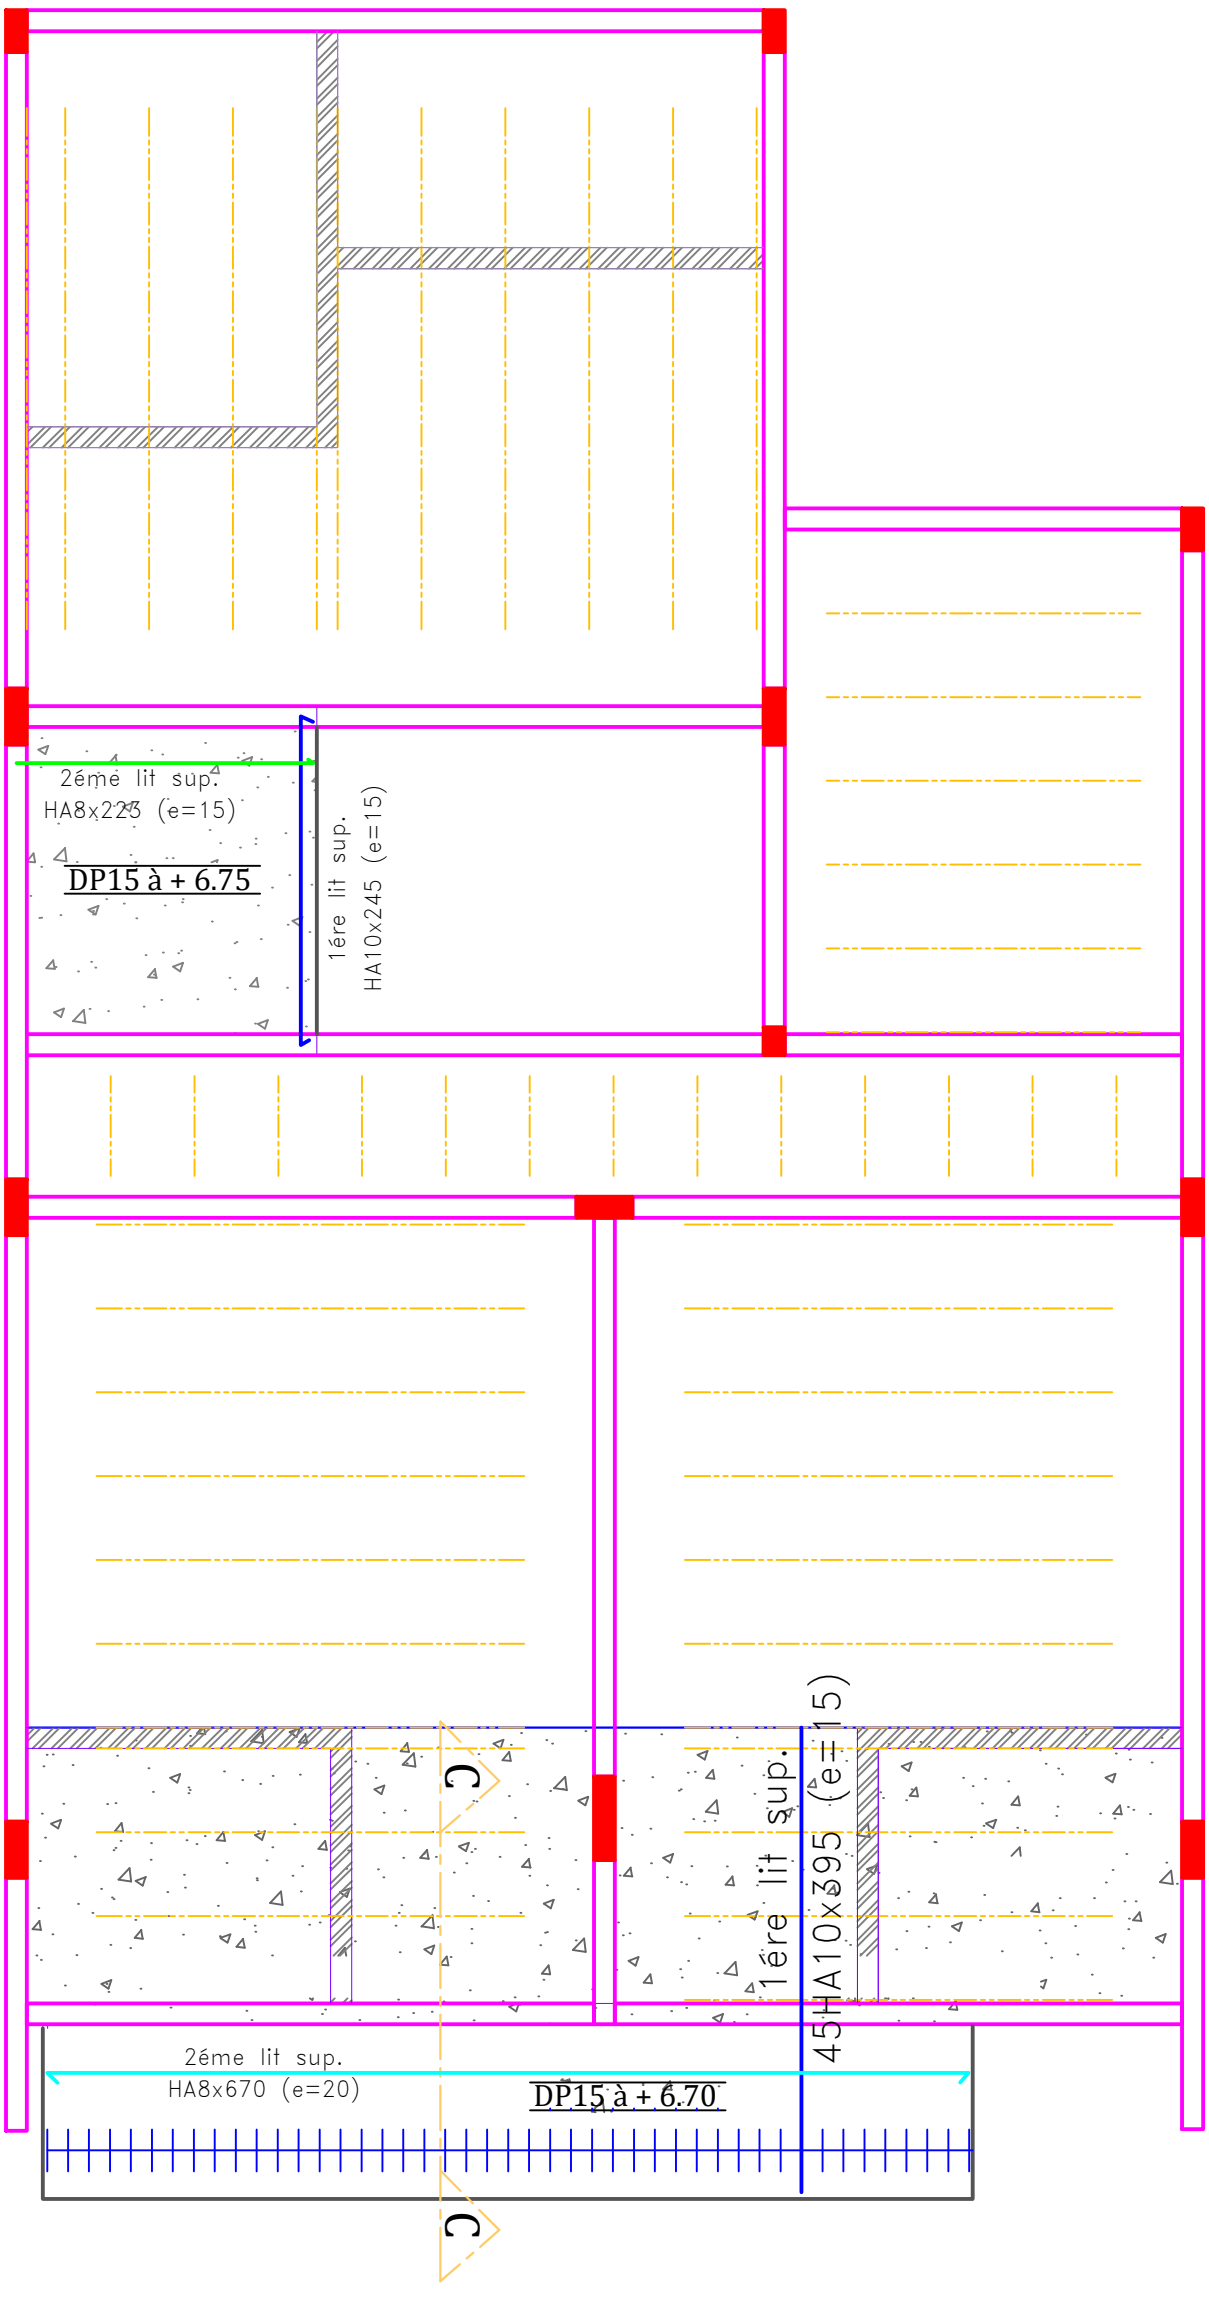


D&F ENGINEERING Confort at home	**D&F ENGINEERING** **D&F ENGINNERING SARL** **SCAT URBAM VILLA 67H** **17086 DAKAR / LIBERTE** **77 234 03 20/ 76 141 32 23**	**Projet Mohamed BADIANE** FERRAILLAGE DP ETAGE NAPPE SUPERIEURE	N° d' affaire :		N° PLAN
			Indice / Date		Début :
					Dessiné par :MD
					Vérifié par :

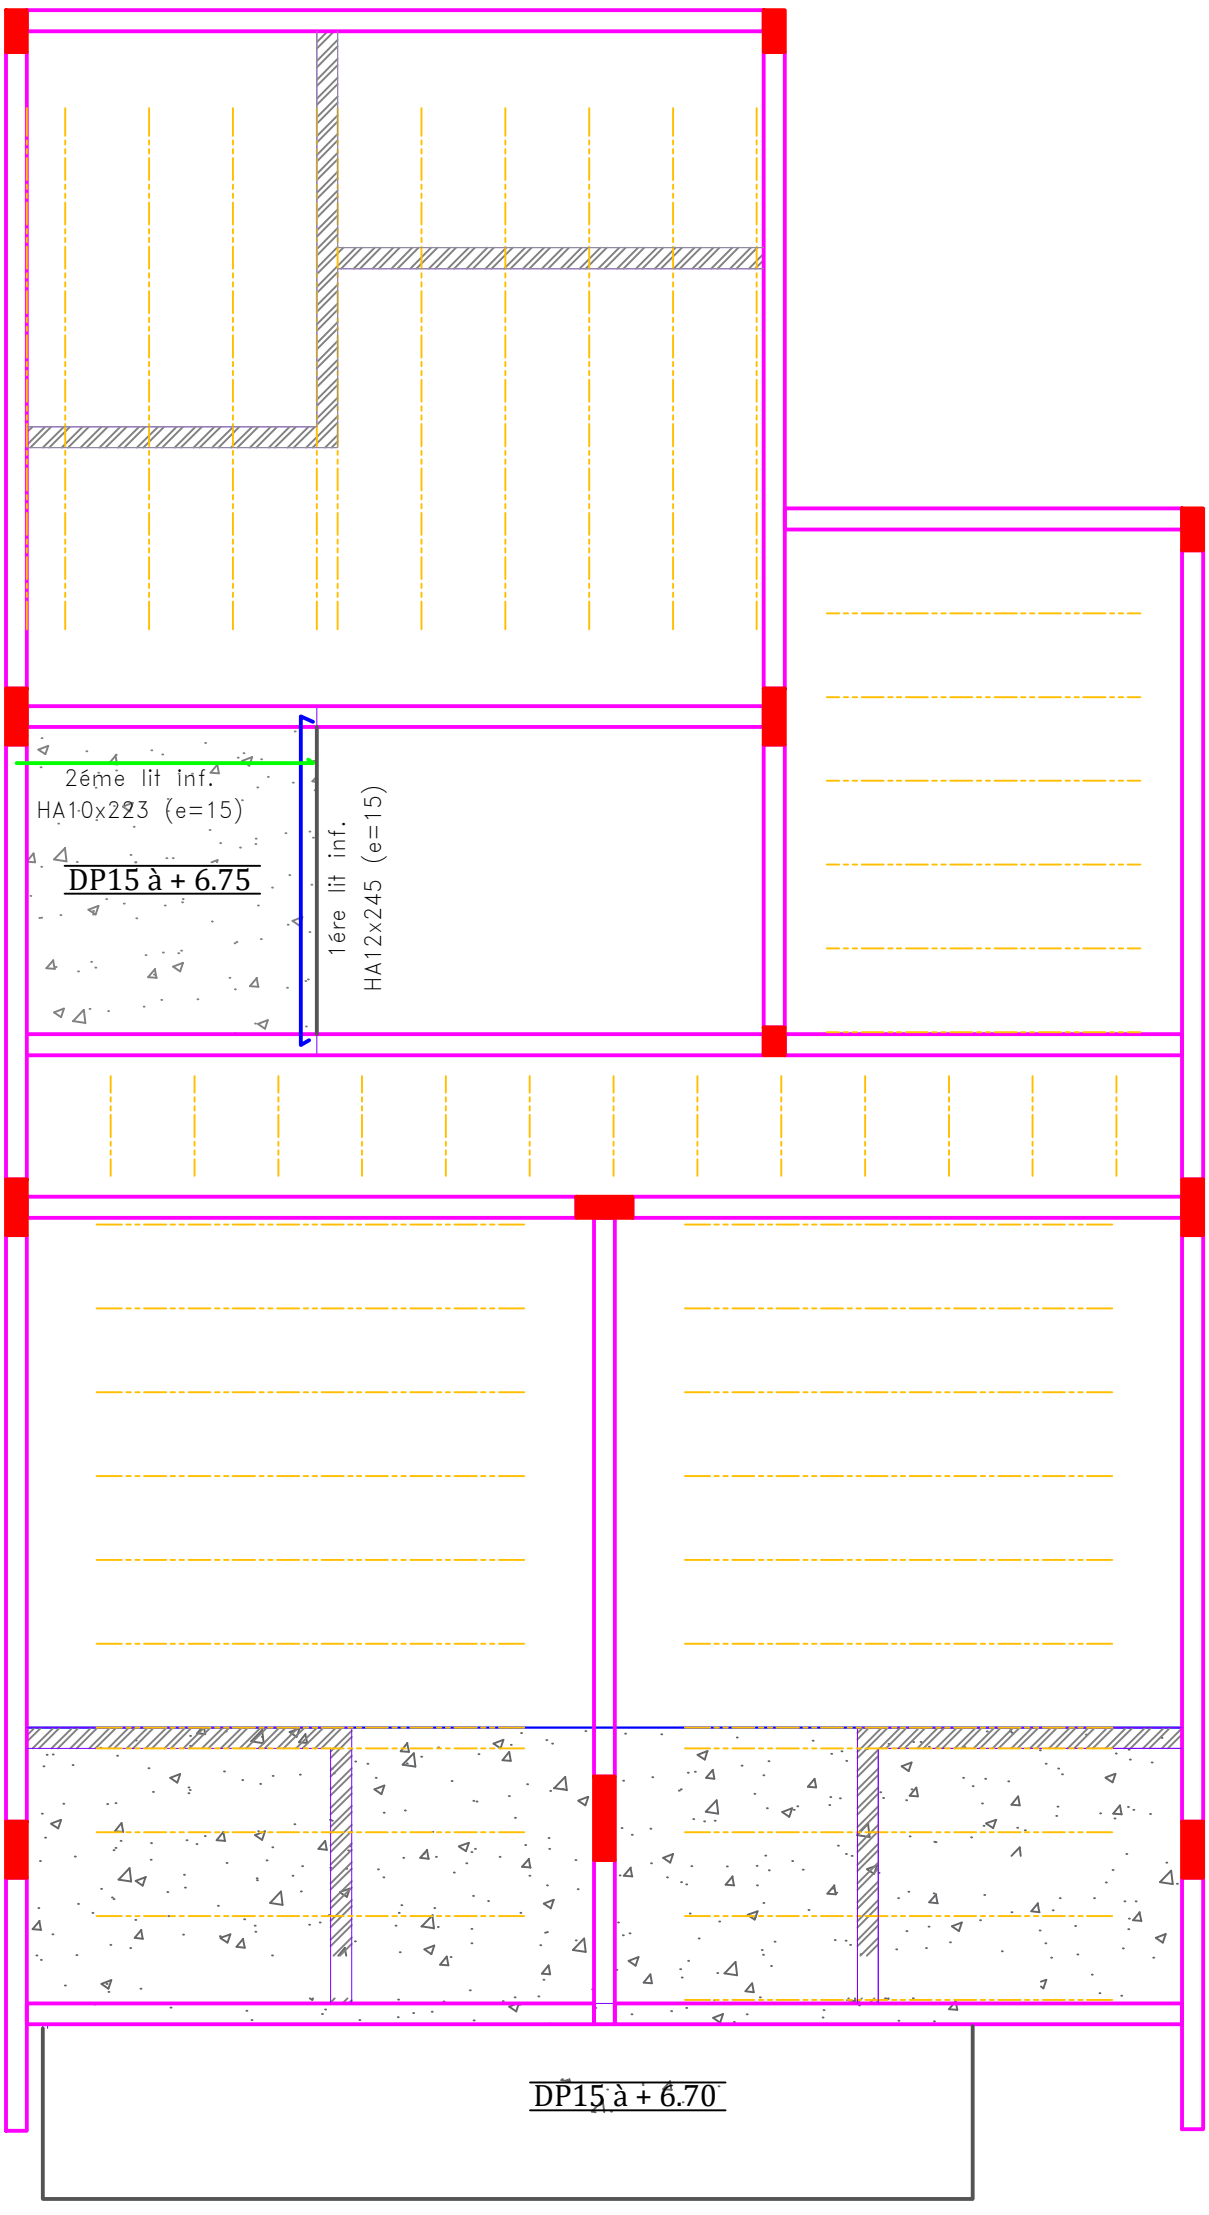


D&F ENGINEERING Confort at home	**D&F ENGINEERING** **D&F ENGINNERING SARL** **SCAT URBAM VILLA 67H** **17086 DAKAR / LIBERTE** **77 234 03 20/ 76 141 32 23**	**Projet Mohamed BADIANE** FERRAILLAGE DP ETAGE NAPPE INFERIEURE	N° d' affaire :		N° PLAN
			Indice / Date		Début :
					Dessiné par :MD
					Vérifié par :

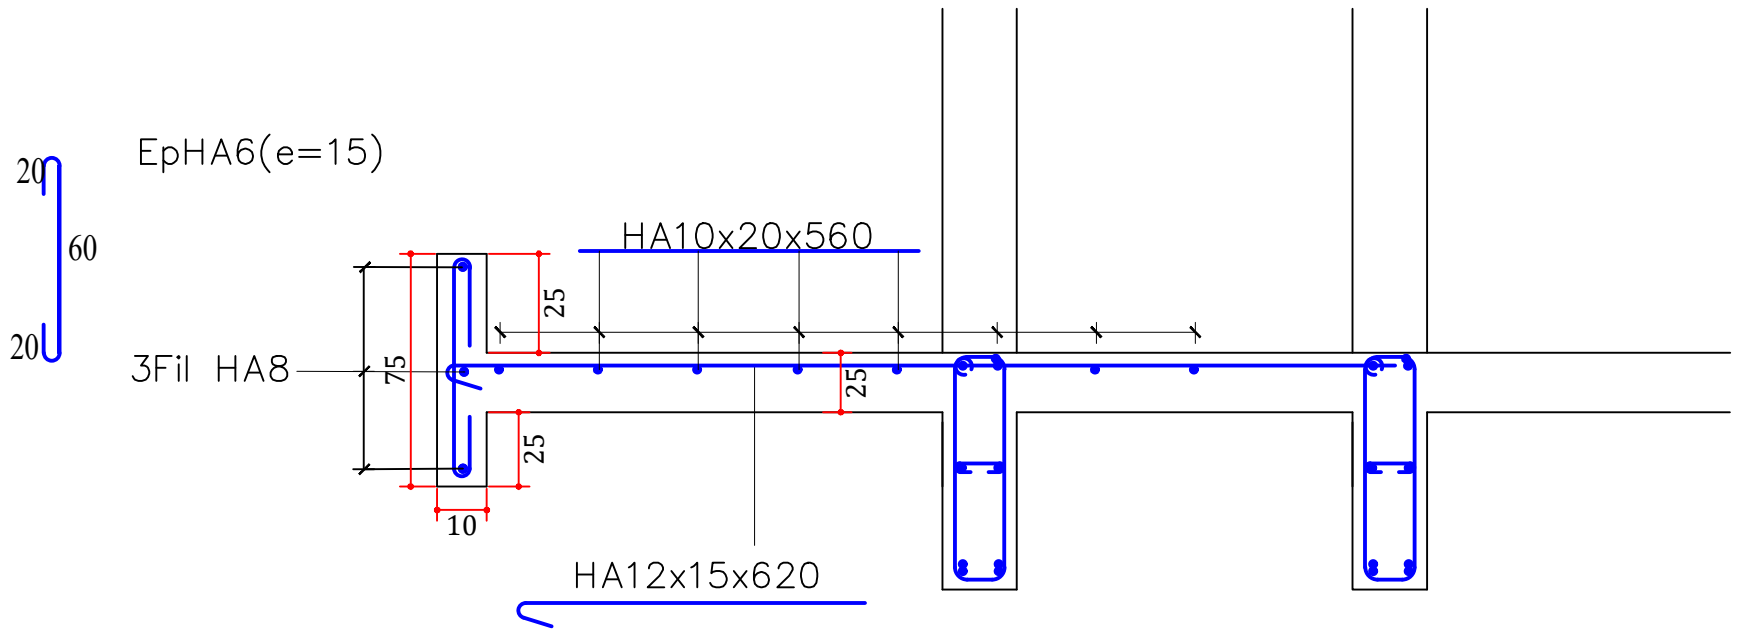

coupe AA

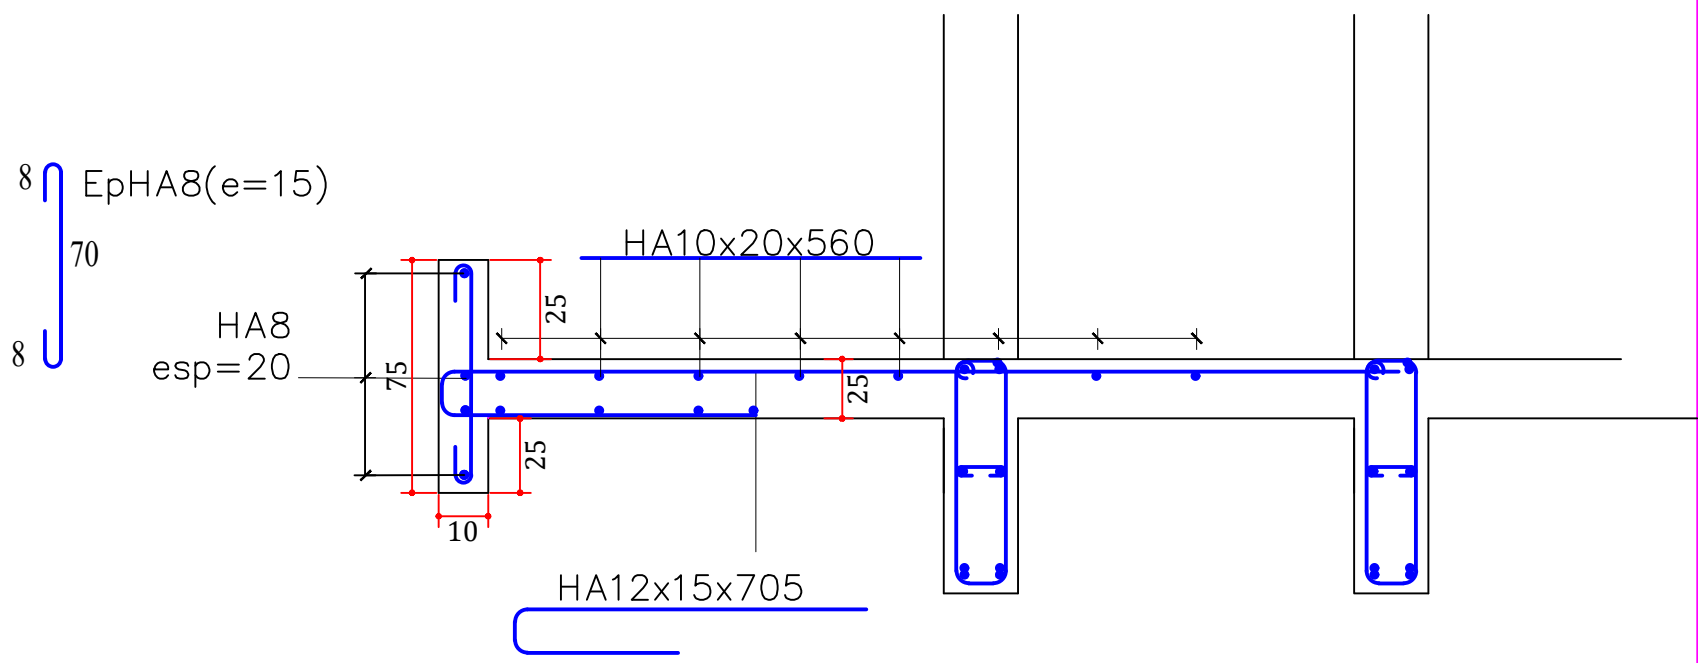

coupe BB

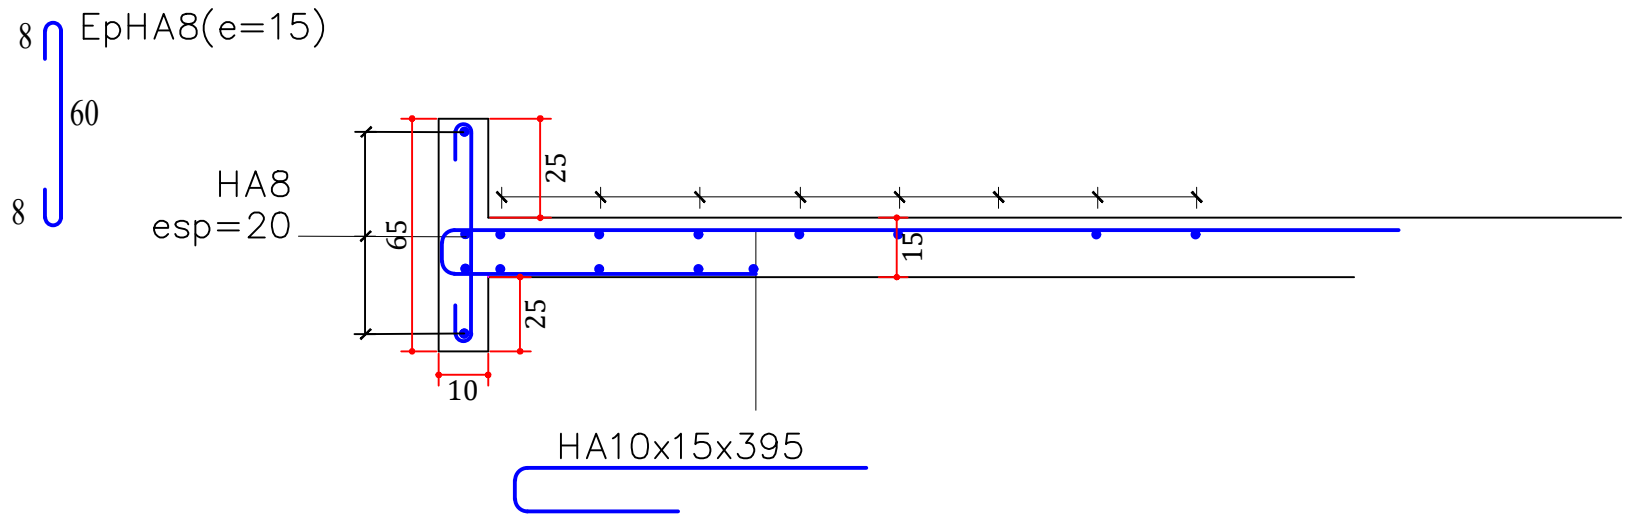

coupe CC

Calcul de plancher hourdis

Projet de construction Mouhamed BADIANE

Etape 3 : Tableau de ferraillage des nervures

<<-- Ajout nervure

Calcul aciers chapeaux -->>

Nervures			Aciers longitudinaux				Cadre (acier 4)		
N°	Type	Nombre	1	2	3	Long	Φ	L4 (m)	esp.(m)
N 2	16+4	7	HA 14	HA 12	HA 8	4,36	HA 6	0,40	0,13
N 3	12+4	13	HA 8	HA 8	HA 8	1,31	HA 6	0,32	0,11
N 4	12+4	5	HA 10	HA 10	HA 8	3,15	HA 6	0,32	0,11
N 5	20+4	10	HA 14	HA 14	HA 8	5,13	HA 6	0,48	0,16