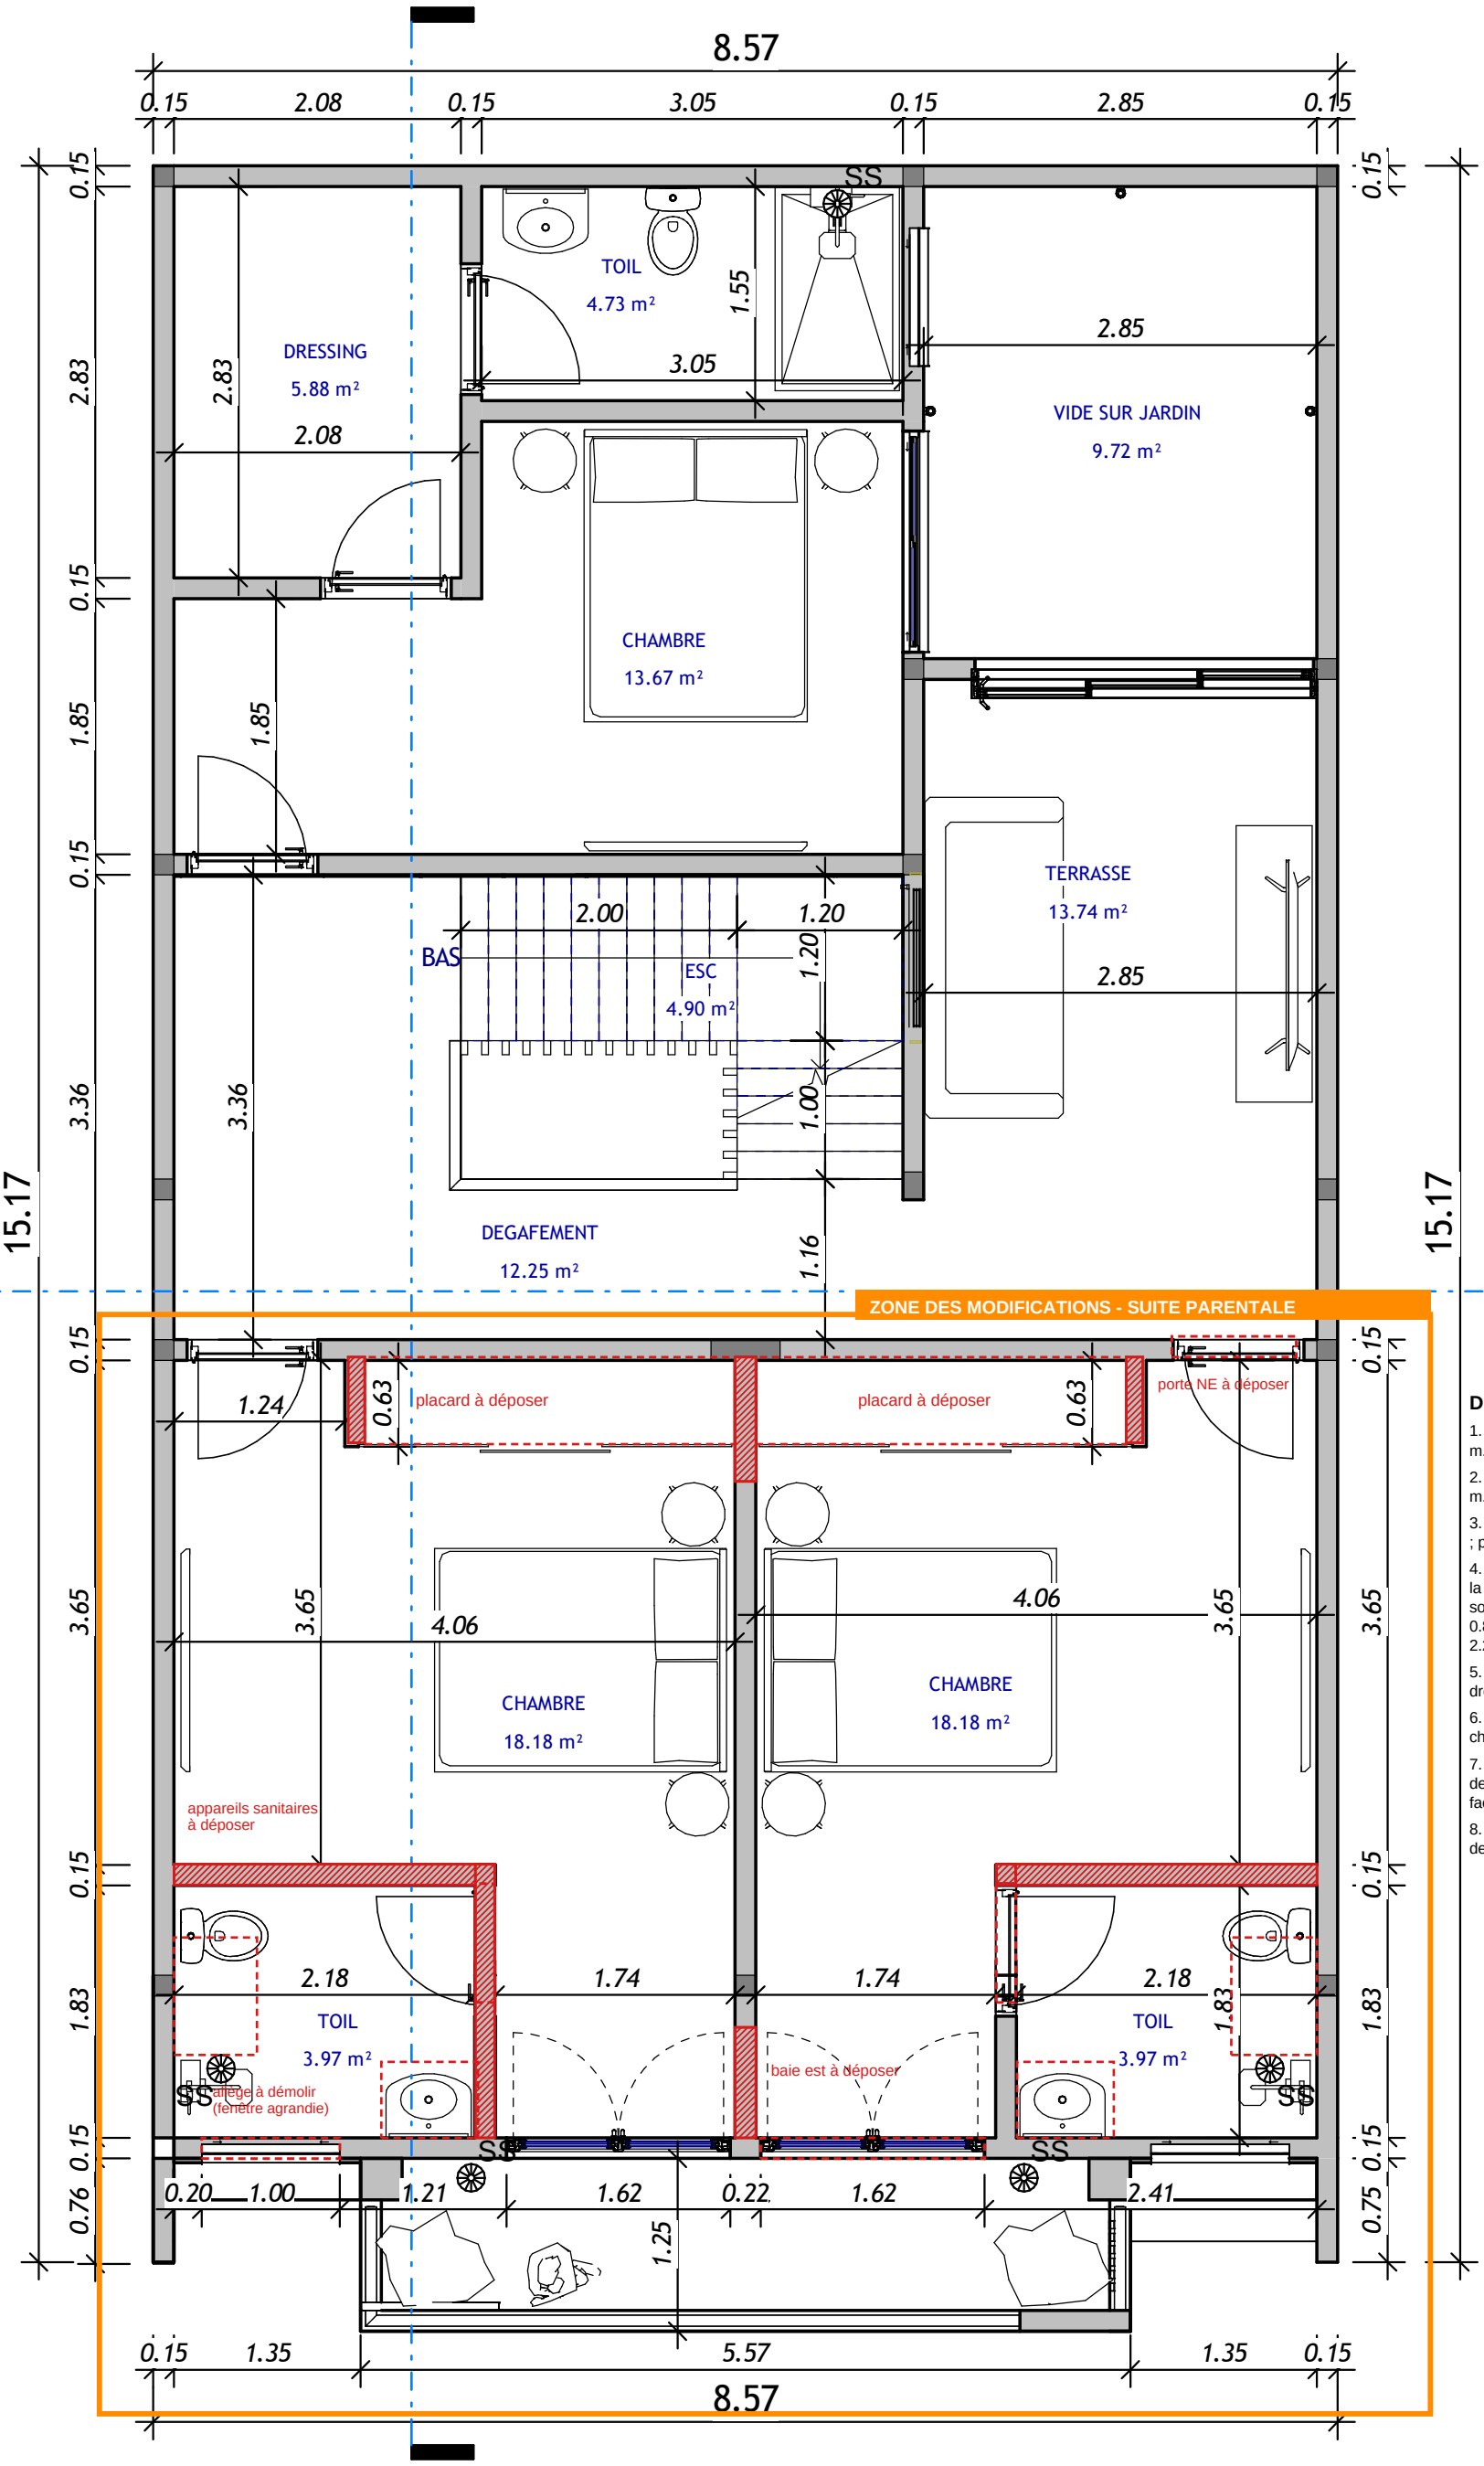


LÉGENDE

Cadre orange : zone des modifications (deux chambres miroirs du R+1).

Hachures rouges : cloison ou mur à démolir.

Pointillé rouge : élément à déposer (placard, sanitaire, porte, baie, allège).

Gris : existant conservé.

Les poteaux, les poutres et les dalles ne sont pas touchés.

DÉMOLITIONS

1. Cloison nord du WC ouest, 2.32 m.
2. Cloison est du WC ouest, 1.98 m.
3. Cloison nord du WC est, 2.32 m ; petit retour du mur ouest, 0.14 m.
4. Deux ouvertures de porte dans la cloison centrale (non porteuse, sous la poutre B14) : côté façade 0.80 m, côté nord 0.90 m, hauteur 2.20, linteaux à prévoir.
5. Deux petits murs de l'ancien dressing : 0.62 m chacun.
6. Placards coulissants des deux chambres.
7. Appareils sanitaires, deux portes de WC, porte NE, baie est de façade.
8. Allège de la fenêtre du WC ouest, de 1.60 à 0.95 (fenêtre agrandie).

Maitre d'ouvrage:

Mohamed BADIANE


Projet:

PROJET DE CONSTRUCTION D UNE VILLA RESIDENTIELLE SIS A MBAO

Titre: R+1 - DEMOLITIONS

02/11/26	DWG No: 016	Cad APS
DWR E.H.S.F	ECH: 1 : 50	

D&F ENGINEERING
Confort et home
Tel (+221) 76-141-32-23
Tel (+221) 77-234-03-20
Email: dnfengineeringsav@gmail.com

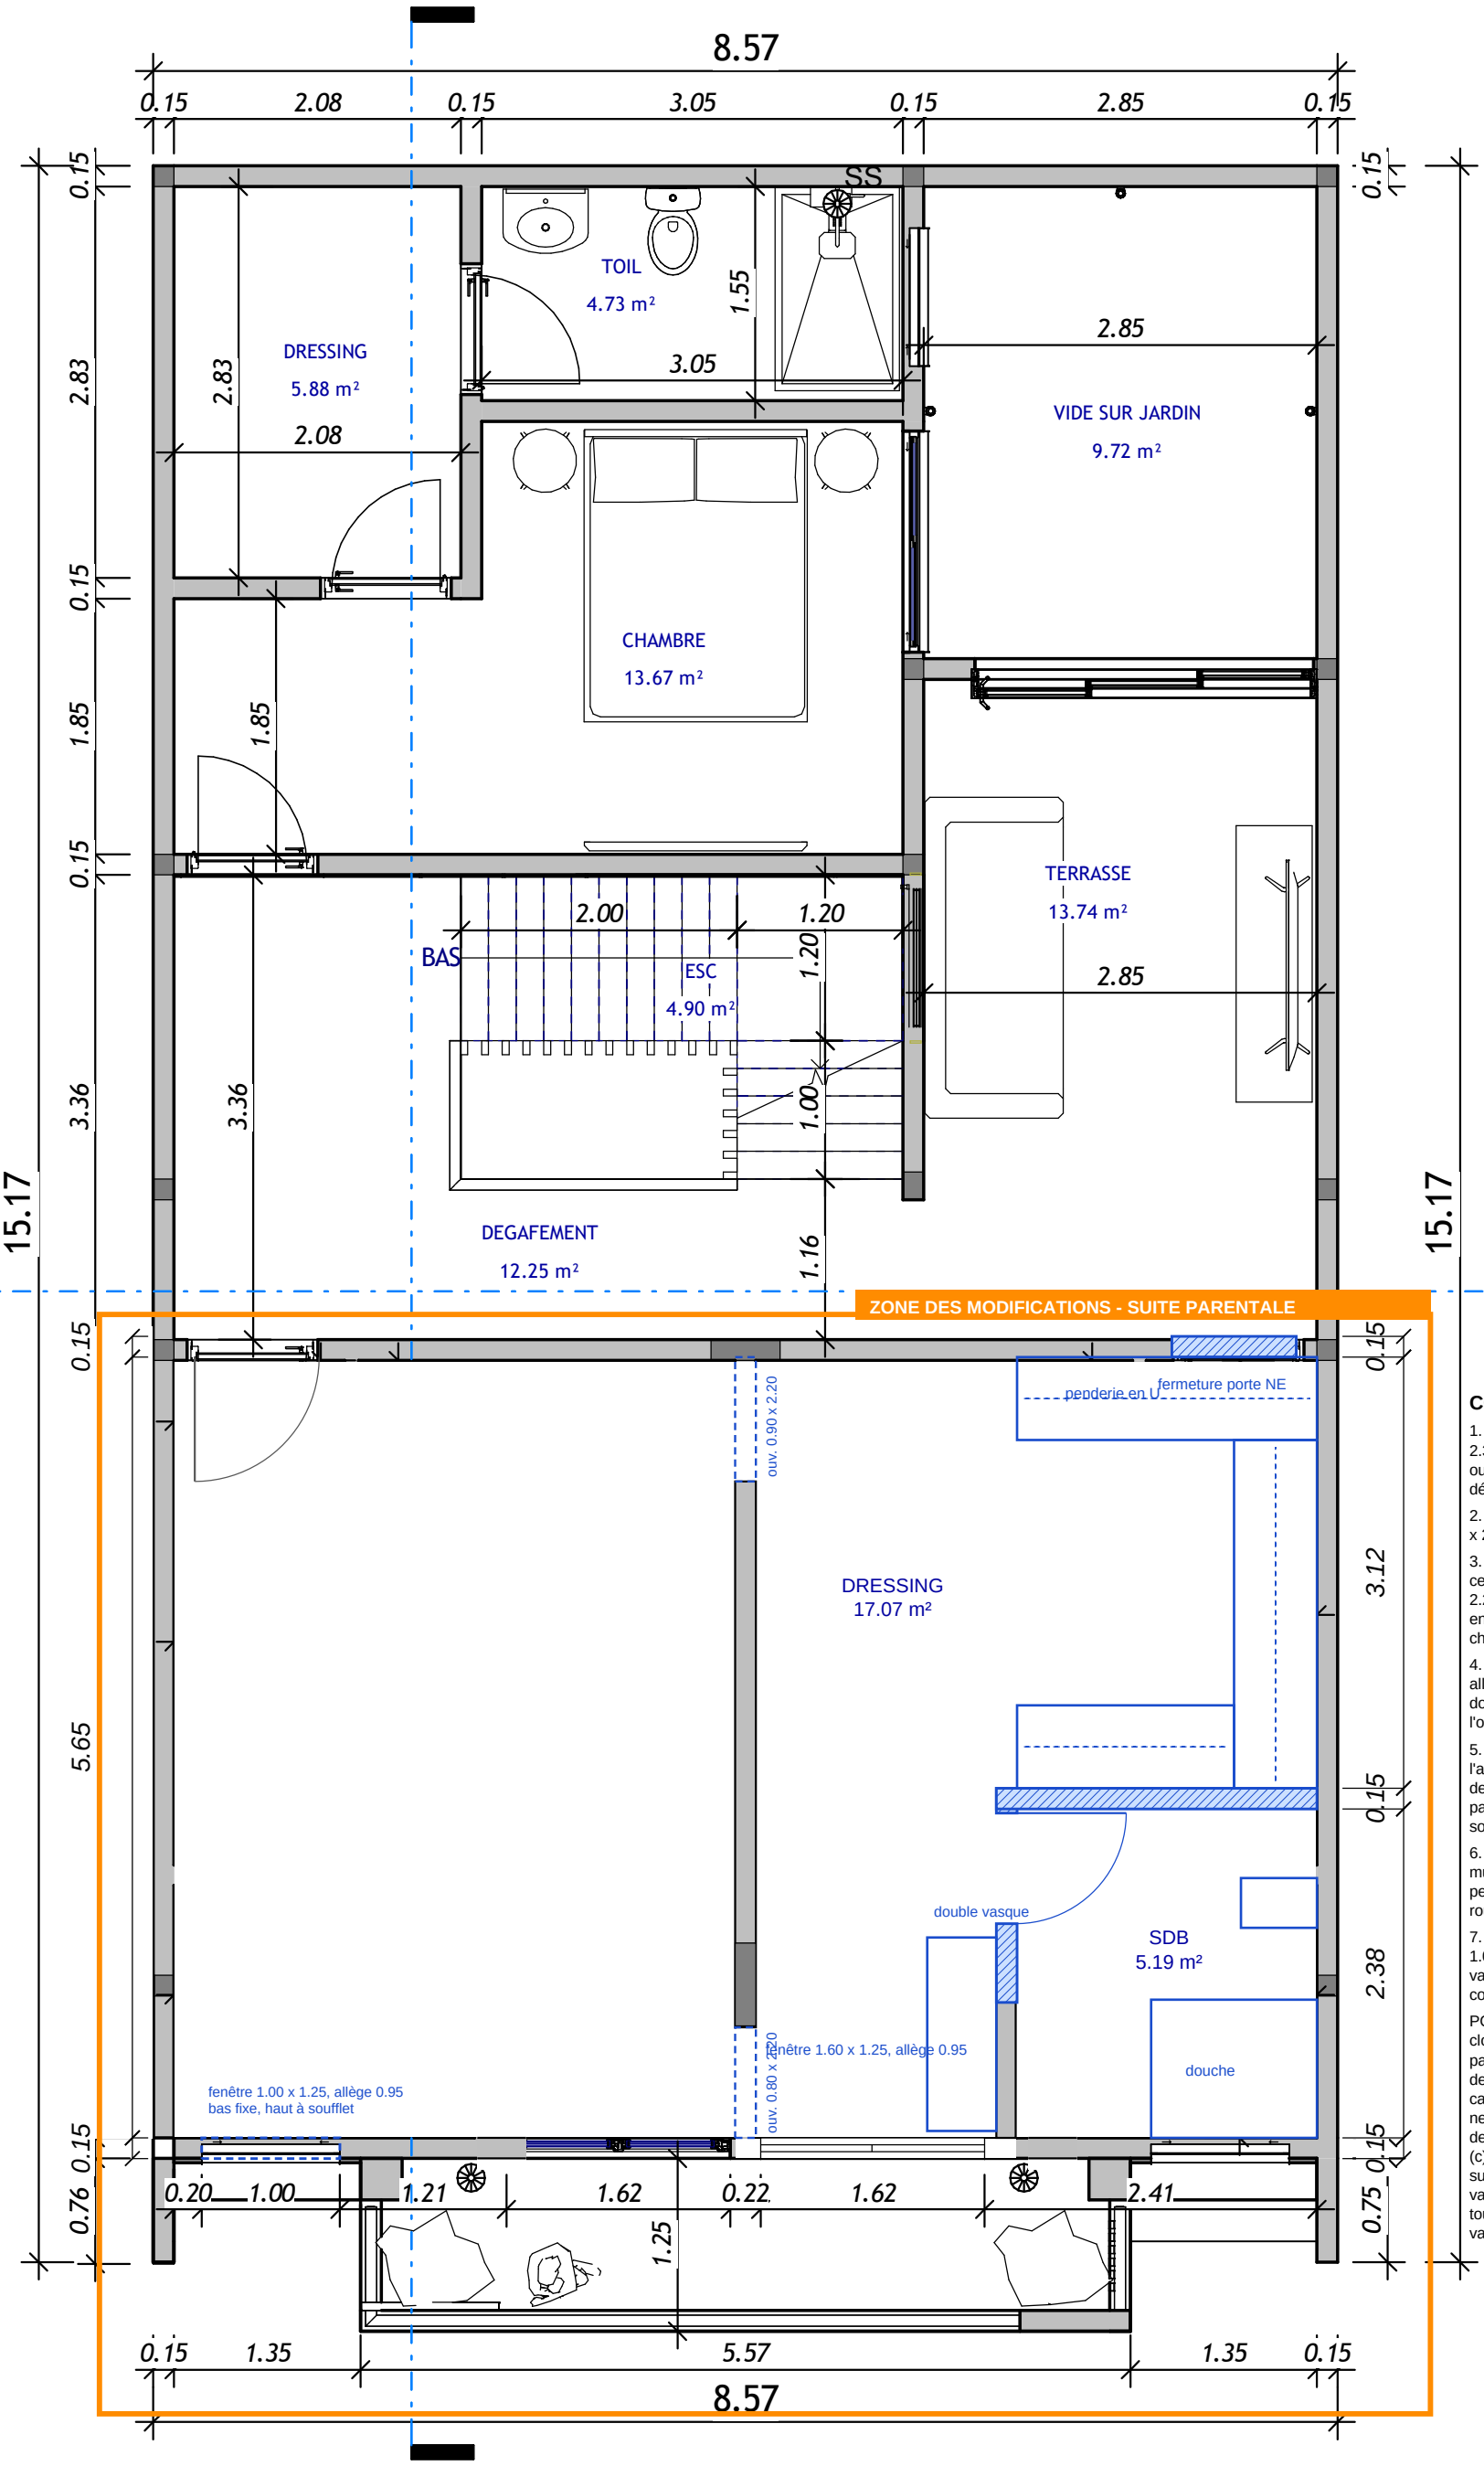

LÉGENDE

Cadre orange : zone des modifications (deux chambres miroirs du R+1).

Bleu hachuré : mur ou cloison à construire (épaisseur 0.15).

Contour bleu : menuiserie, appareil ou agencement neuf.

Gris : existant conservé.

Mobilier non figuré (voir le projet final).

CONSTRUCTIONS

1. Cloison nord de la salle de bain, 2.32 m, à 2.38 de la façade ; mur ouest prolongé de 1.22 m (porte déplacée à 1.55-2.35).

2. Fermeture de la porte NE (0.90 x 2.20) en maçonnerie.

3. Deux ouvertures dans la cloison centrale, 0.80 et 0.90 de large, 2.20 de haut, avec linteaux : on entre et on sort du dressing de chaque côté.

4. Fenêtre du dressing 1.60 x 1.25, allège 0.95 (à la hauteur de la double vasque), tête 2.20, dans l'ouverture de la baie est (1.62).

5. Fenêtre de la chambre : l'ancienne fenêtre du WC ouest devient 1.00 x 1.25, allège 0.95 : partie basse fixe, partie haute à soufflet.

6. Double vasque 1.40 contre le mur ouest de la salle de bain ; penderie en U limitée à la ligne rouge, sans îlot.

7. Salle de bain : douche 1.20 x 1.00 et WC suspendu, sans vasque ; porte 0.80, vantail ouvert contre le mur nord.

POINTS DE L'INGÉNIEUR : (a) cloison nord de la salle de bain parallèle aux nervures 12+8, à 0.55 de l'ancienne : poutrelle doublée ou calcul de charge ; (b) linteaux neufs de la porte 1.55-2.35 et des deux ouvertures, appuis de 0.20 ; (c) attentes de plomberie à relever sur site (WC déplacé, double vasque) ; (d) étanchéité sous faïence toute hauteur derrière la double vasque et la douche.

Maitre d'ouvrage:

Mohamed BADIANE


Projet:

PROJET DE CONSTRUCTION D UNE VILLA RESIDENTIELLE SIS A MBAO

Titre: R+1 - CONSTRUCTIONS

02/11/26	DWG No: 017	Cad APS
DWR E.H.S.F	ECH: 1 : 50	

D&F ENGINEERING
Confort at home
Tel (+221) 76-141-32-23
Tel (+221) 77-234-03-20
Email: dnfengineeringsav@gmail.com

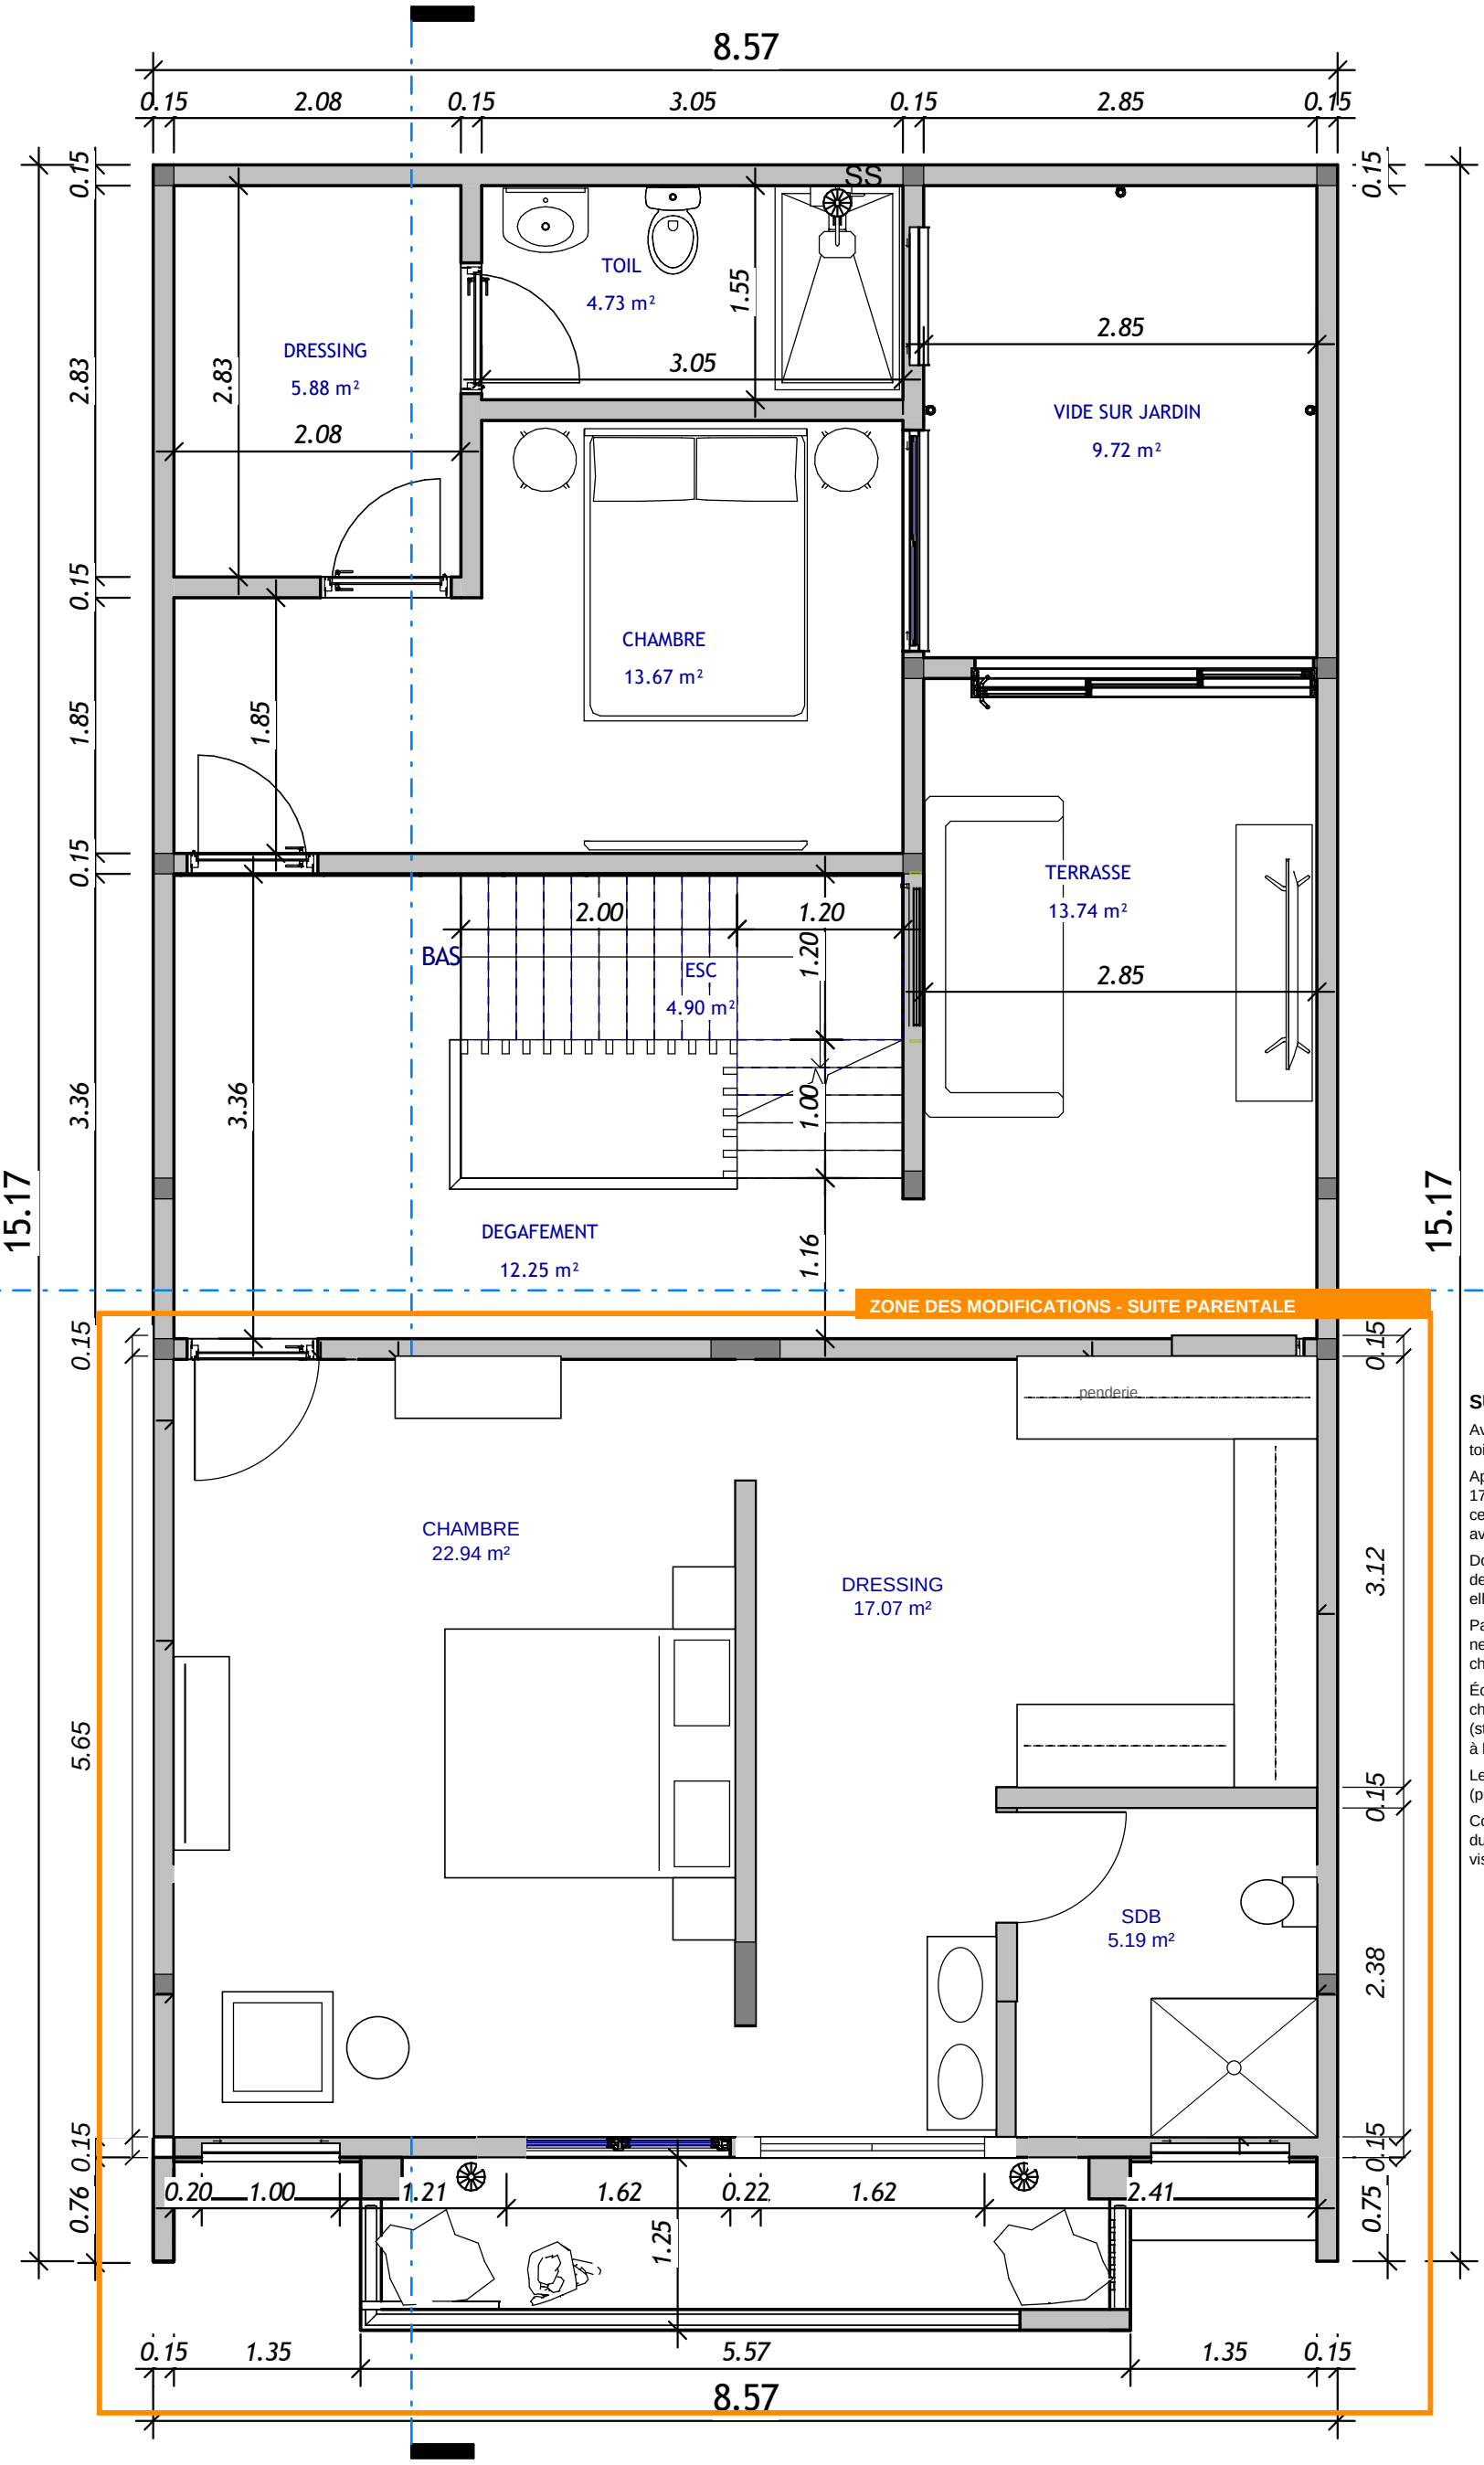

LÉGENDE

Cadre orange : zone des modifications (deux chambres miroirs du R+1 transformées en une suite parentale).

Parcours : chambre, dressing, salle de bain ; on entre et on sort du dressing par deux ouvertures de porte (0.80 côté façade, 0.90 côté nord).

Lumière et air naturels : fenêtre 1.60 x 1.25 pour le dressing, fenêtre 1.00 x 1.25 pour la chambre (bas fixe, haut à soufflet), fenêtre 1.00 pour la salle de bain (châssis fixe dépoli ou soufflet haut au-dessus de la douche).

SURFACES NETTES (m²)

Avant : 2 chambres de 18.18 et 2 toilettes de 3.97.

Après : chambre 22.94 ; dressing 17.07 (hall et penderie en U, allée centrale 1.92) ; salle de bain 5.19, avec WC et douche seulement.

Double vasque 1.40 contre le mur de la salle de bain, côté dressing : elle sert de lave-mains.

Pas d'îlot : un îlot de 1.00 de large ne laisse pas 0.90 de passage de chaque côté.

Écart au standard : fenêtre de chambre de 1.00 de large (standard 1.40 ou 1.60), conservée à la demande du client.

Le WC n'est pas en cabinet fermé (pièce de 2.17 x 2.38).

Cotes en mètres. Plan sous réserve du relevé des attentes sur site et du visa de l'ingénieur de structure.

Maitre d'ouvrage:

Mohamed BADIANE

Projet:

PROJET DE CONSTRUCTION D UNE VILLA RESIDENTIELLE SIS A MBAO

Titre: R+1 - PROJET FINAL

02/11/26	DWG No: 018	Cad APS
DWR E.H.S.F	ECH: 1 : 50	

D&F ENGINEERING
Confort at home
Tel (+221) 76-141-32-23
Tel (+221) 77-234-03-20
Email: dnfengineeringsav@gmail.com