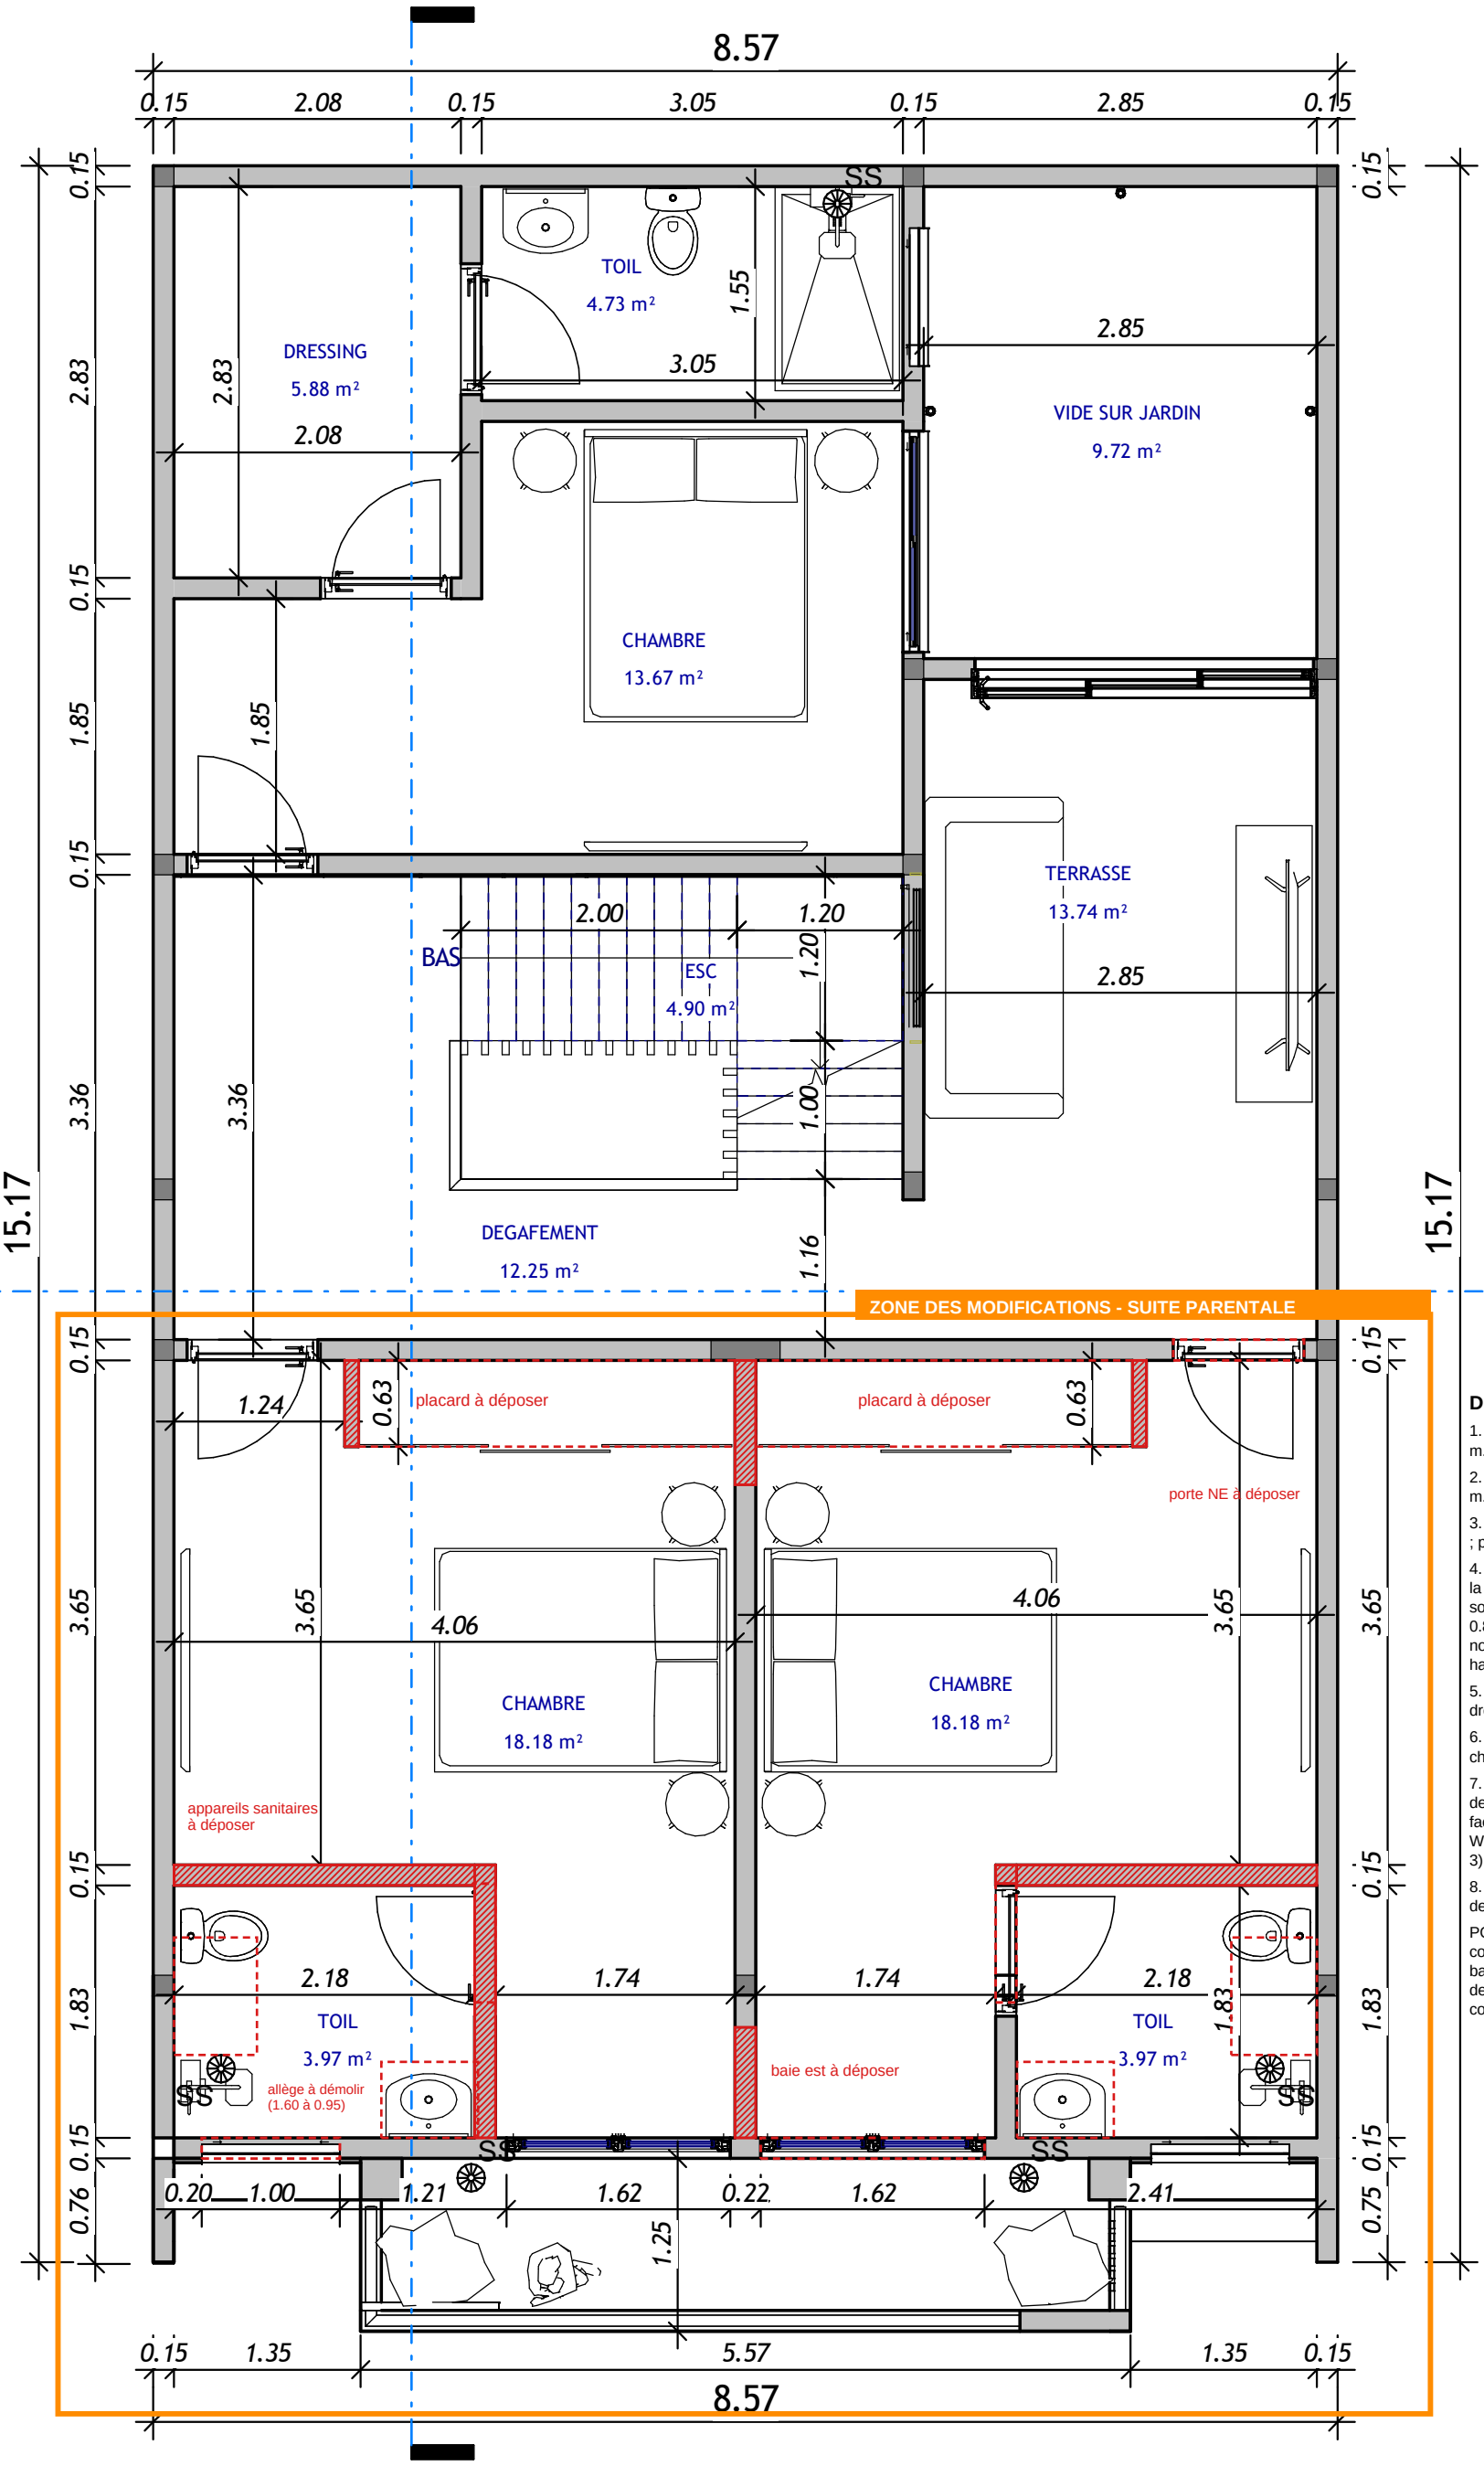


LÉGENDE

Cadre orange : zone des modifications (deux chambres miroirs du R+1).

Hachures rouges : cloison ou mur à démolir.

Pointillé rouge : élément à déposer (placard, sanitaire, porte, baie, allège).

Gris : existant conservé.

Les poteaux, les poutres et les dalles ne sont pas touchés.

DÉMOLITIONS

1. Cloison nord du WC ouest, 2.32 m.
2. Cloison est du WC ouest, 1.98 m.
3. Cloison nord du WC est, 2.32 m ; petit retour du mur ouest, 0.14 m.
4. Deux ouvertures de porte dans la cloison centrale (non porteuse, sous la poutre B14) : côté façade 0.80 m (sous la poutre C4), côté nord 0.90 m (sous la poutre B14), hauteur 2.20, linteaux à prévoir.
5. Deux petits murs de l'ancien dressing : 0.62 m chacun.
6. Placards coulissants des deux chambres.
7. Appareils sanitaires, deux portes de WC, porte NE, baie est de façade ; repères « SS » des anciens WC supprimés au projet (pages 2 et 3).
8. Allège de la fenêtre du WC ouest, de 1.60 à 0.95 (fenêtre agrandie).

POINT DE L'INGÉNIEUR : sur le coffrage du plancher haut, des bandes hachurées passent au droit des cloisons des WC : nature à confirmer avant la démolition.

Maitre d'ouvrage:

Mohamed BADIANE


Projet:

PROJET DE CONSTRUCTION D UNE VILLA RESIDENTIELLE SIS A MBAO

Titre: R+1 - DEMOLITIONS - IND. E

03/11/26	DWG No: 016	Cad APS
DWR E.H.S.F	ECH: 1 : 50	

D&F ENGINEERING
Confort at home
Tel (+221) 76-141-32-23
Tel (+221) 77-234-03-20
Email: dnfengineeringsav@gmail.com

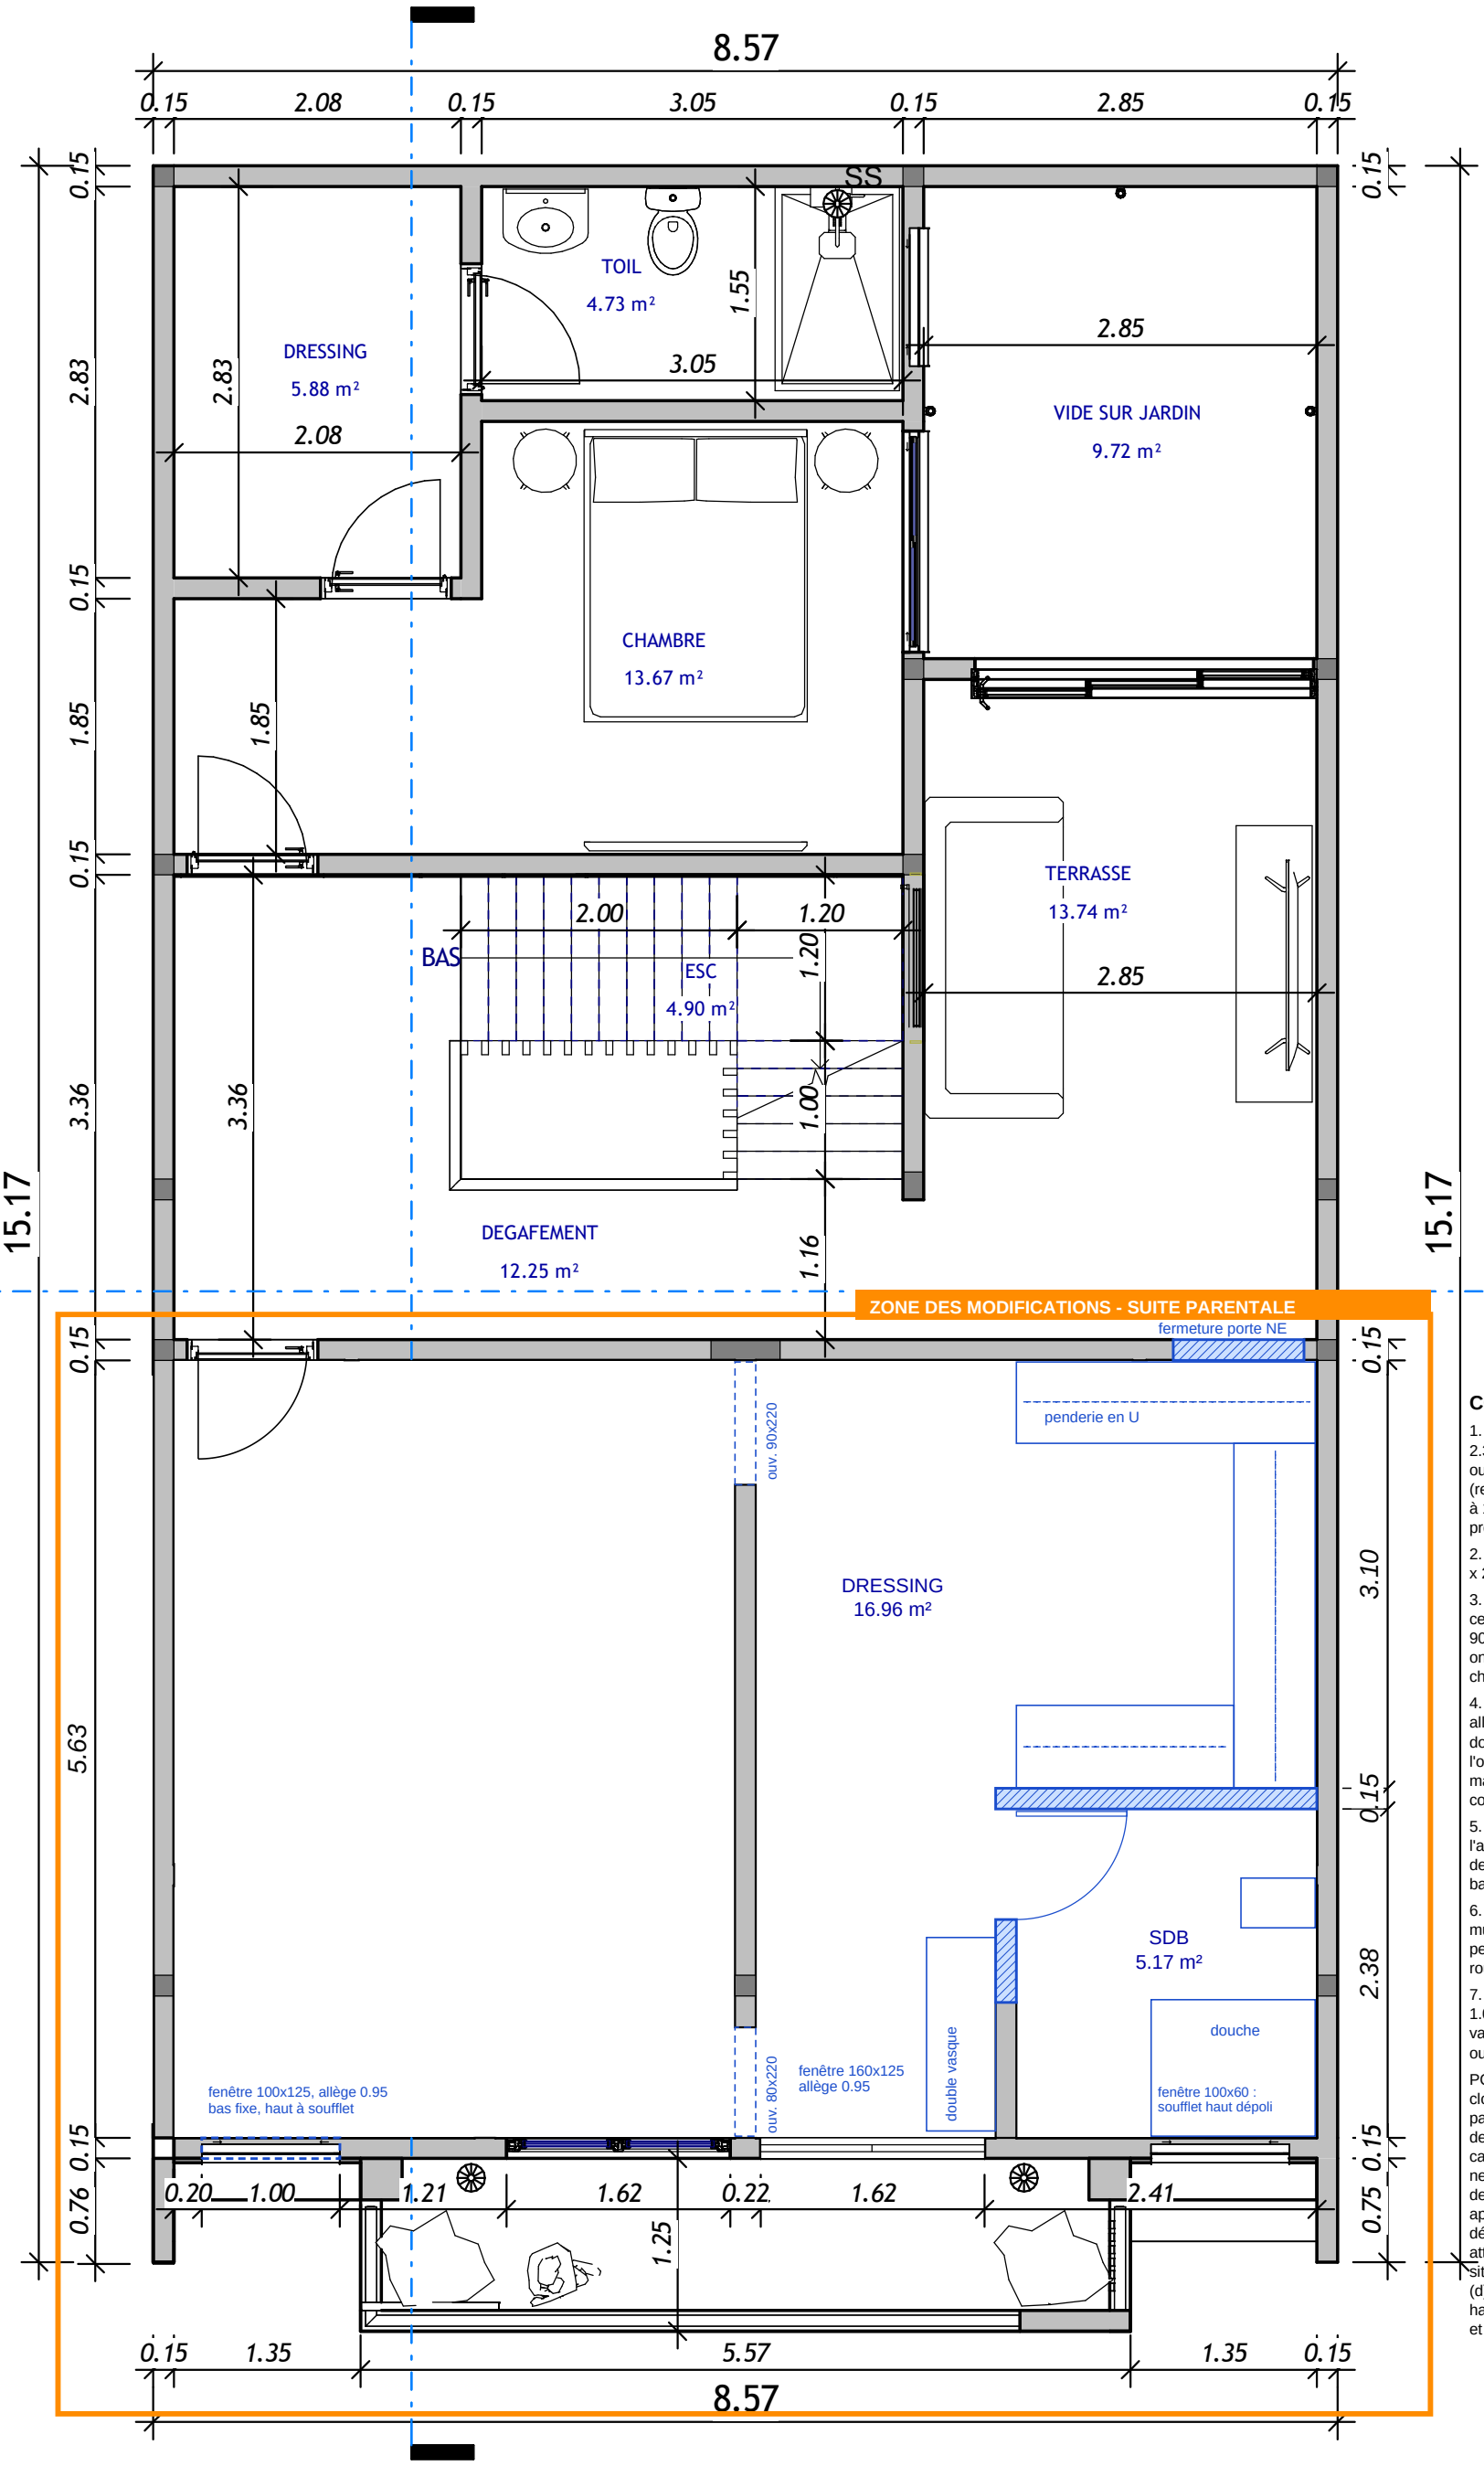

LÉGENDE

Cadre orange : zone des modifications (deux chambres miroirs du R+1).

Bleu hachuré : mur ou cloison à construire (épaisseur 0.15).

Contour bleu : menuiserie, appareil ou agencement neuf.

Gris : existant conservé.

Mobilier libre non figuré (voir le projet final).

CONSTRUCTIONS

1. Cloison nord de la salle de bain, 2.32 m, à 2.38 de la façade ; mur ouest prolongé de 0.60 m (rebouchage de 0.60 ; porte déplacée à 1.58-2.38, jambage dans le prolongement du mur nord).

2. Fermeture de la porte NE (0.90 x 2.20) en maçonnerie.

3. Deux ouvertures dans la cloison centrale, 80x220 (côté façade) et 90x220 (côté nord), avec linteaux : on entre et on sort du dressing de chaque côté ; sans porte.

4. Fenêtre du dressing 160x125, allège 0.95 (à la hauteur de la double vasque), tête 2.20, dans l'ouverture de la baie est (162) : maçonnerie d'allège 1.62 x 0.95 à construire.

5. Fenêtre de la chambre : l'ancienne fenêtre du WC ouest devient 100x125, allège 0.95 : partie basse fixe, partie haute à soufflet.

6. Double vasque 1.40 contre le mur ouest de la salle de bain ; penderie en U limitée à la ligne rouge, sans îlot.

7. Salle de bain : douche 1.20 x 1.00 et WC suspendu, sans vasque ; porte 80x220, vantail ouvert contre le mur nord.

POINTS DE L'INGÉNIEUR : (a) cloison nord de la salle de bain parallèle aux nervures 12+8, à 0.55 de l'ancienne : poutrelle doublée ou calcul de charge ; (b) linteaux neufs de la porte 1.55-2.35 et des deux ouvertures (sous C4 et B14), appuis de 0.20, joints de désolidarisation sous poutre ; (c) attentes de plomberie à relever sur site (WC déplacé, double vasque) ; (d) étanchéité sous faïence toute hauteur derrière la double vasque et la douche.

Maitre d'ouvrage:

Mohamed BADIANE


Projet:

PROJET DE CONSTRUCTION D UNE VILLA RESIDENTIELLE SIS A MBAO

Titre: R+1 - CONSTRUCTIONS - IND. E

03/11/26	DWG No: 017	Cad APS
DWR E.H.S.F	ECH: 1 : 50	

D&F ENGINEERING
Confort et home
Tel (+221) 76-141-32-23
Tel (+221) 77-234-03-20
Email: dnfengineeringsav@gmail.com

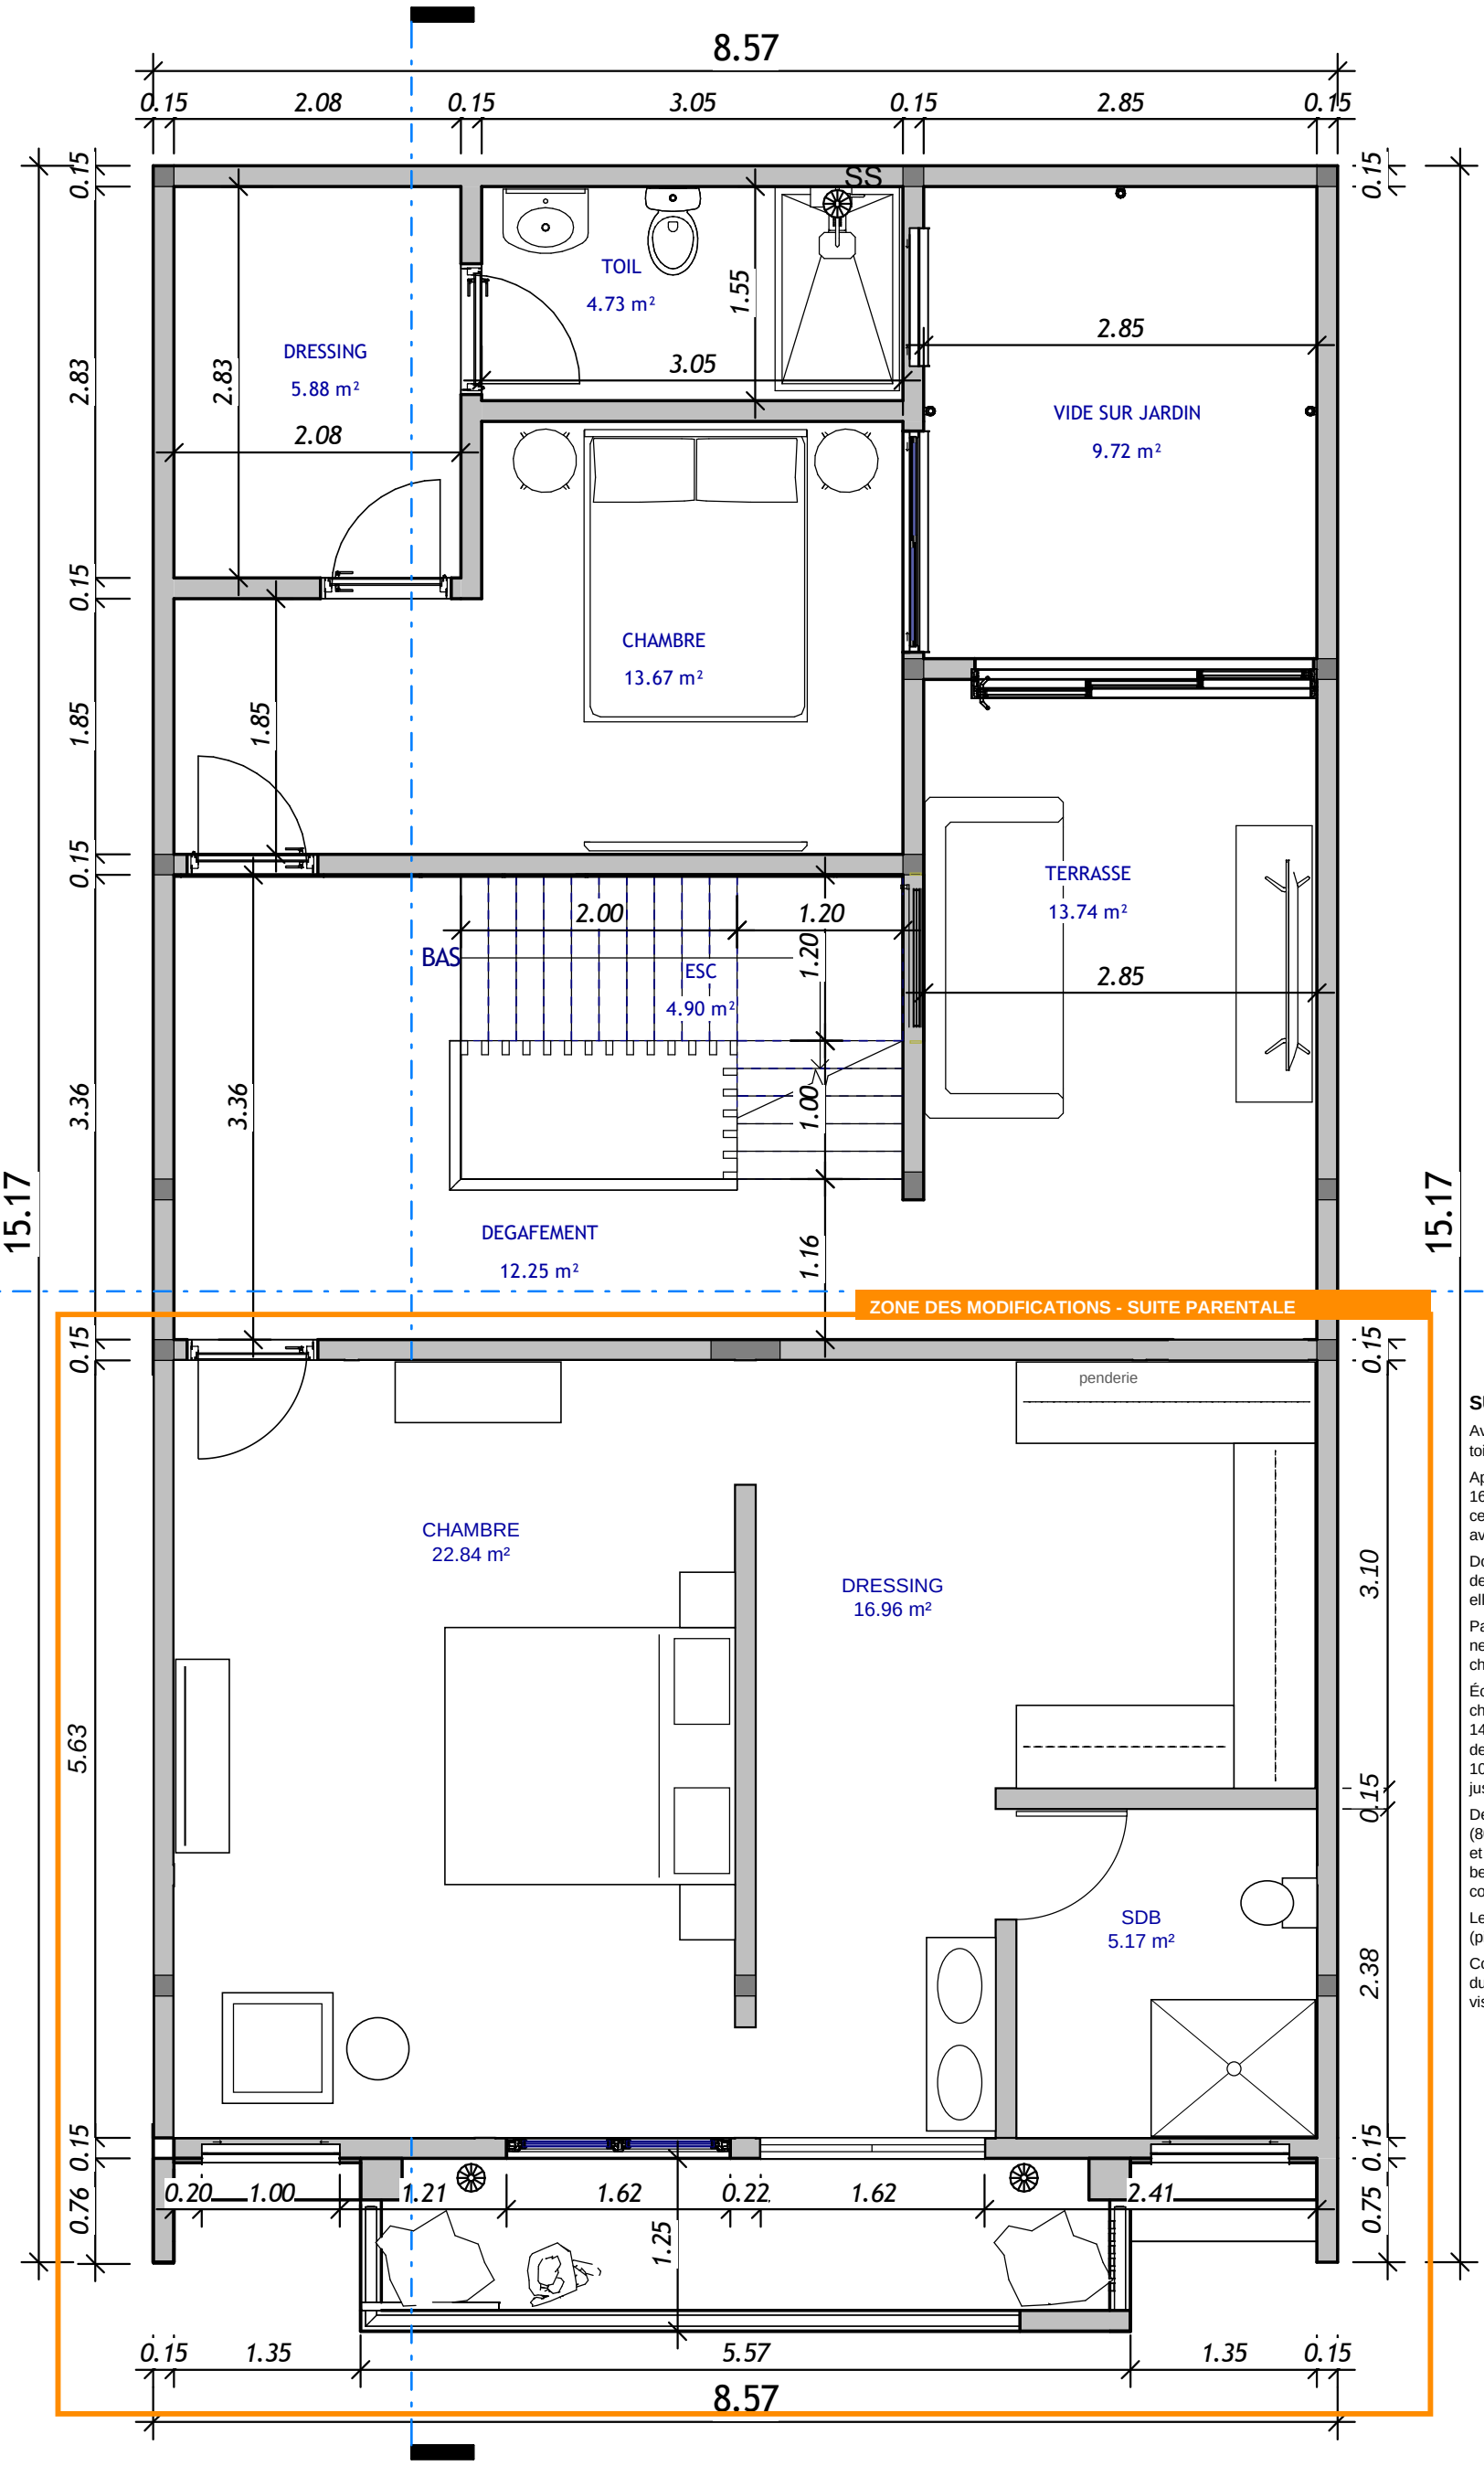

LÉGENDE

Cadre orange : zone des modifications (deux chambres miroirs du R+1 transformées en une suite parentale).

Parcours : chambre, dressing, salle de bain ; on entre et on sort du dressing par deux ouvertures de porte (0.80 côté façade, 0.90 côté nord).

Lumière et air naturels : fenêtre 160x125 pour le dressing, fenêtre 100x125 pour la chambre (bas fixe, haut à soufflet), fenêtre 100x60 à soufflet haut dépoli pour la salle de bain, au-dessus de la douche.

SURFACES NETTES (m²)

Avant : 2 chambres de 18.18 et 2 toilettes de 3.97.

Après : chambre 22.84 ; dressing 16.96 (hall et penderie en U, allée centrale 1.92) ; salle de bain 5.17, avec WC et douche seulement.

Double vasque 1.40 contre le mur de la salle de bain, côté dressing : elle sert de lave-mains.

Pas d'îlot : un îlot de 1.00 de large ne laisse pas 0.90 de passage de chaque côté.

Écart au standard : fenêtre de chambre de 100 de large (standard 140 ou 160), conservée à la demande du client ; lue comme 100x125, allège 0.95 (une lecture jusqu'au sol est possible).

Deux ouvertures sans porte (80x220 et 90x220) : intimité du lit et de la salle de bain à traiter si besoin. Baie ouest : porte-fenêtre coulissante, conservée.

Le WC n'est pas en cabinet fermé (pièce de 2.17 x 2.38).

Cotes en mètres. Plan sous réserve du relevé des attentes sur site et du visa de l'ingénieur de structure.

Maitre d'ouvrage:

Mohamed BADIANE

Projet:

PROJET DE CONSTRUCTION D UNE VILLA RESIDENTIELLE SIS A MBAO

Titre: R+1 - PROJET FINAL - IND. E

03/11/26	DWG No: 018	Cad APS
DWR E.H.S.F	ECH: 1 : 50	

D&F ENGINEERING
Confort at home
Tel (+221) 76-141-32-23
Tel (+221) 77-234-03-20
Email: dnfengineeringsav@gmail.com